



TOP-CAP LED CHANNEL — SECTION

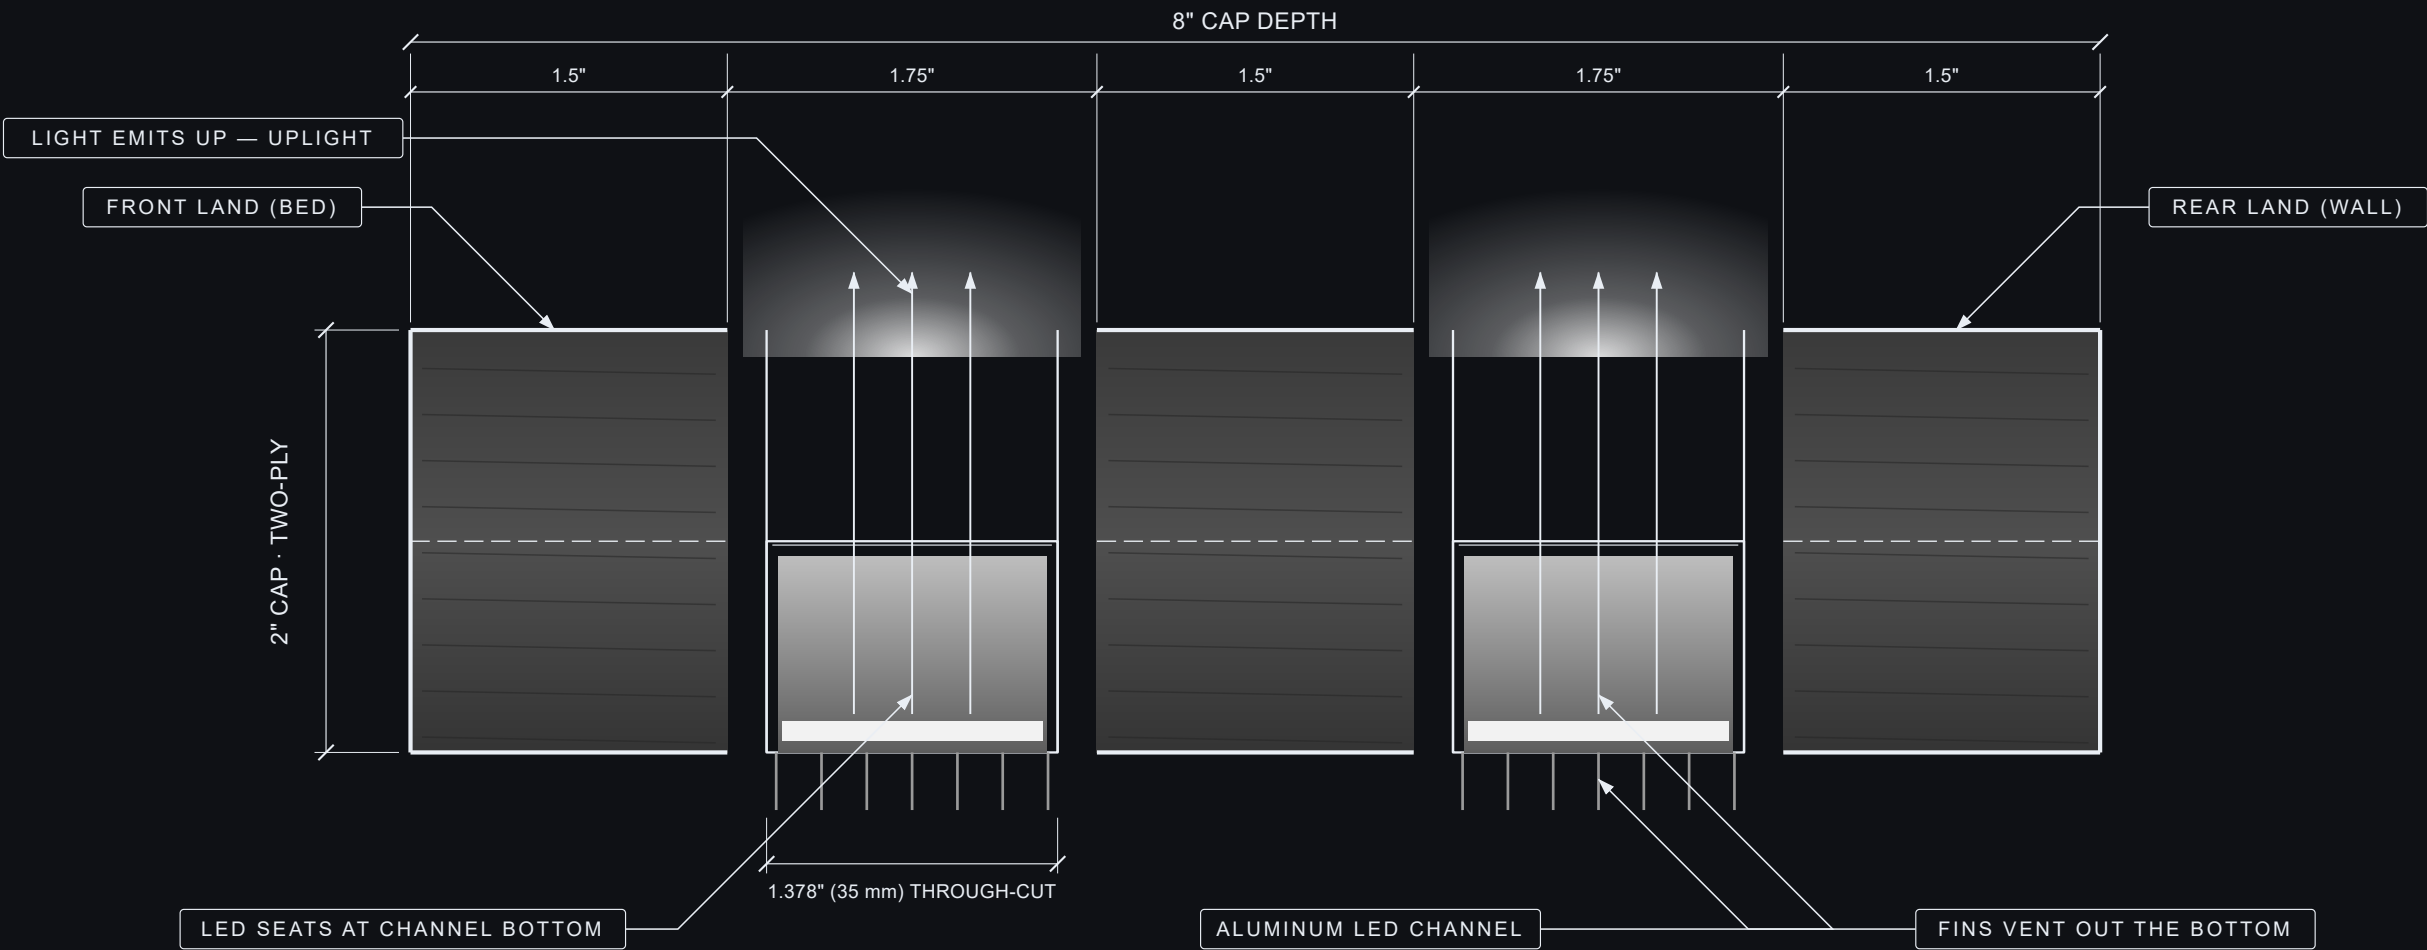


PROJECT	HEIRLOOM BED	SHEET 1 OF 2
DRAWING NO.	TopCap-LED_Blueprint	
LAST UPDATE	2026-06-19 12:30 PM	REV 1.21

TOP-CAP — CONTINUOUS 130" RUN (ISOMETRIC)

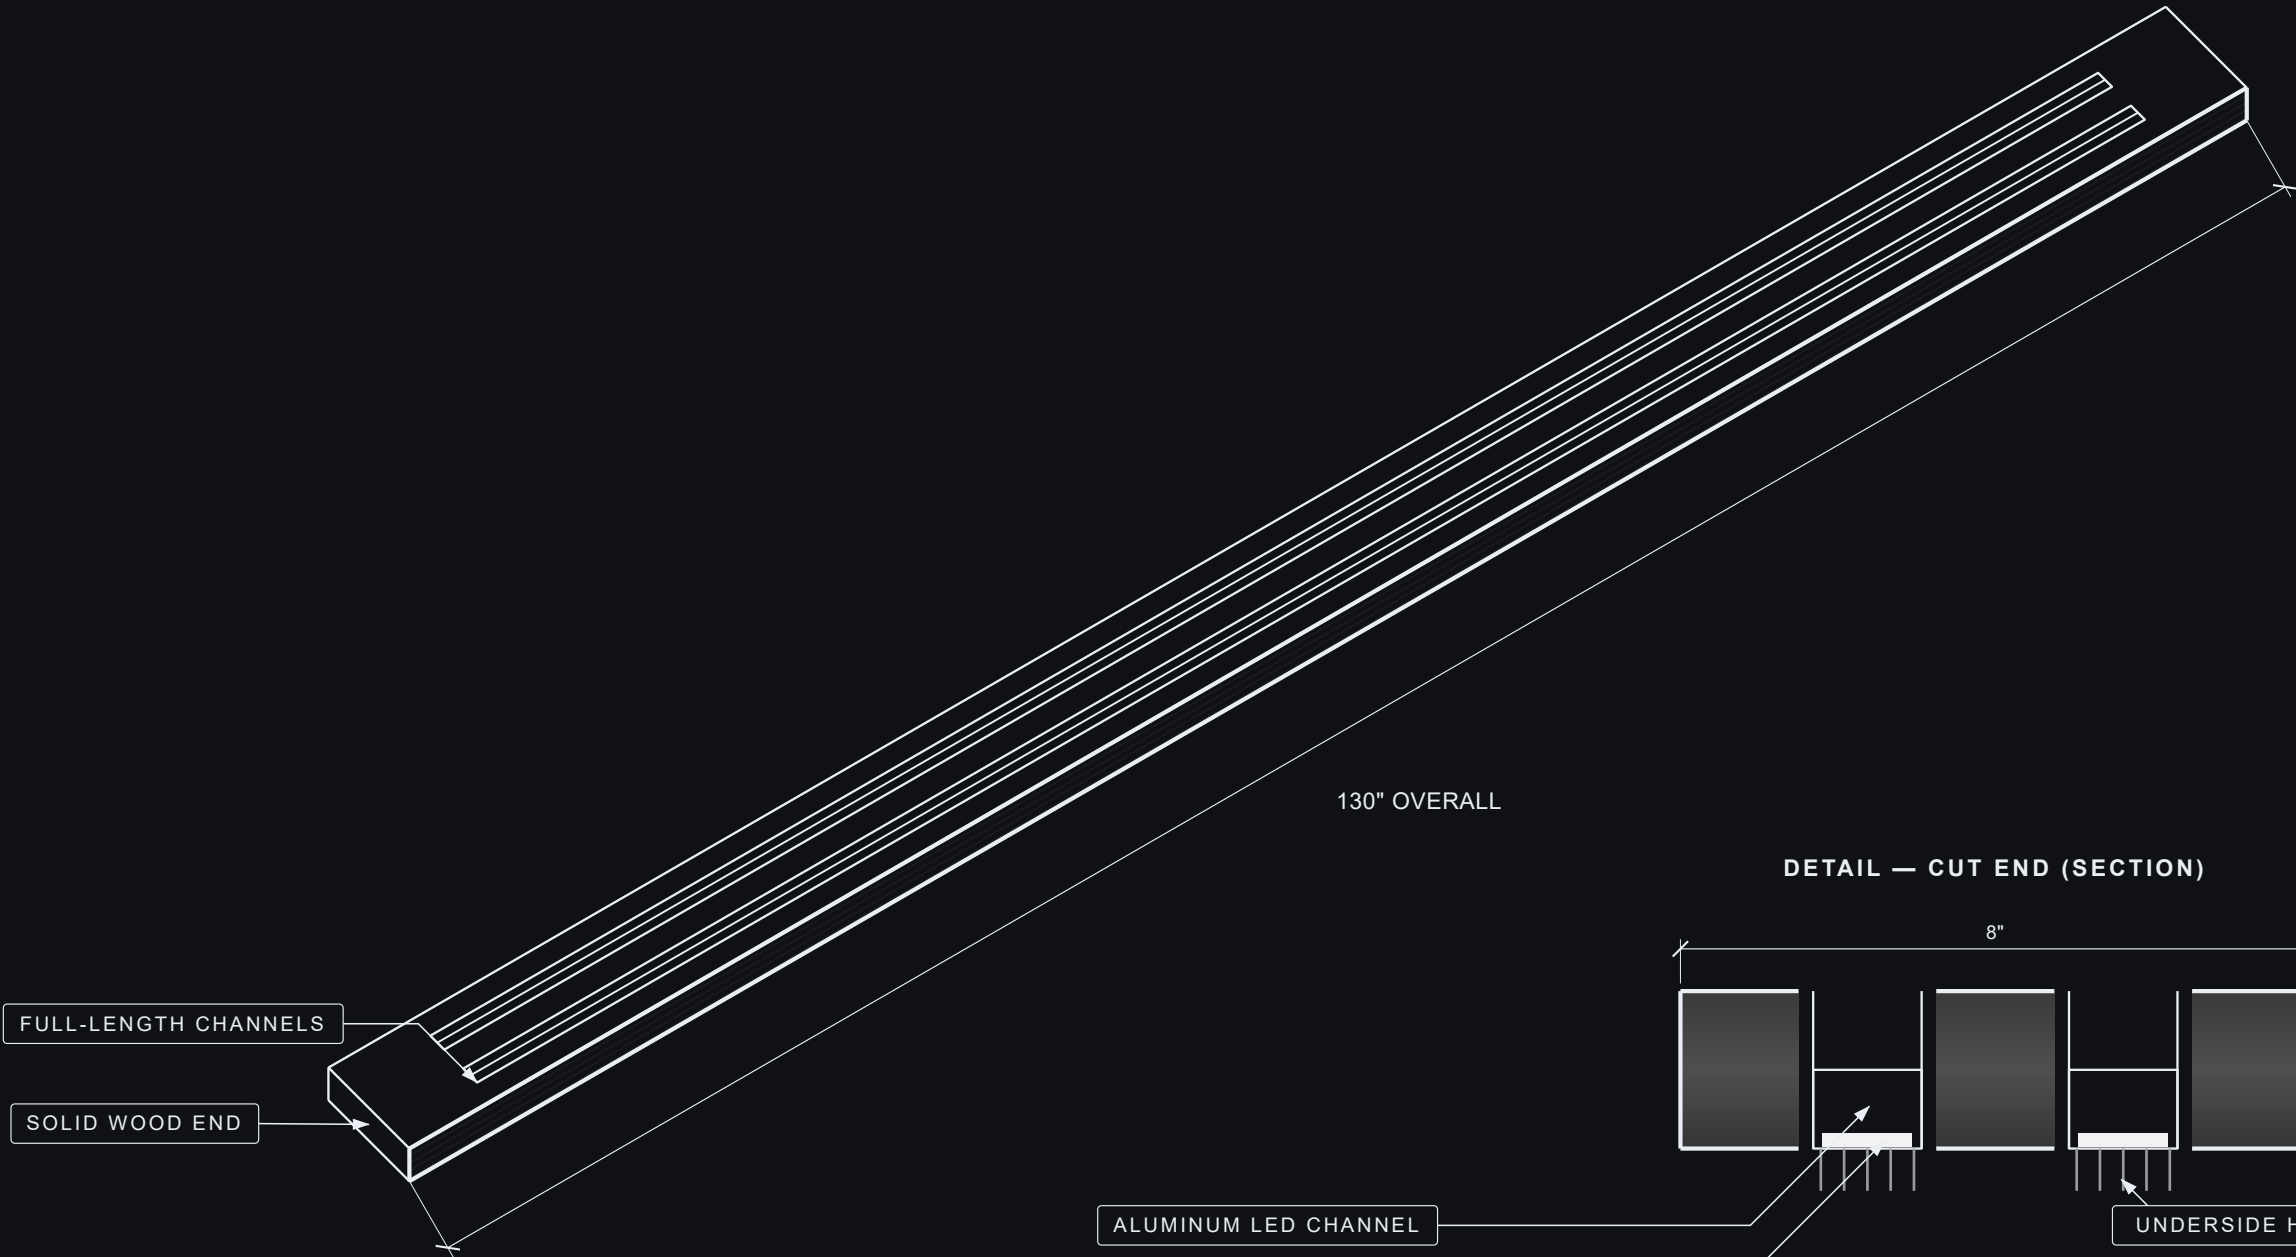

DETAIL — CUT END (SECTION)

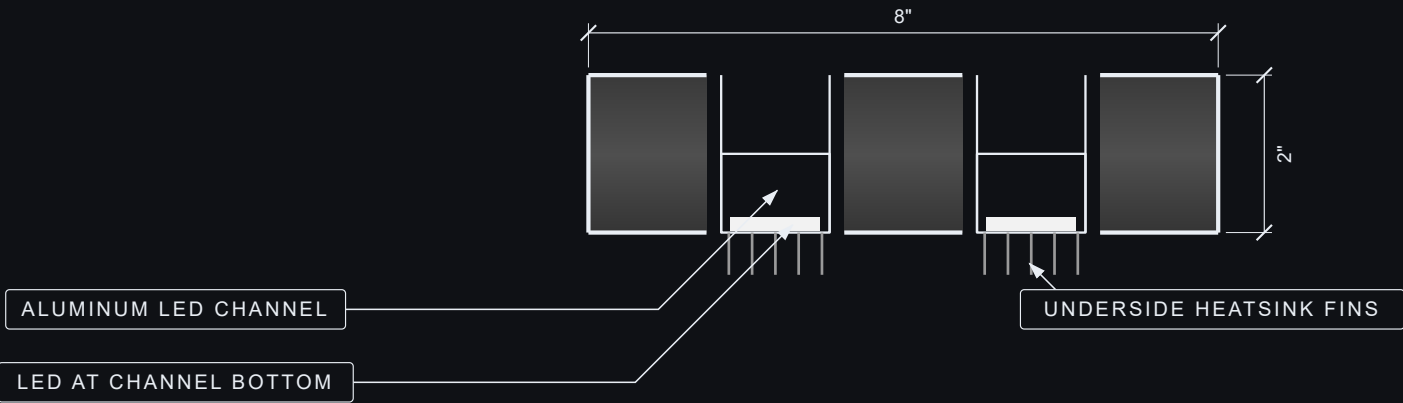

PROJECT	HEIRLOOM BED	SHEET 2 OF 2
DRAWING NO.	TopCap-LED_Blueprint	
LAST UPDATE	2026-06-19 12:30 PM	REV 1.21