

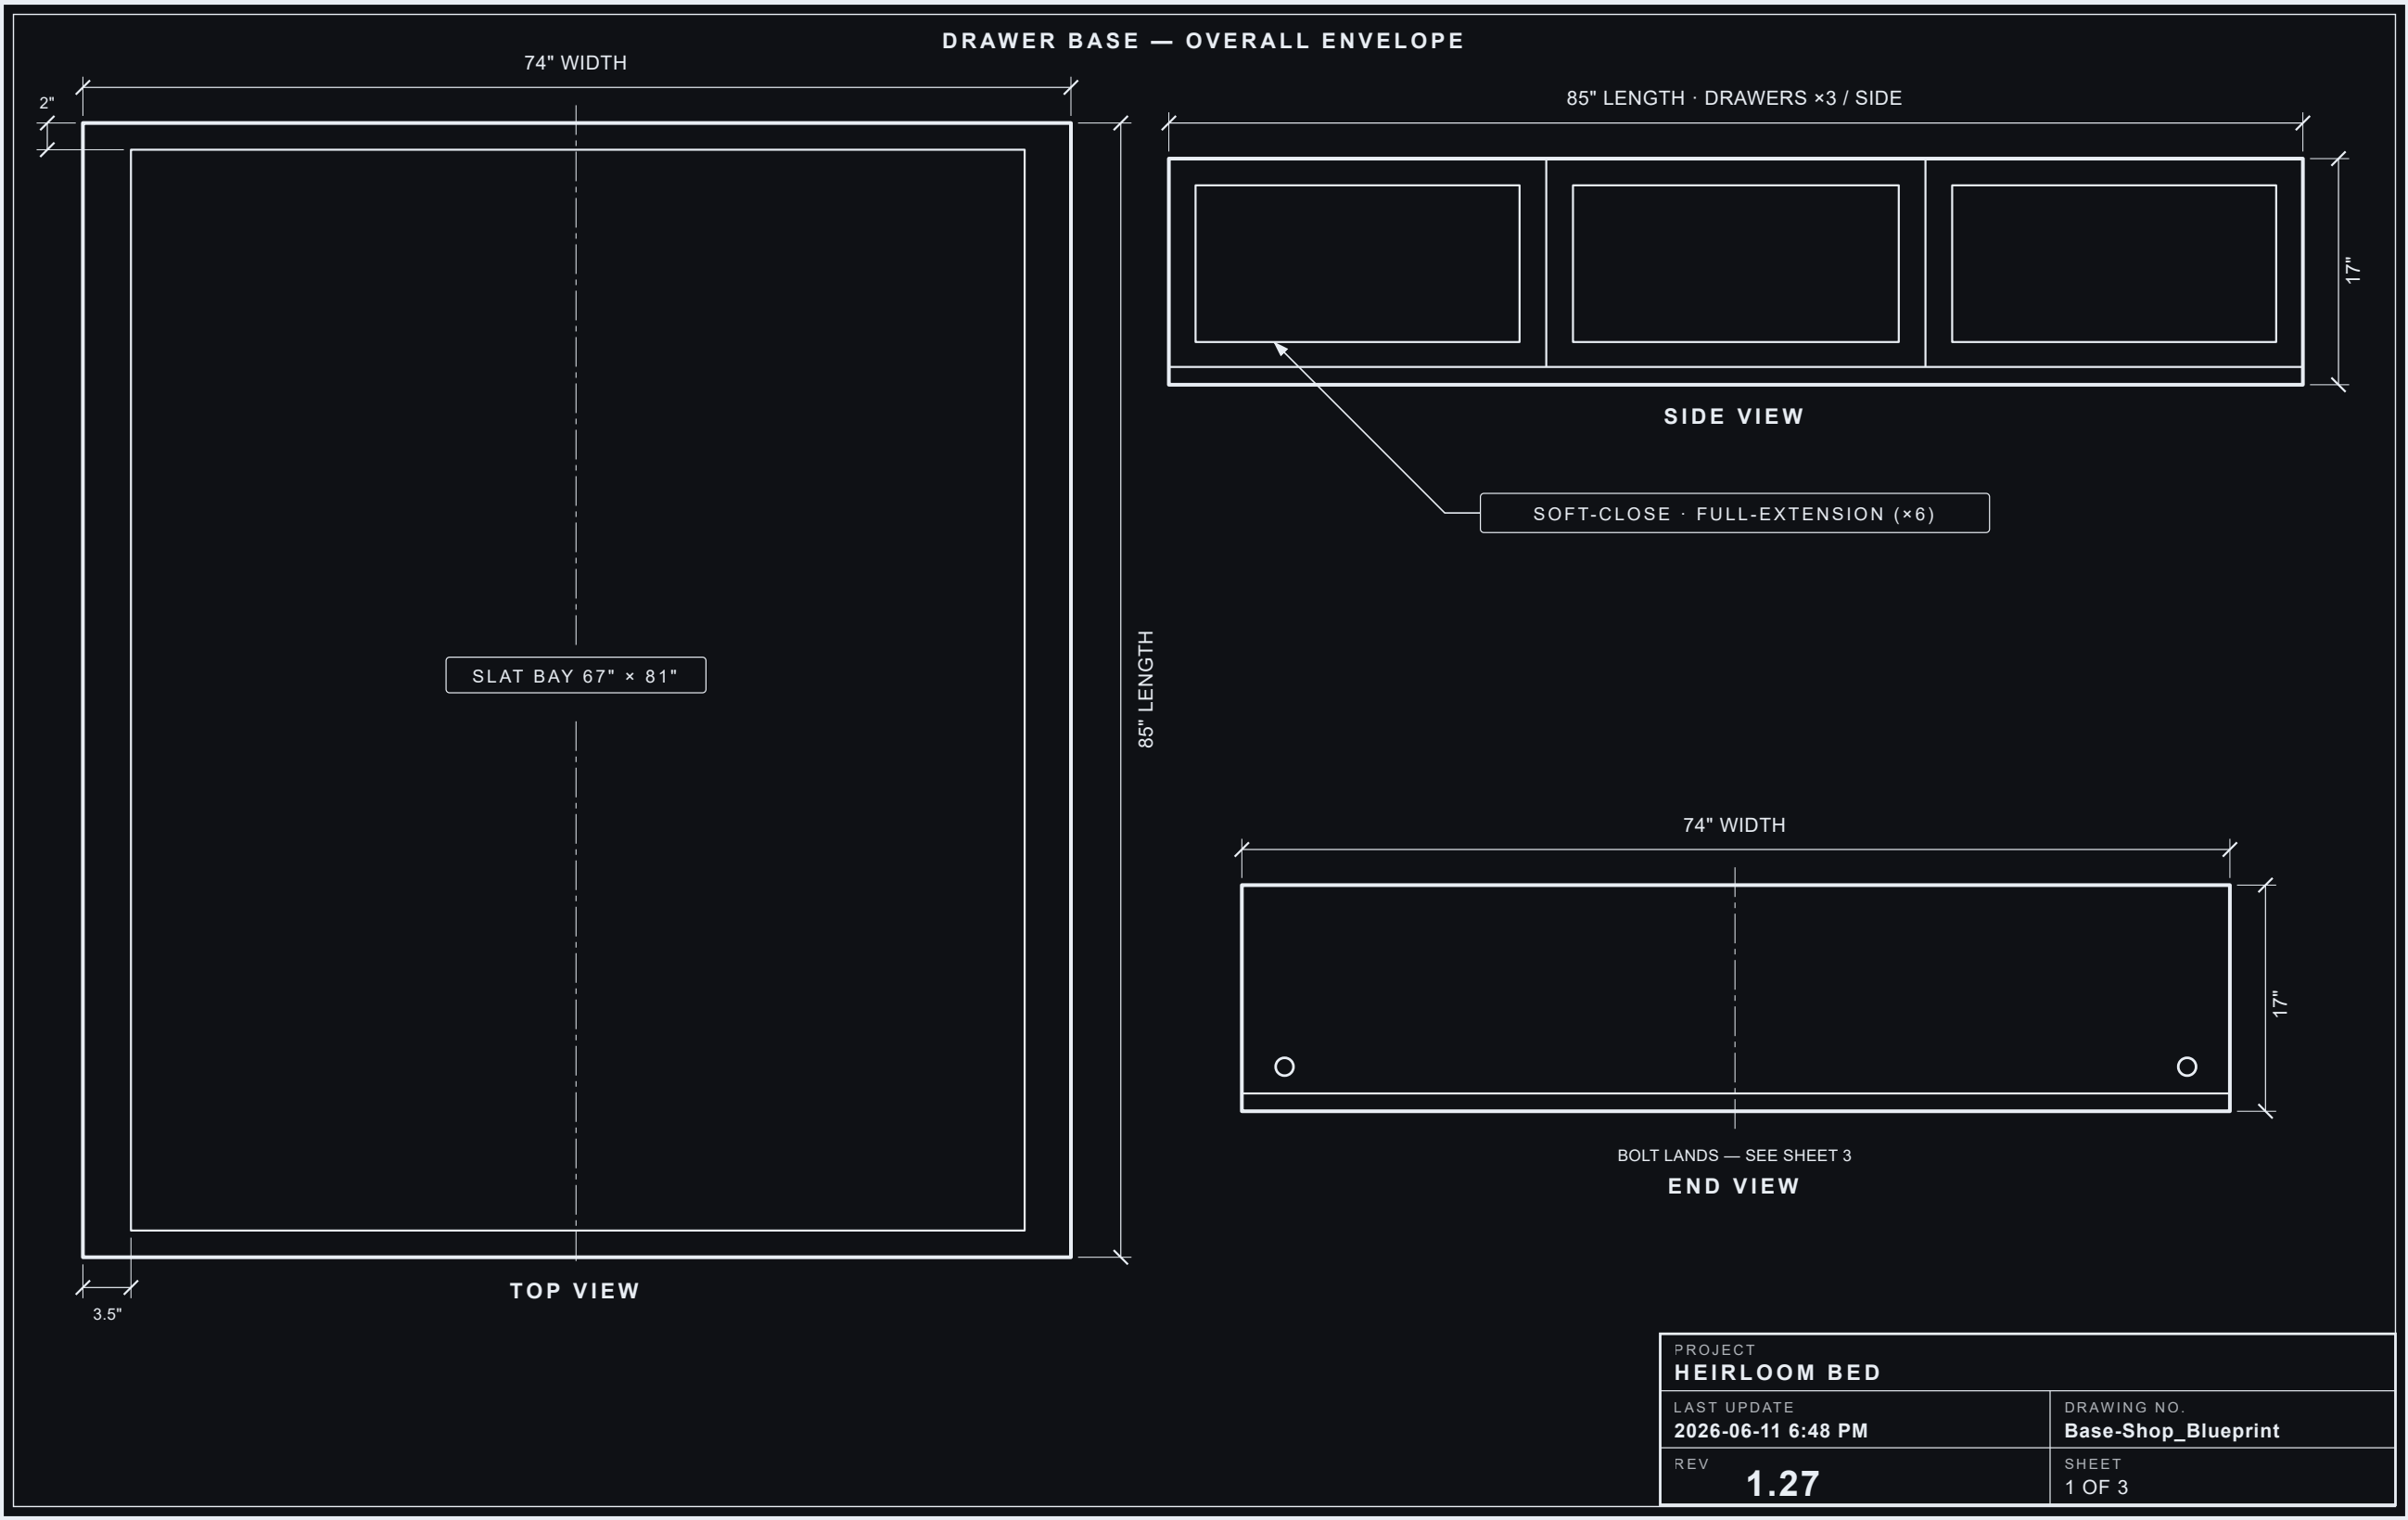


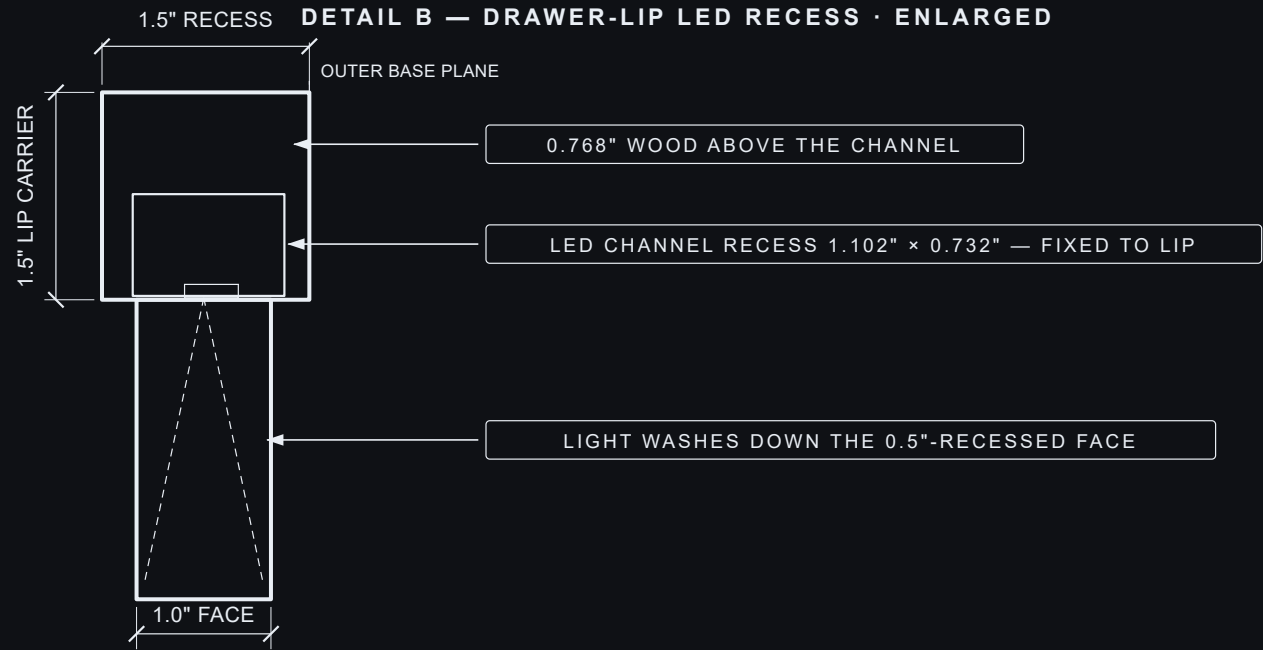


SECTION DETAILS

SECTION A-A · TRANSVERSE (ACROSS THE WIDTH)

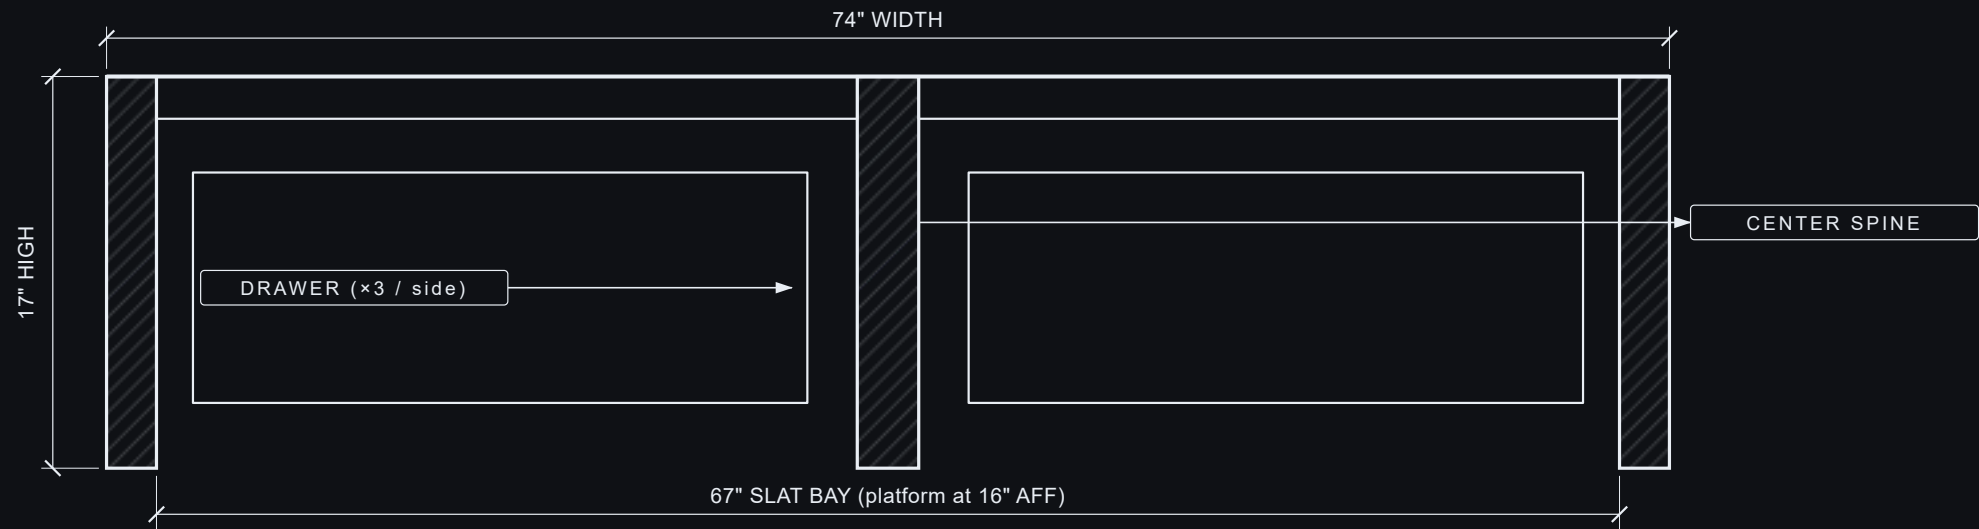

PROJECT HEIRLOOM BED	
LAST UPDATE 2026-06-11 6:48 PM	DRAWING NO. Base-Shop_Blueprint
REV 1.27	SHEET 2 OF 3

CRITICAL INTERFACES — BASE BOLT LANDS

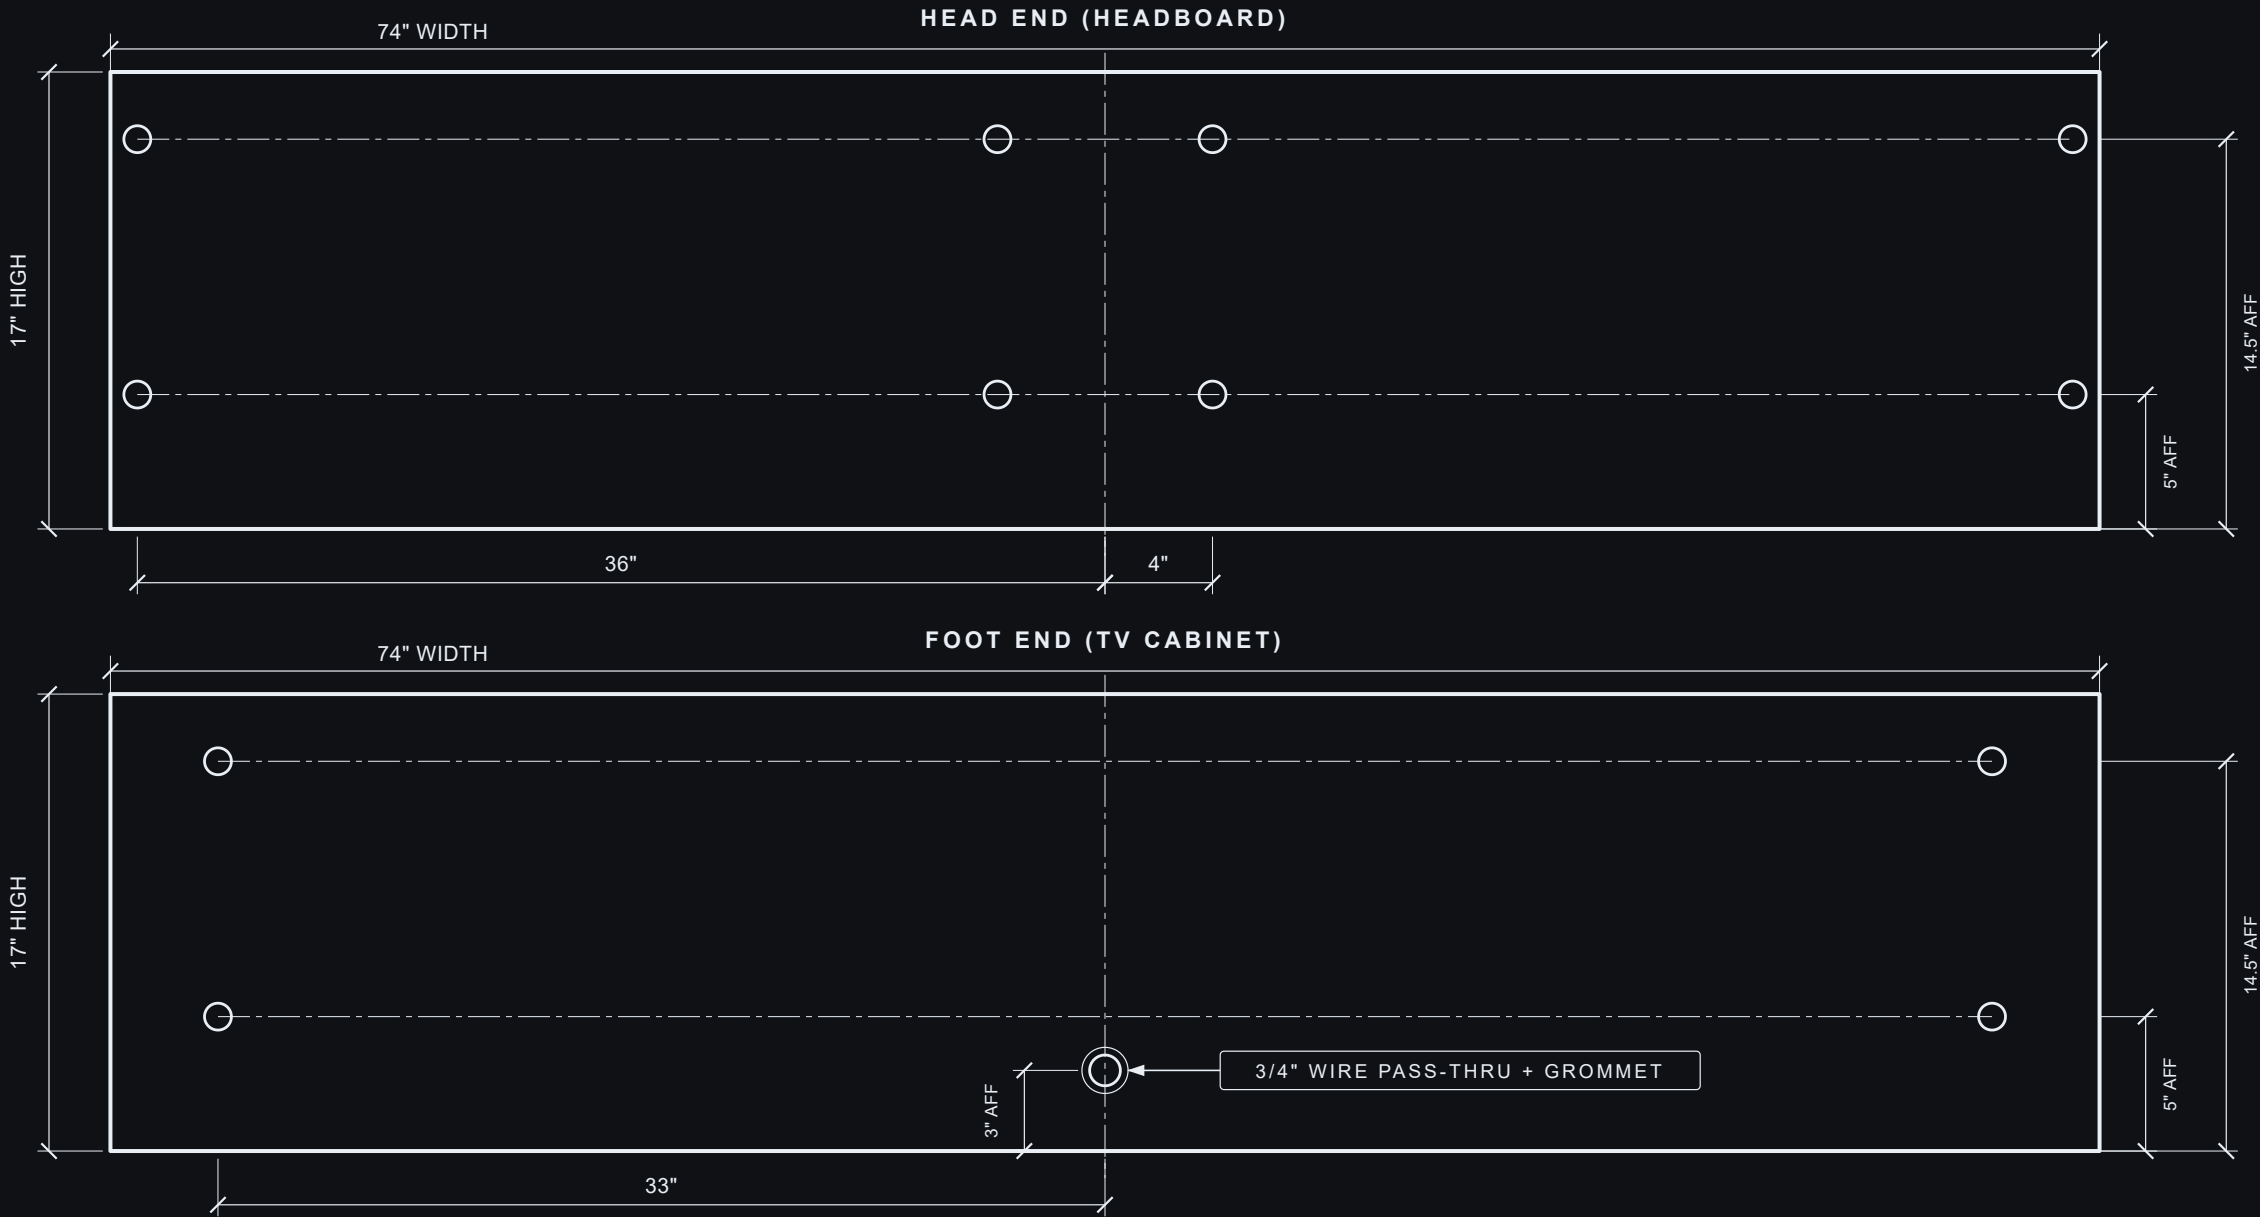

PROJECT HEIRLOOM BED	
LAST UPDATE 2026-06-11 6:48 PM	DRAWING NO. Base-Shop_Blueprint
REV 1.27	SHEET 3 OF 3