




GRAPHIC SCALE (FEET)

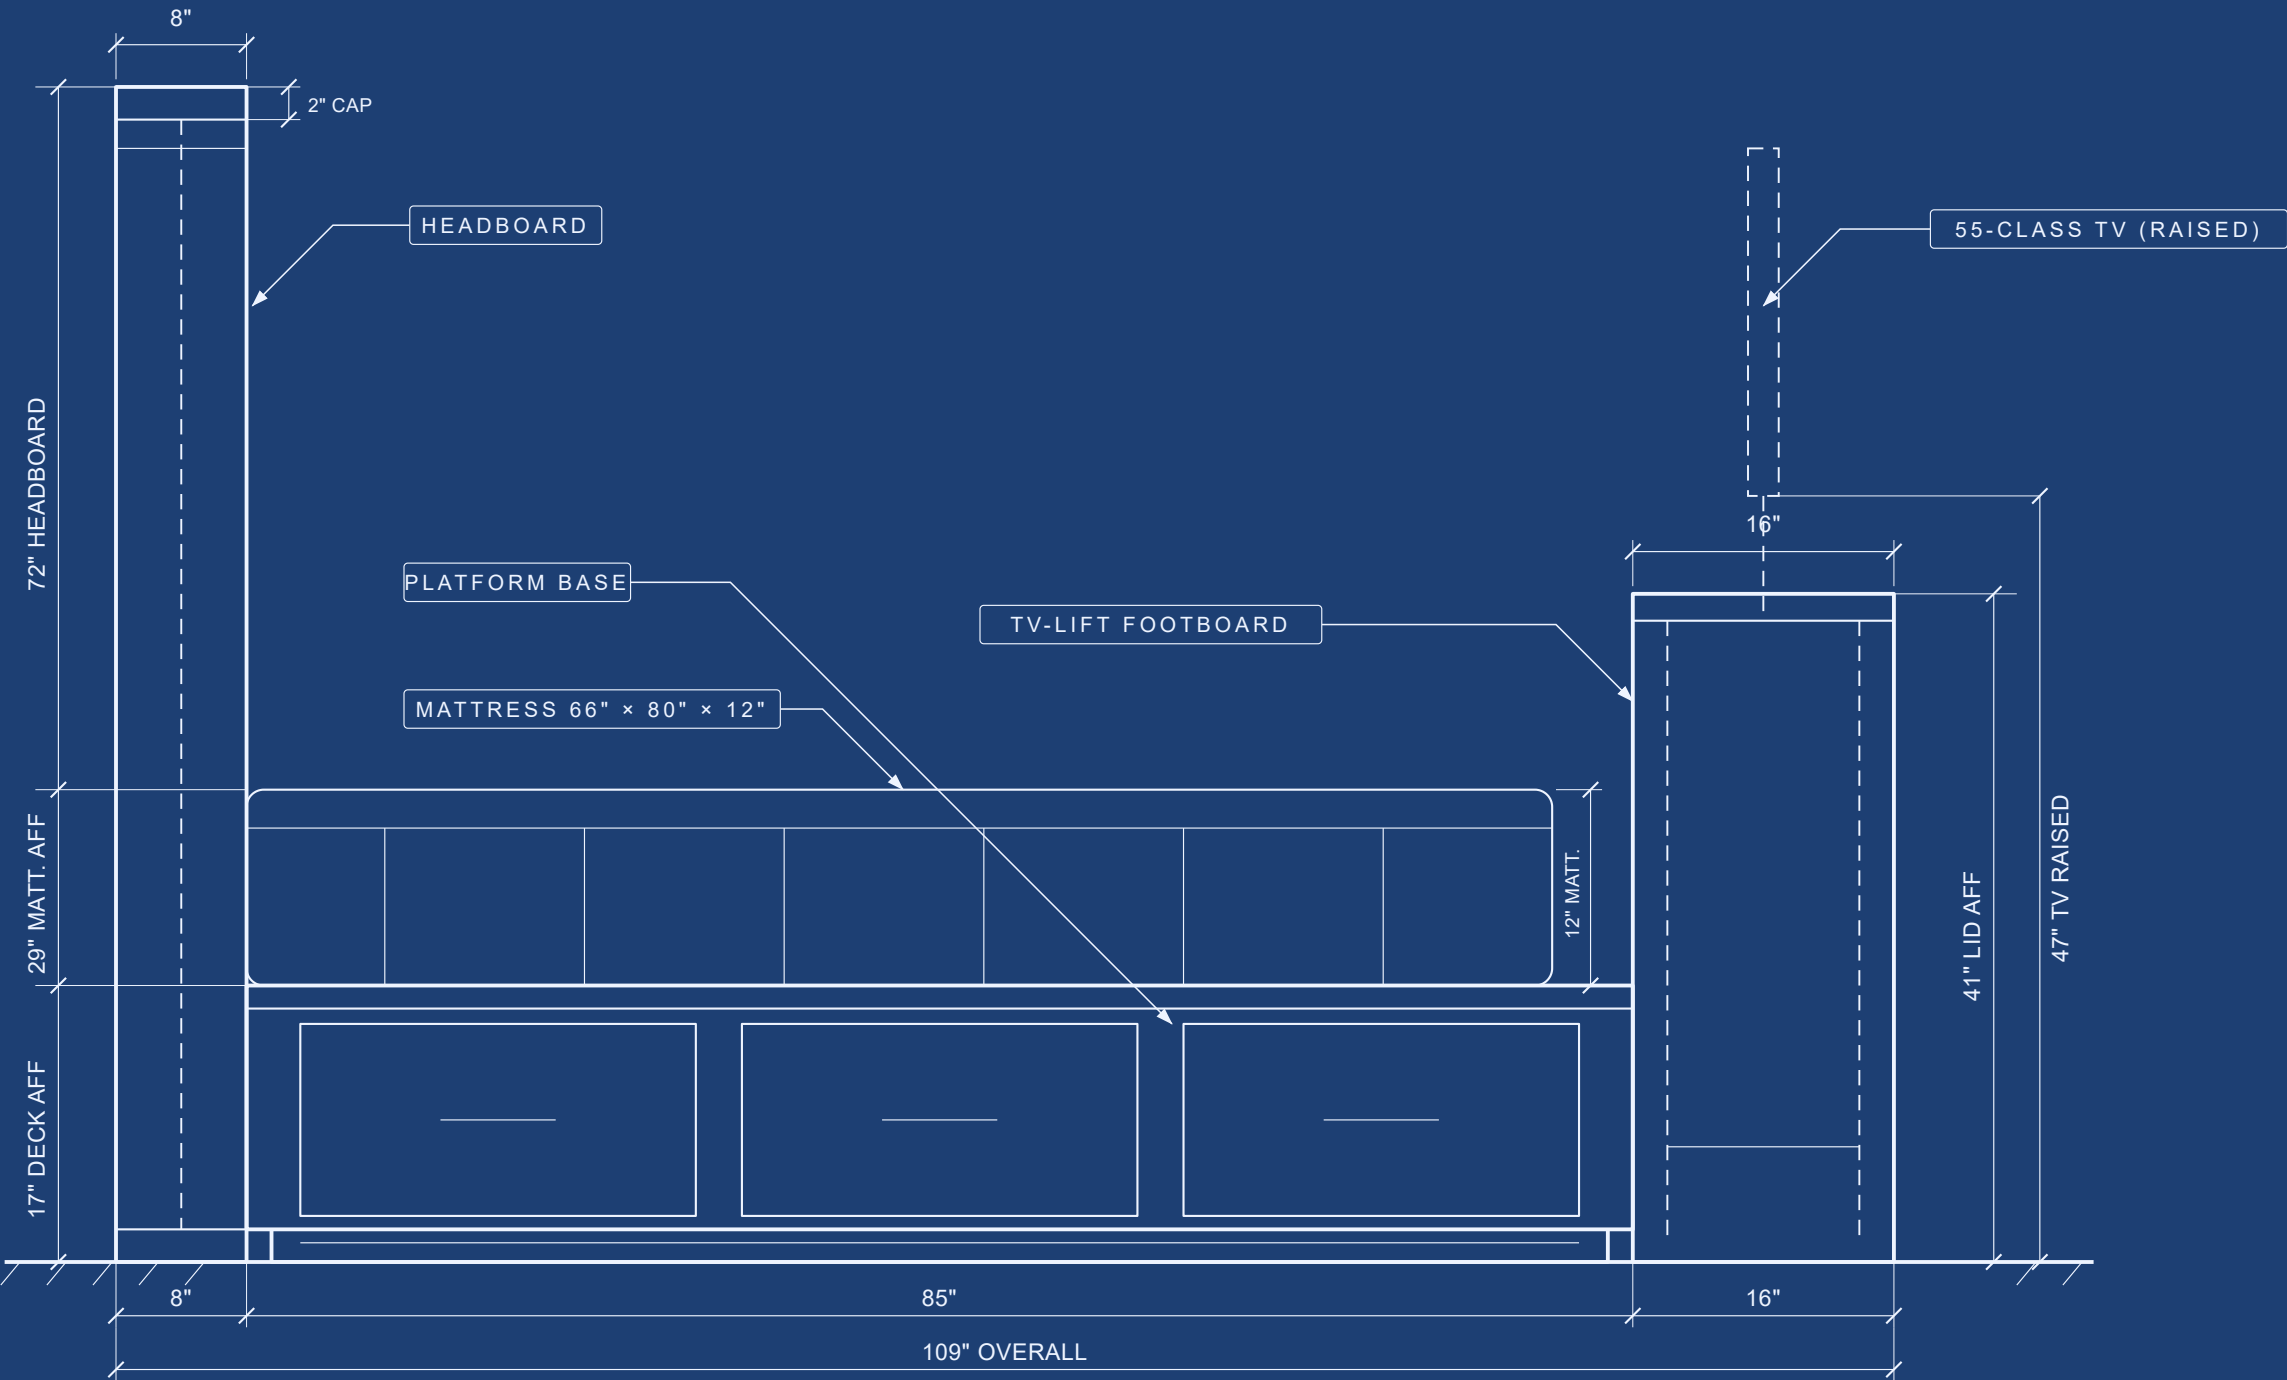

SIDE ELEVATION

GENERAL NOTES

1. All dimensions in inches ("). AFF = above finished floor.
2. Figured dimensions govern — DO NOT scale from the print.

PROJECT
HEIRLOOM BED

DRAWING
Side Elevation

REV
1.0

DRAWING NO.
Bed-Side_Blueprint

SHEET
1 OF 1