

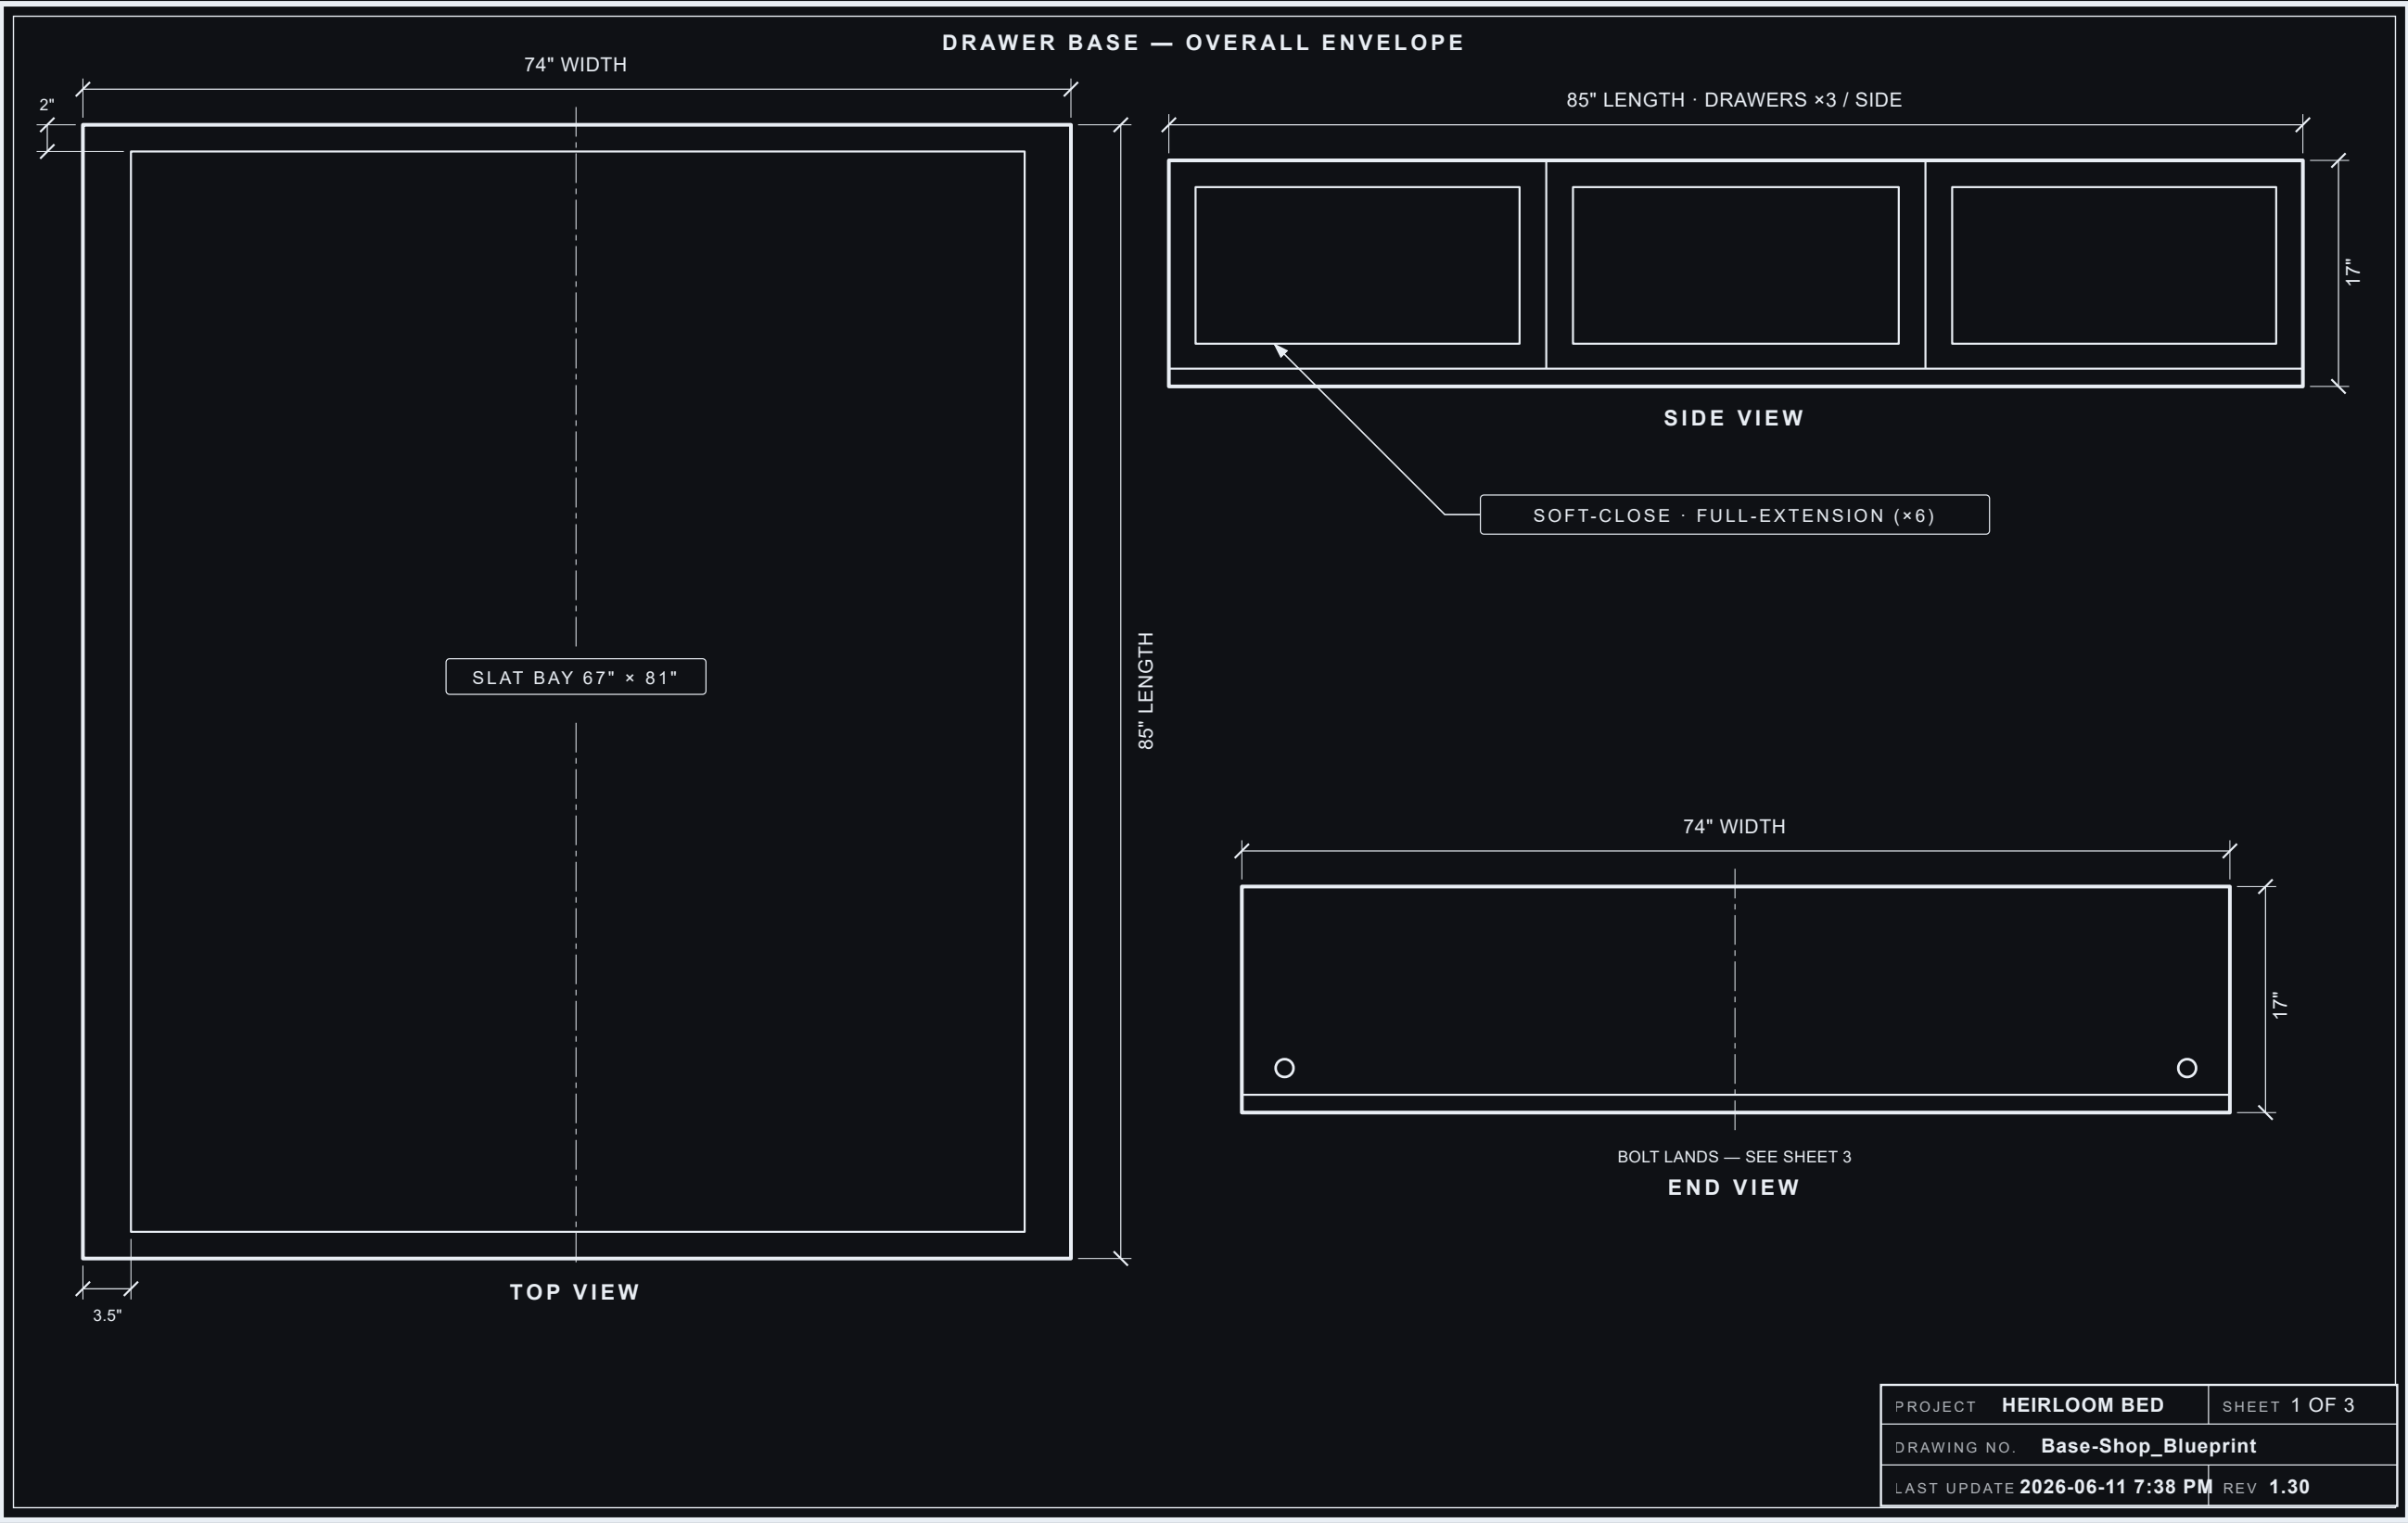


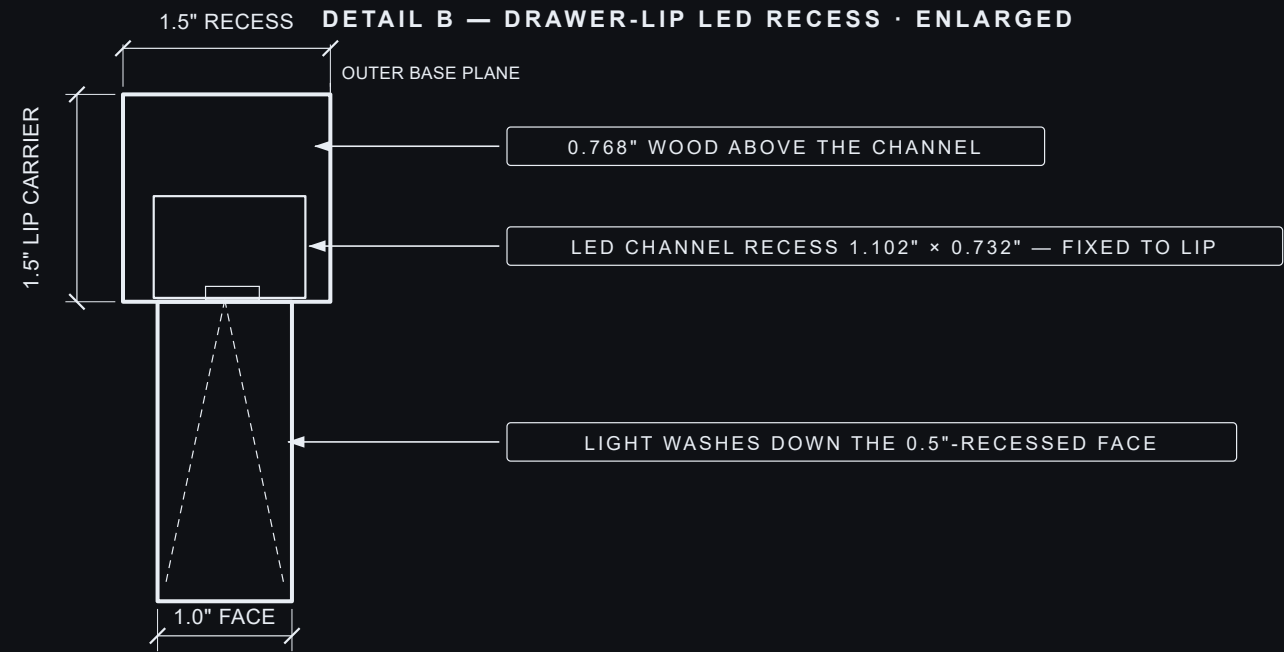


SECTION DETAILS

SECTION A-A · TRANSVERSE (ACROSS THE WIDTH)

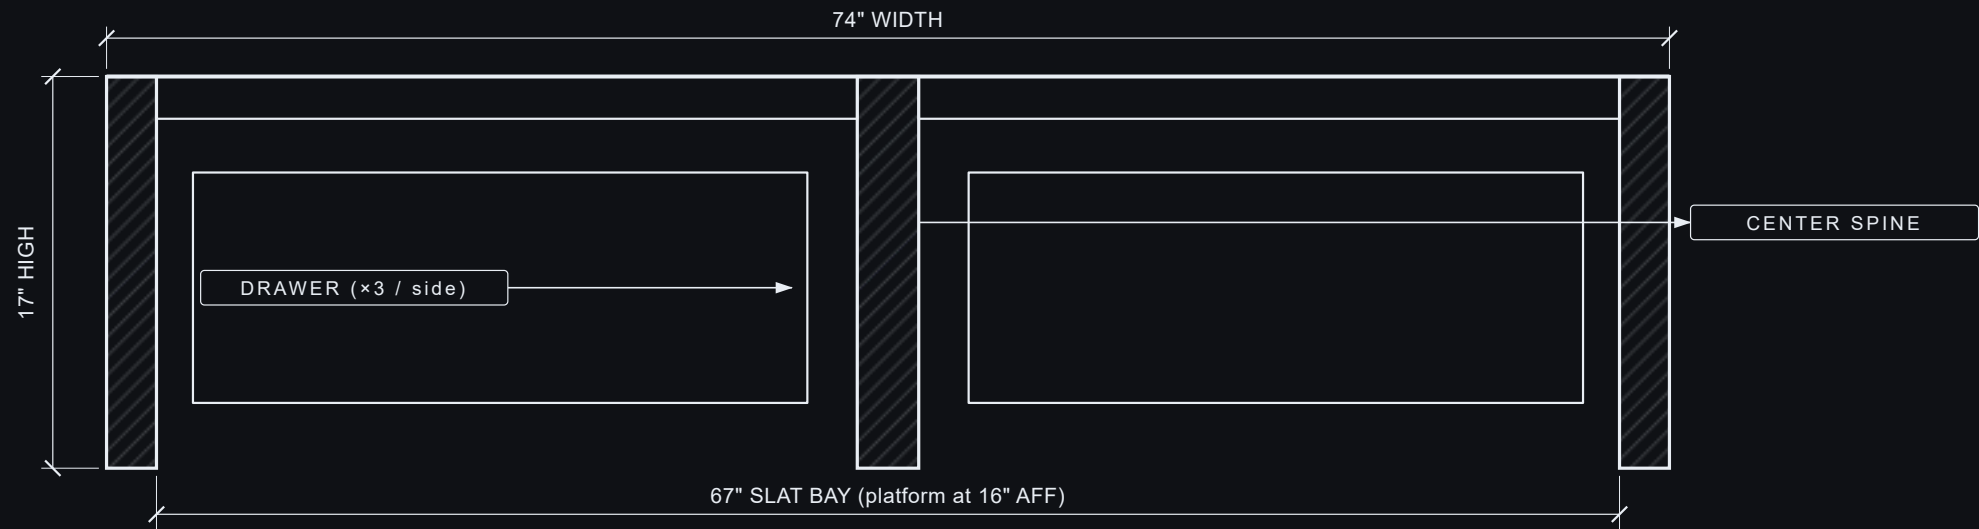

PROJECT	HEIRLOOM BED	SHEET 2 OF 3
DRAWING NO.	Base-Shop_Blueprint	
LAST UPDATE	2026-06-11 7:38 PM	REV 1.30

CRITICAL INTERFACES — BASE BOLT LANDS

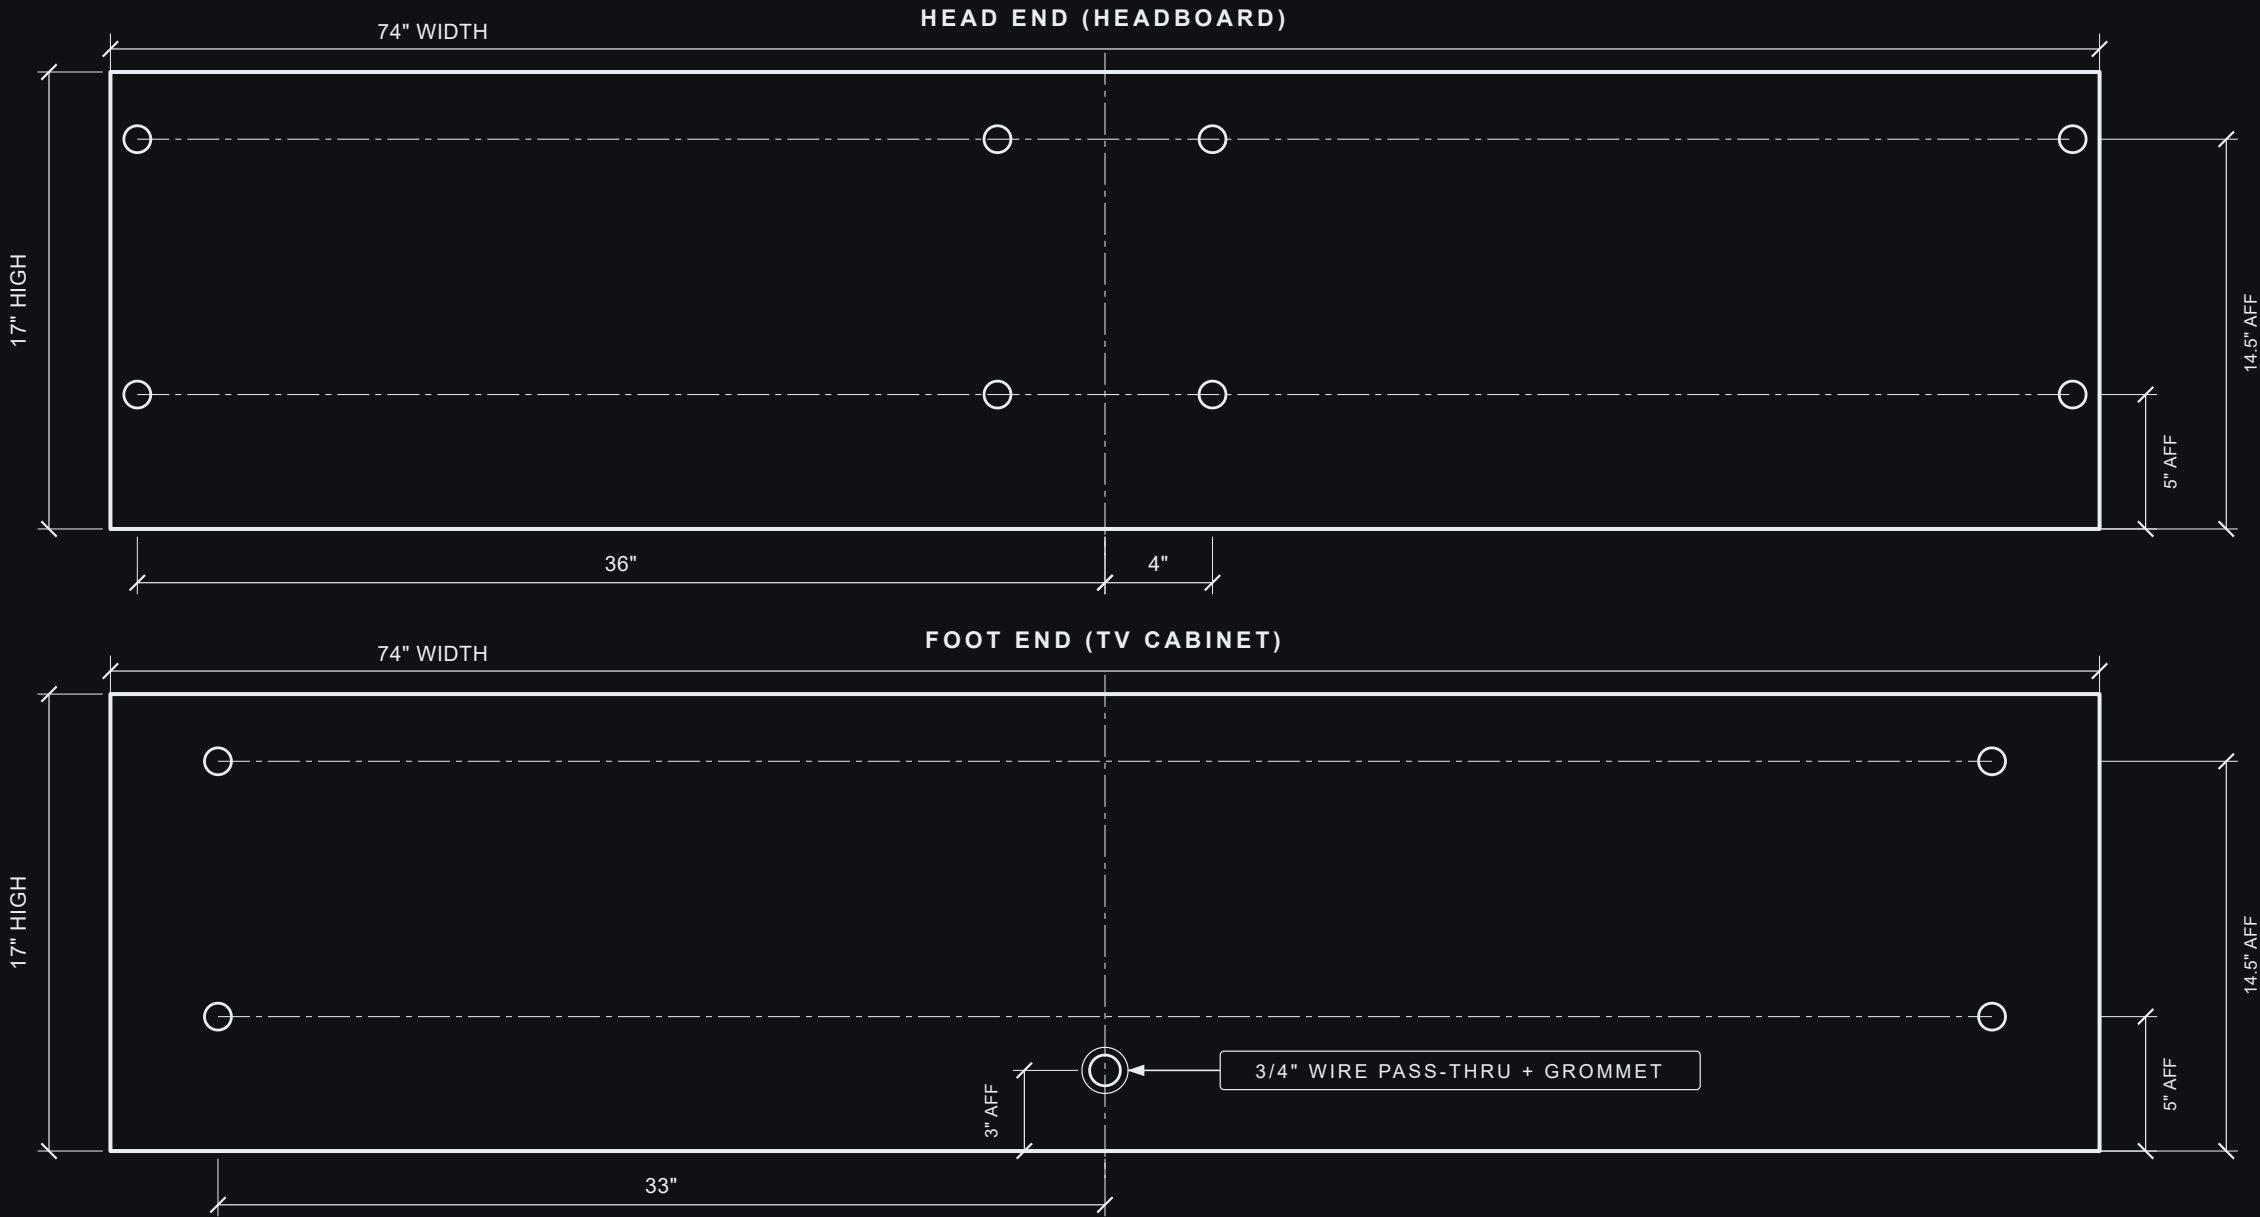

PROJECT	HEIRLOOM BED	SHEET	3 OF 3
DRAWING NO.	Base-Shop_Blueprint		
LAST UPDATE	2026-06-11 7:38 PM	REV	1.30