


FRONT VIEW — WHOLE BED · TV CABINET REMOVED

130" HEADBOARD (OVERALL)

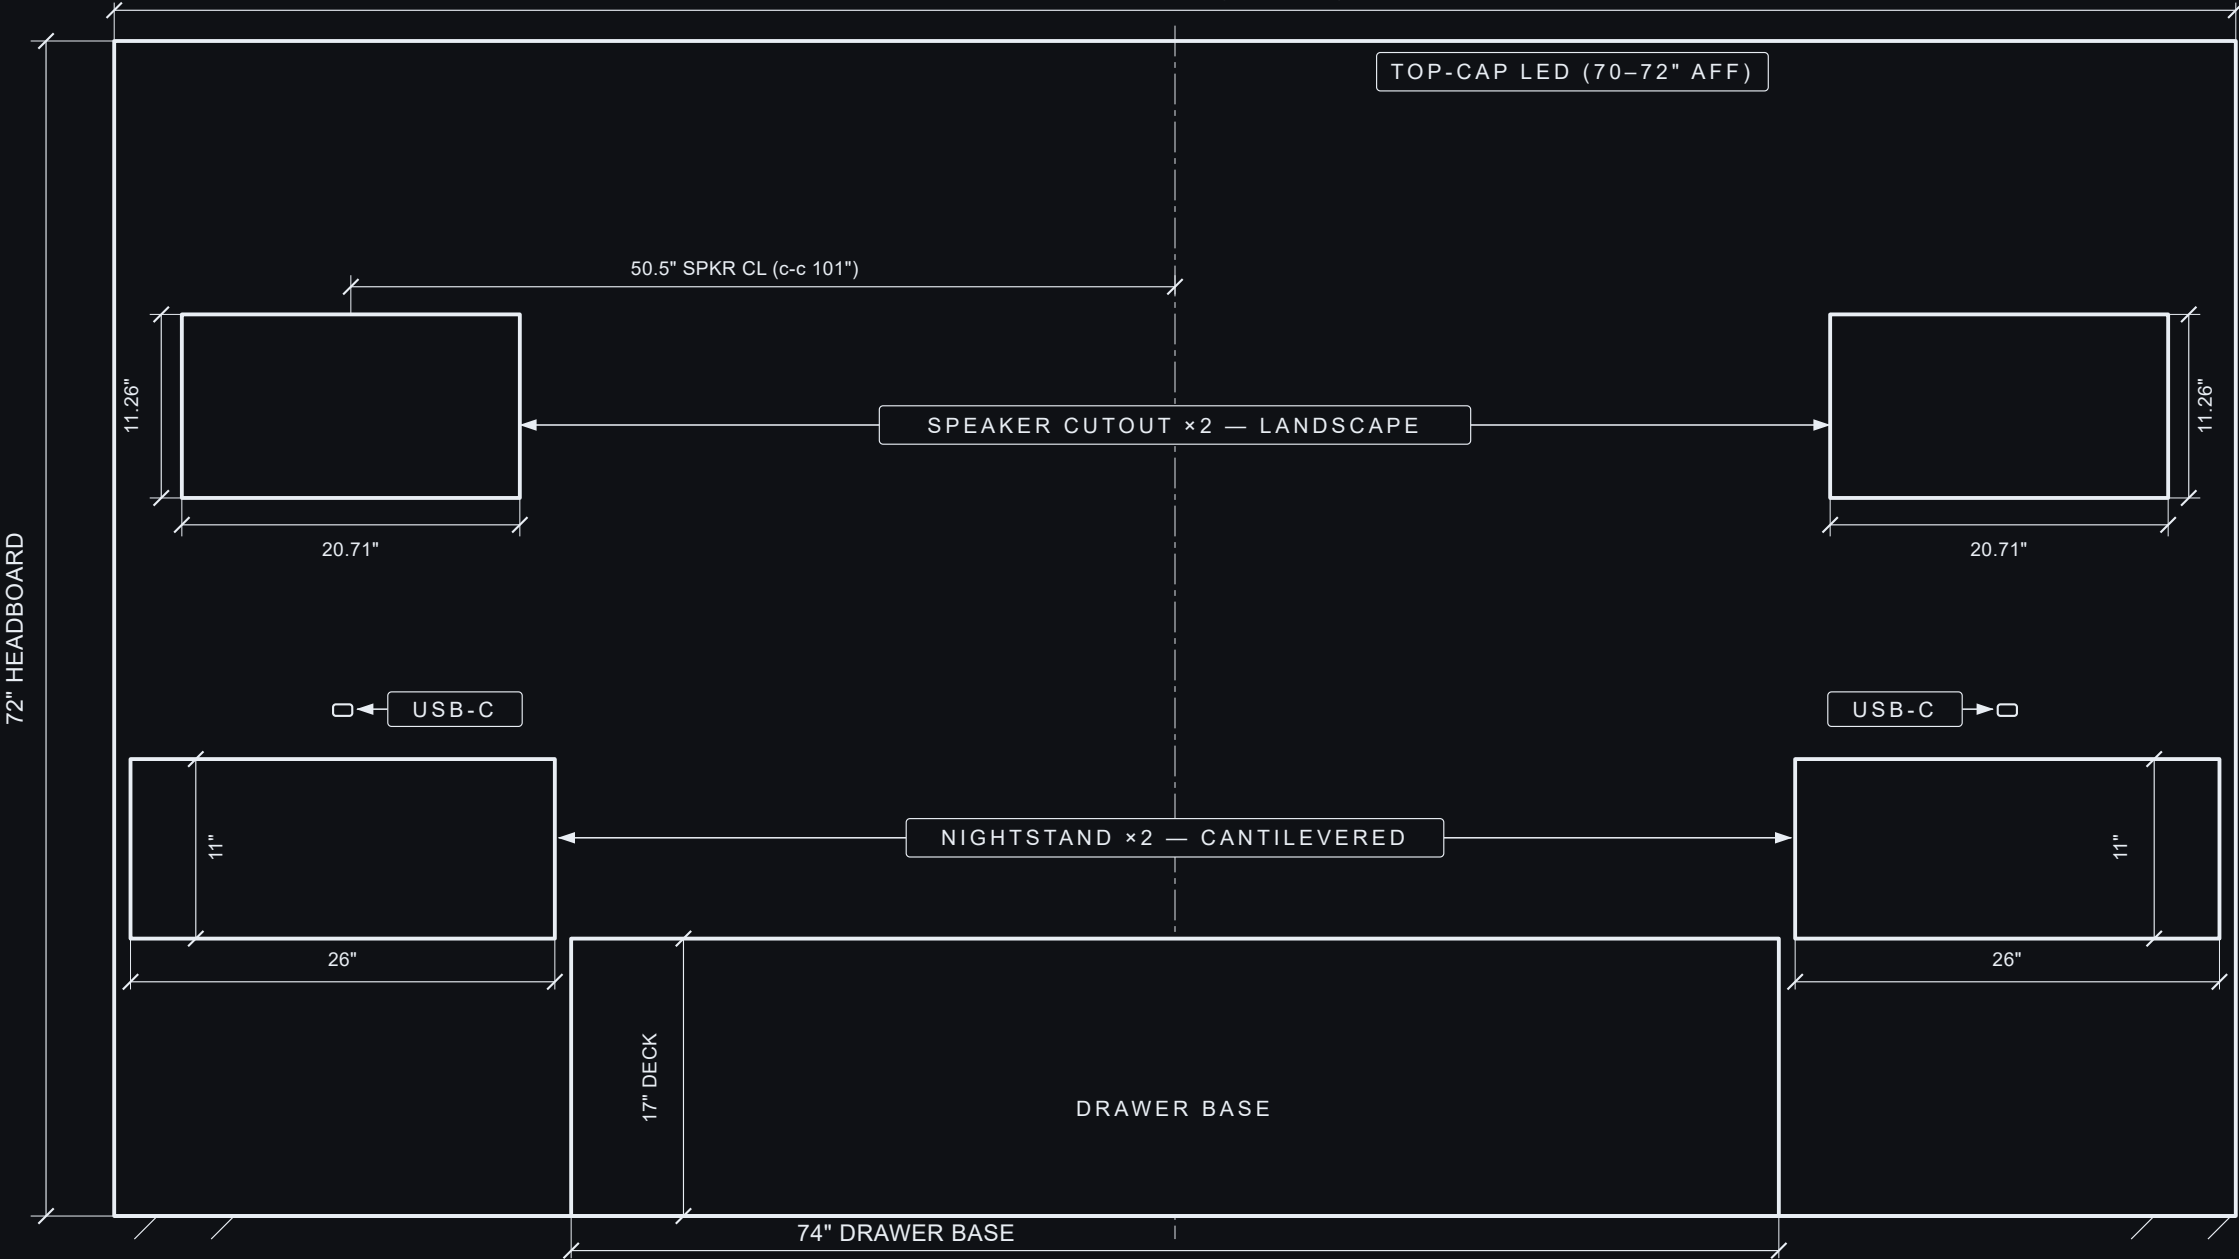

TV CABINET (FOOTBOARD) REMOVED — SEE TV-Cabinet_Blueprint

PROJECT	HEIRLOOM BED	SHEET 1 OF 1
DRAWING NO.	Bed-Front_Blueprint	
LAST UPDATE	2026-06-11 7:38 PM	REV 4.3