


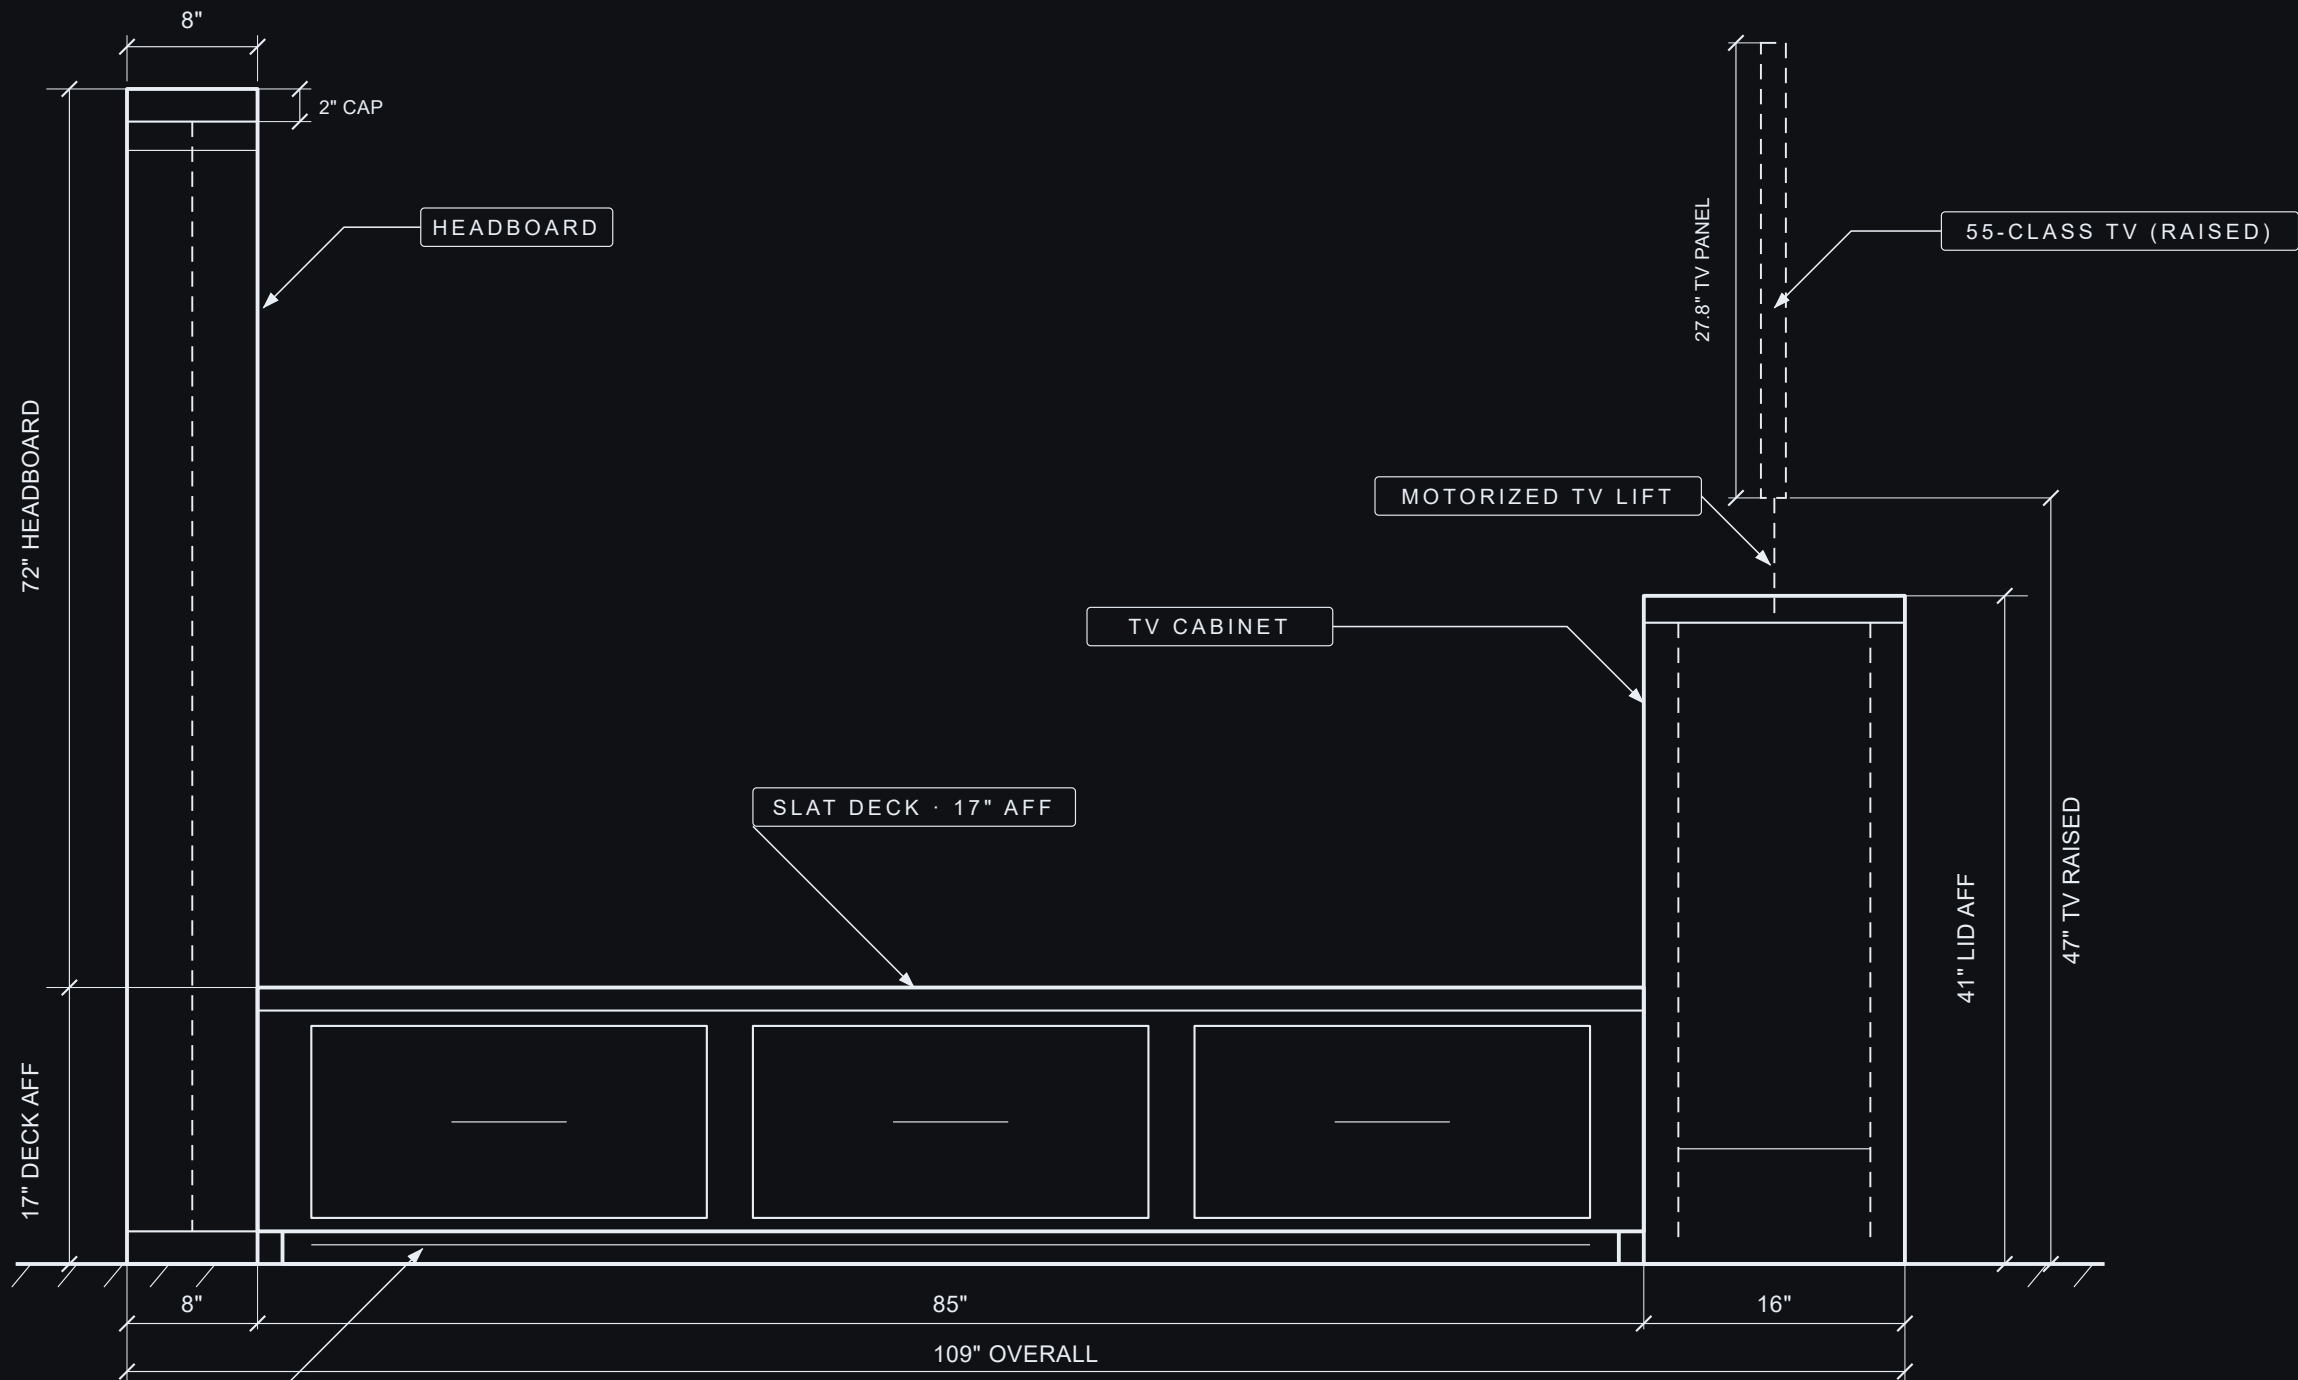

SIDE VIEW

PROJECT	HEIRLOOM BED	SHEET 1 OF 1
DRAWING NO.	Bed-Side_Blueprint	
LAST UPDATE	2026-06-11 7:38 PM	REV 1.18