


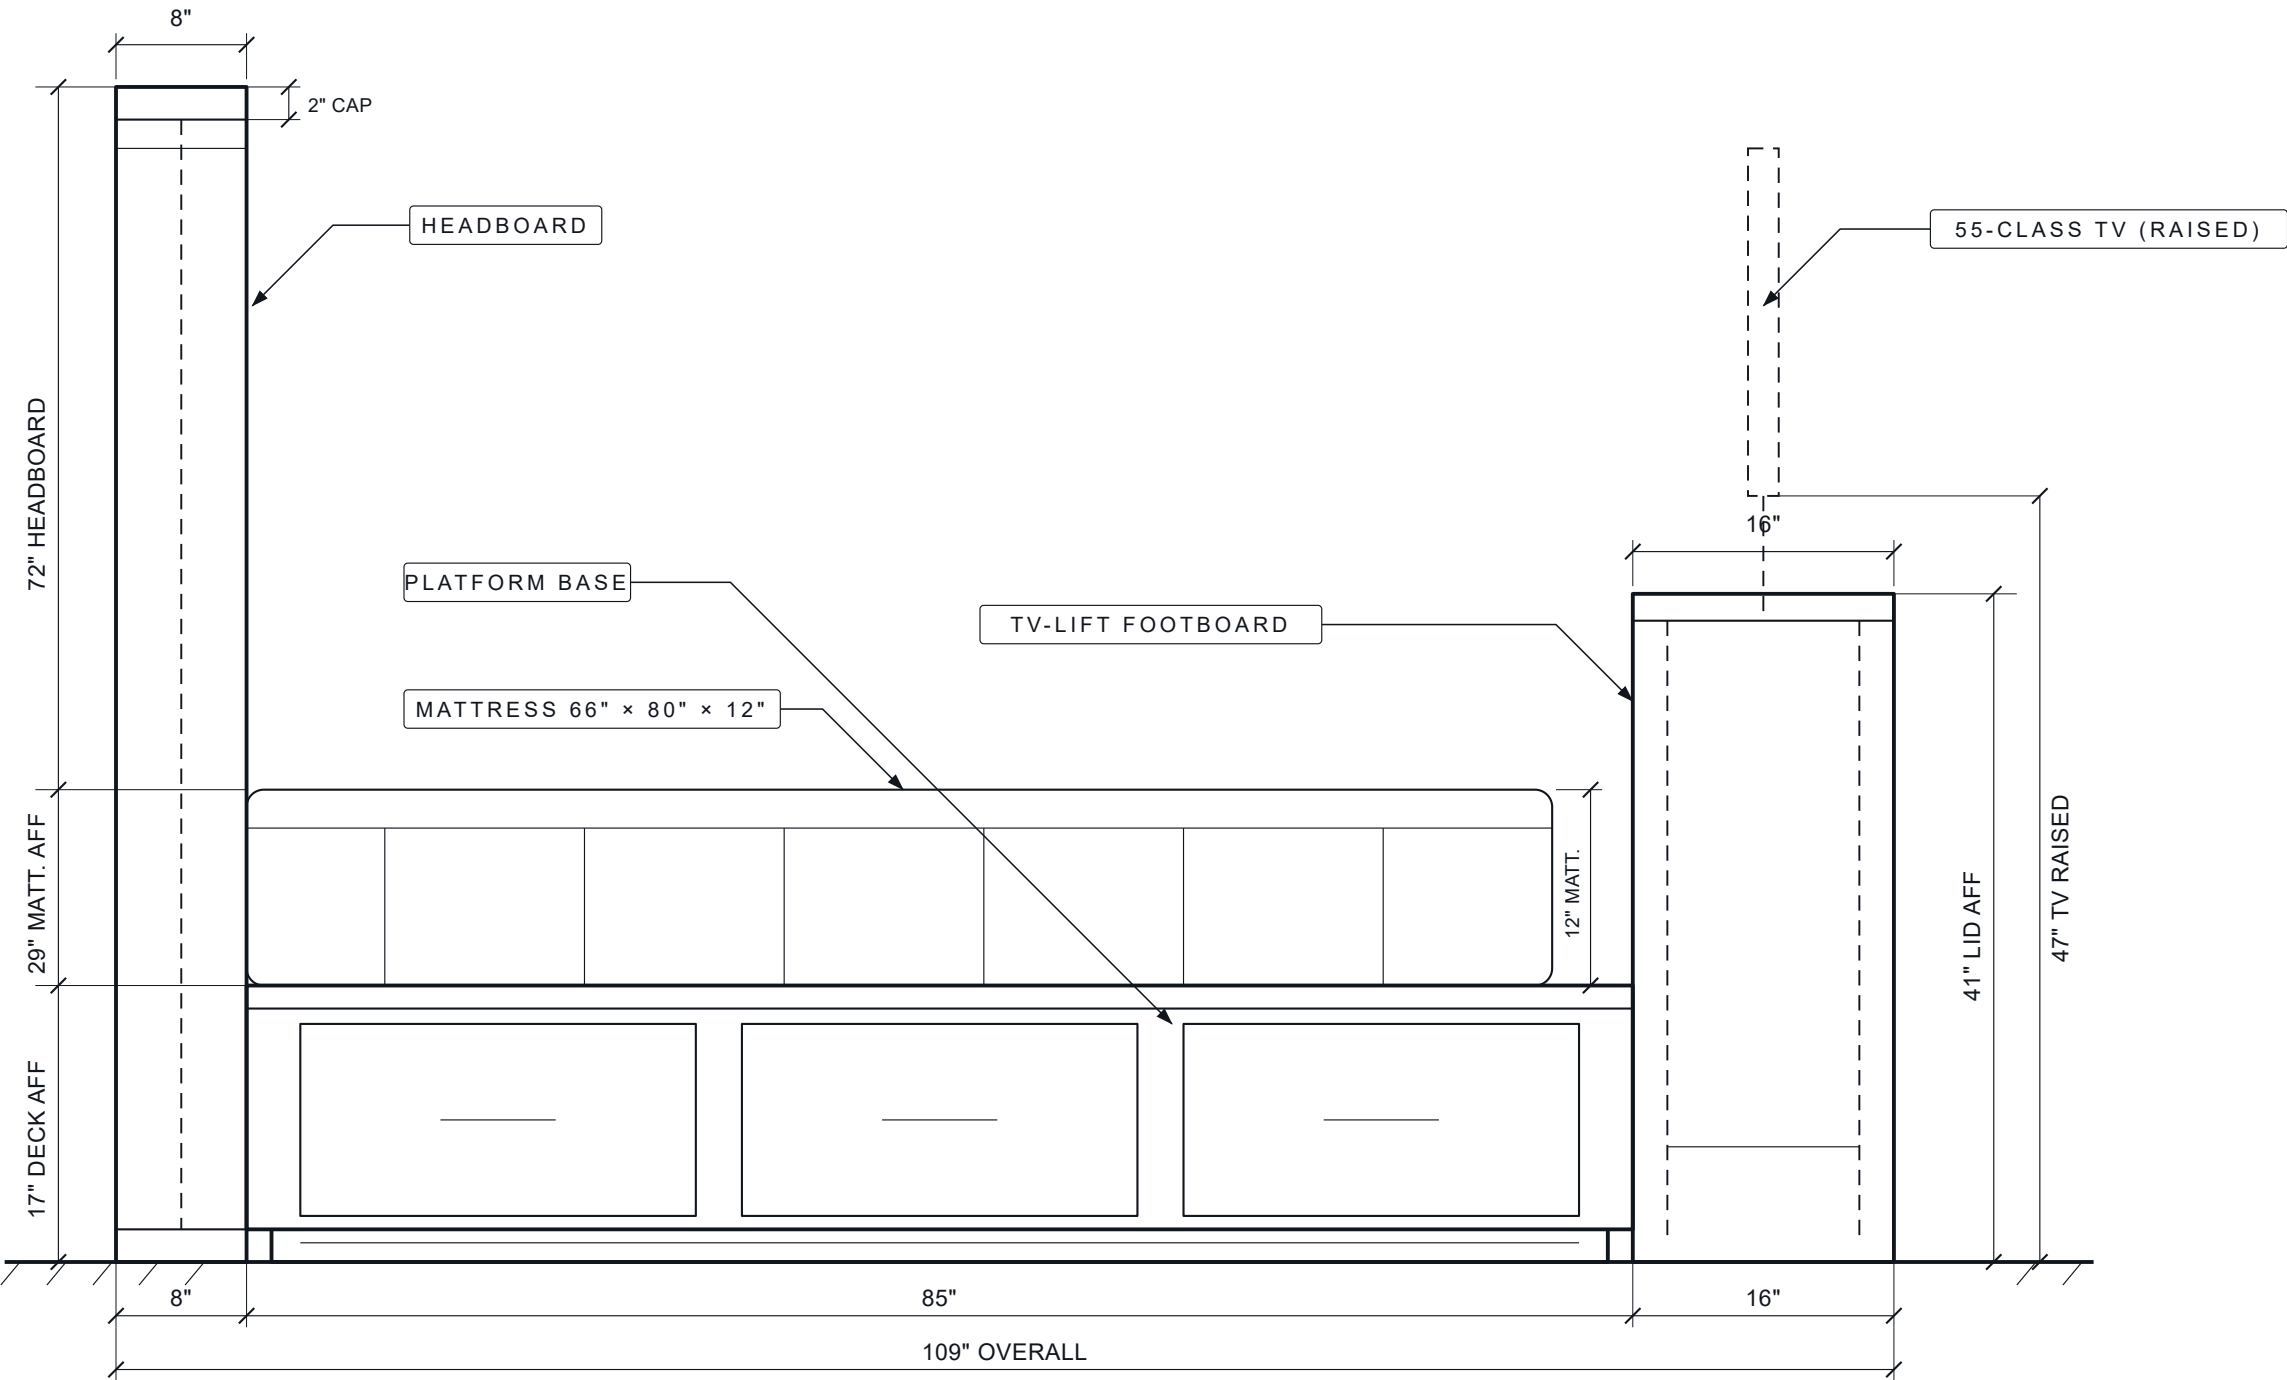

SIDE VIEW

- GENERAL NOTES**
1. All dimensions in inches ("). AFF = above finished floor.
 2. Figured dimensions govern — DO NOT scale from the print.

PROJECT HEIRLOOM BED	
DRAWING Side view	DRAWING NO. Bed-Side_Blueprint
REV 1.3	SHEET 1 OF 1