


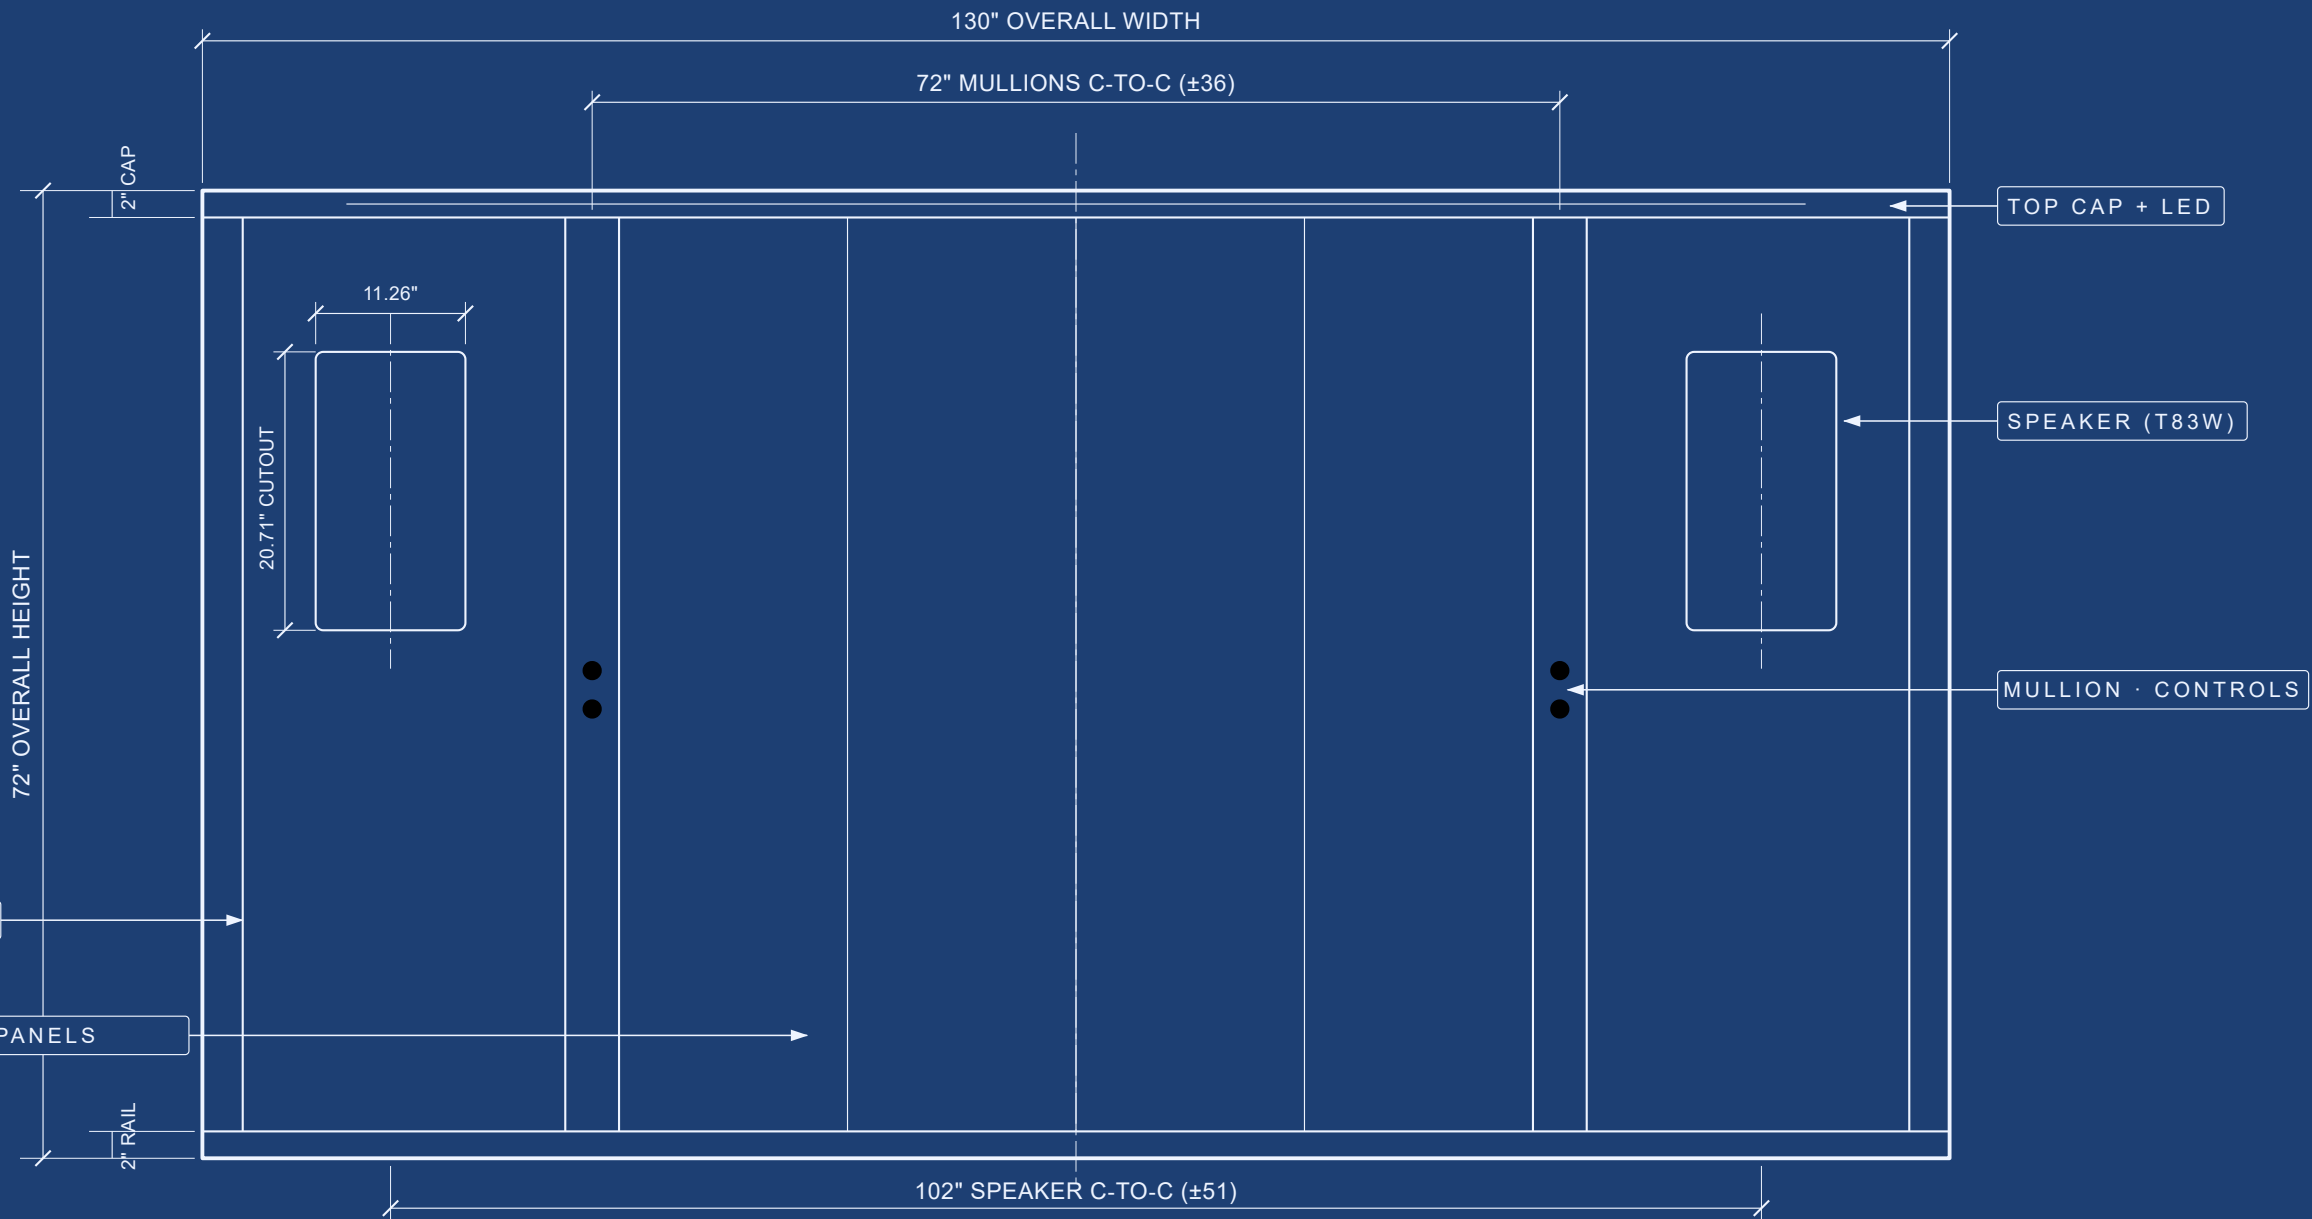

HEADBOARD — FRONT ELEVATION



- GENERAL NOTES**
- 1. All dimensions in inches ("). AFF = above finished floor.
 - 2. Six 1" front panels in a rail-and-stile frame; LED channel in the top cap (see TopCap-LED).
 - 3. Speaker cutouts straight/flush (no toe-in). Do not scale — figured dimensions govern.

PROJECT HEIRLOOM BED	
DRAWING Headboard — Front	DRAWING NO. Headboard-Front_Blueprint
REV 1.0	SHEET 1 OF 1