



TOP-CAP LED CHANNELS — SECTION

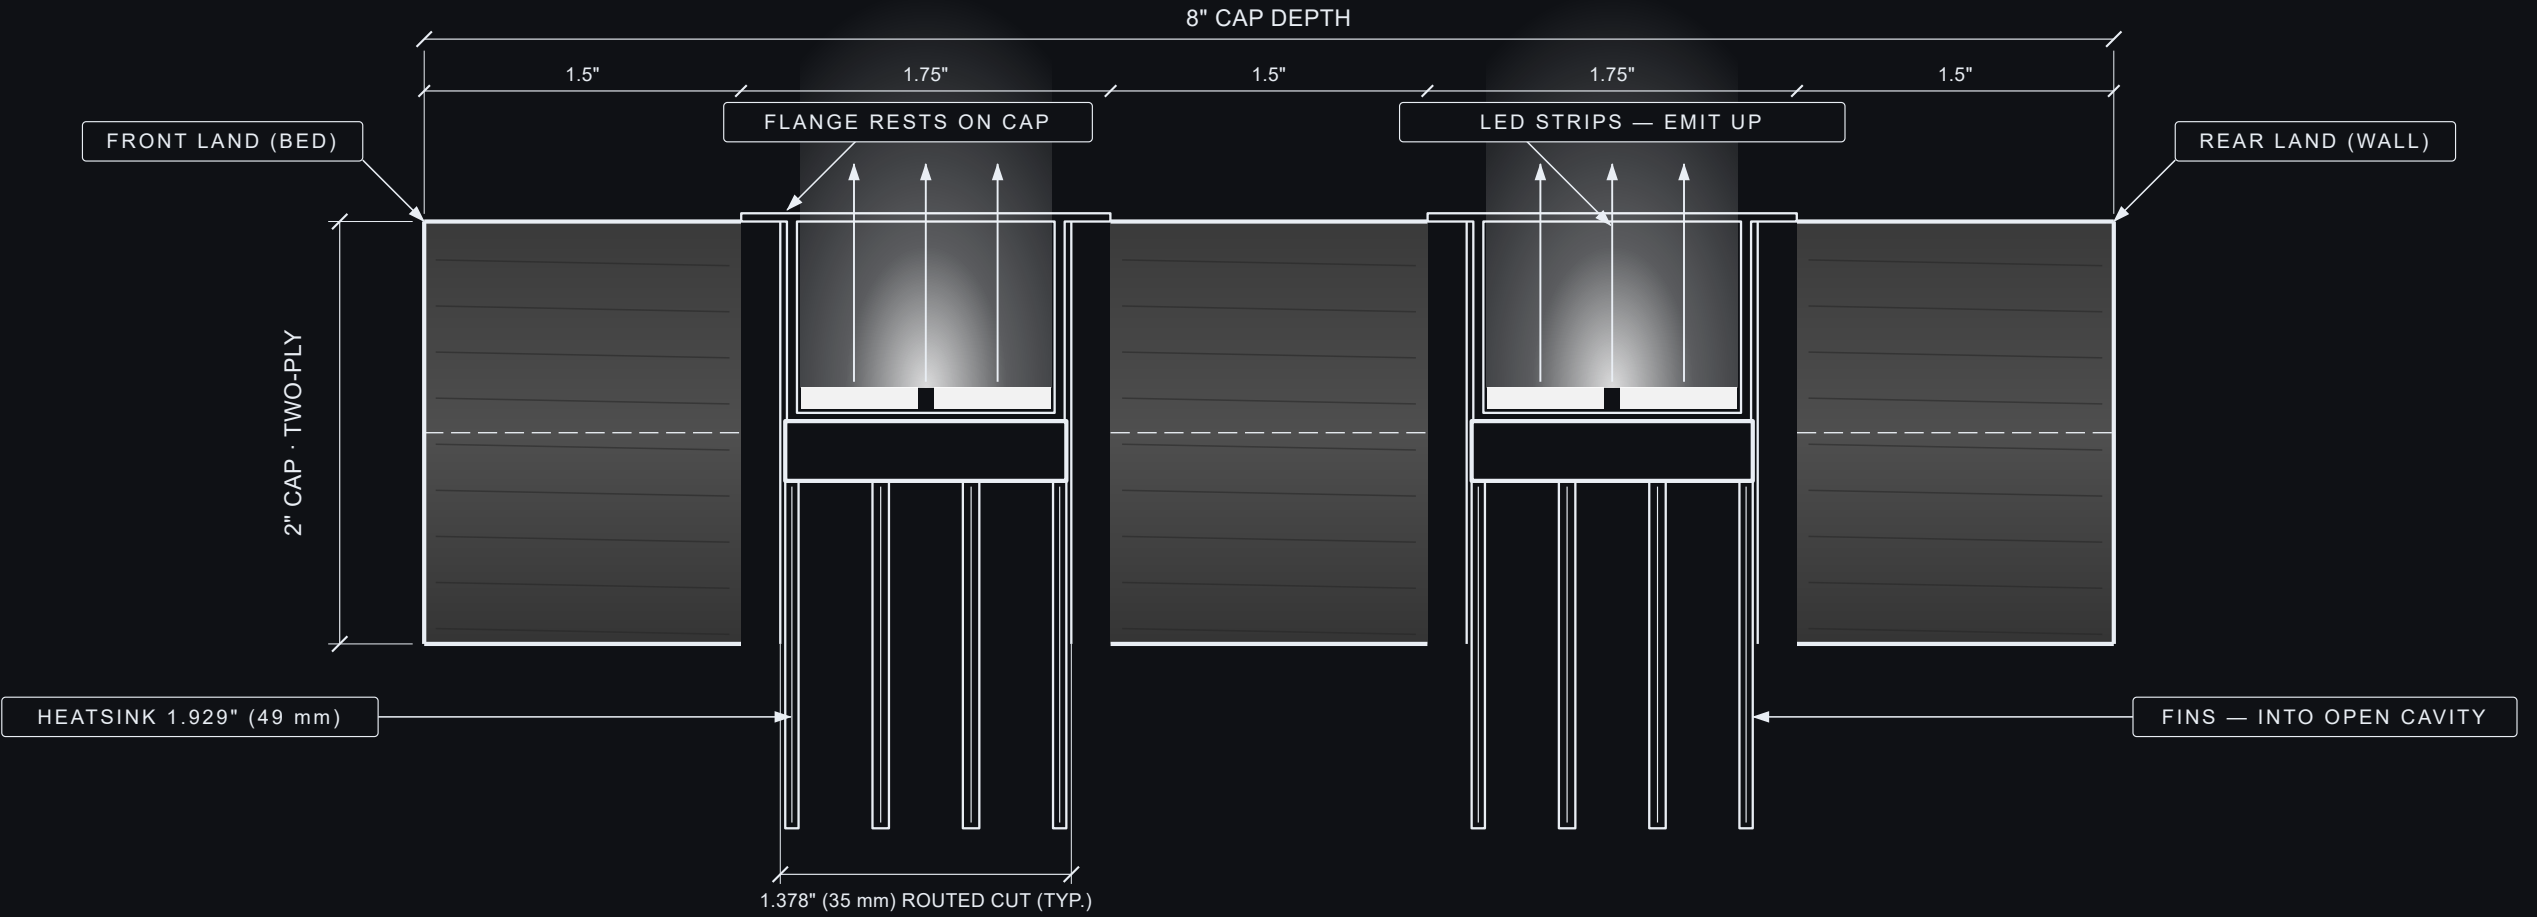

PROJECT	HEIRLOOM BED	SHEET 1 OF 2
DRAWING NO.	TopCap-LED_Blueprint	
LAST UPDATE	2026-06-19 2:19 PM	REV 1.24

TOP-CAP — CONTINUOUS 130" RUN (ISOMETRIC)

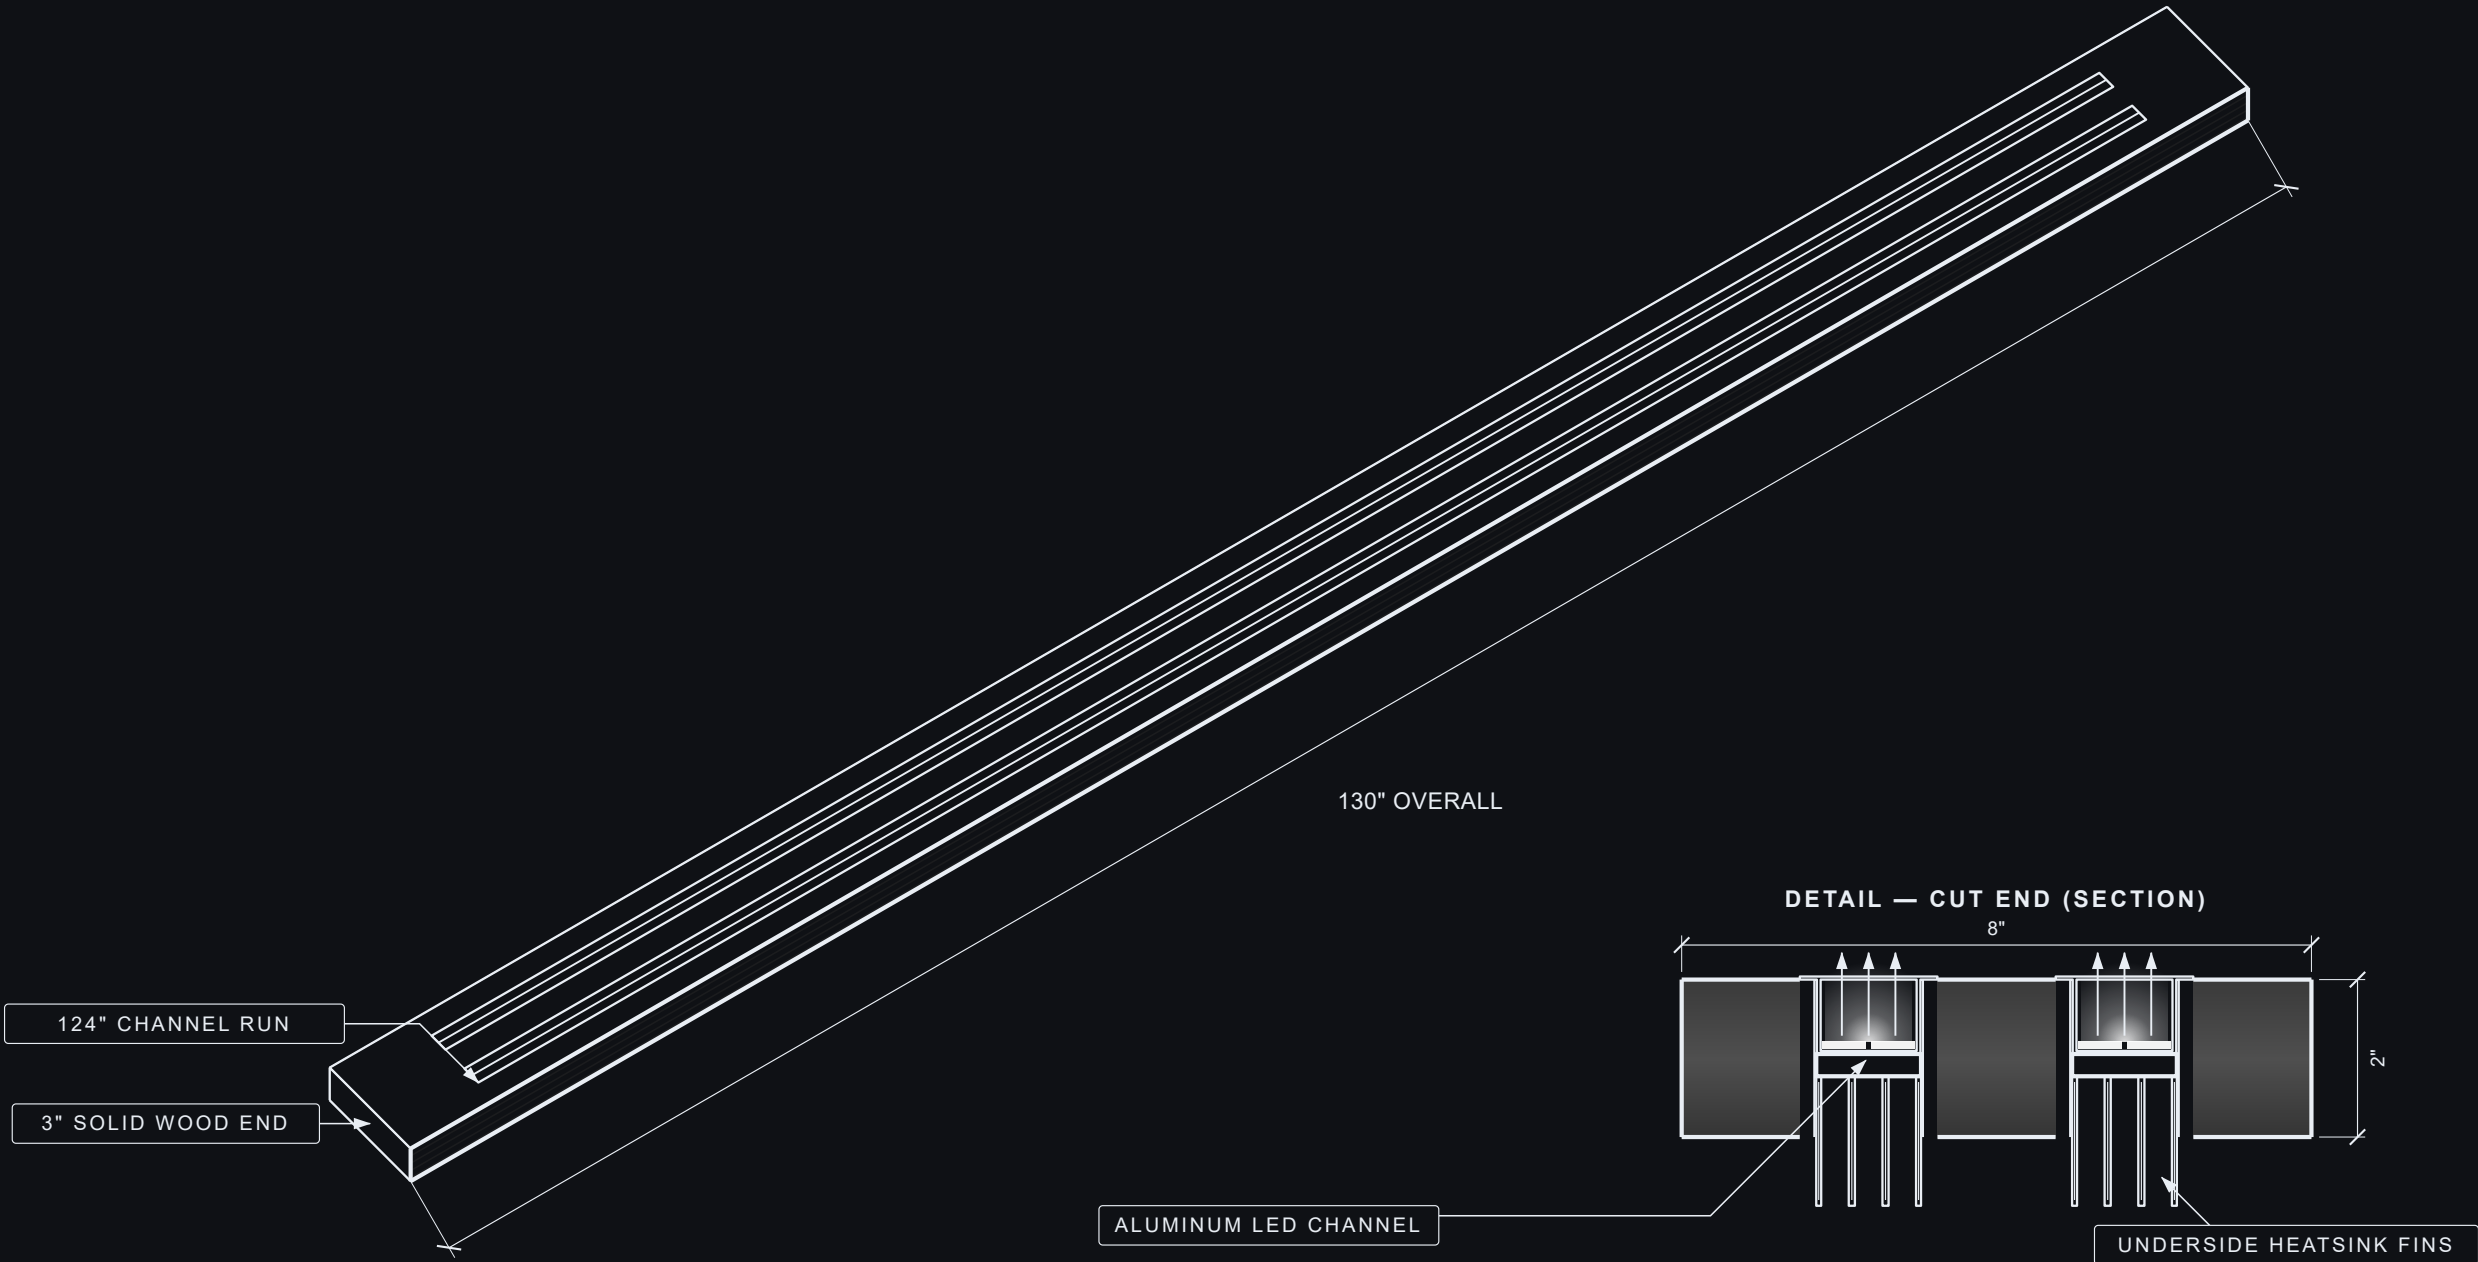

PROJECT	HEIRLOOM BED	SHEET 2 OF 2
DRAWING NO.	TopCap-LED_Blueprint	
LAST UPDATE	2026-06-19 2:19 PM	REV 1.24