


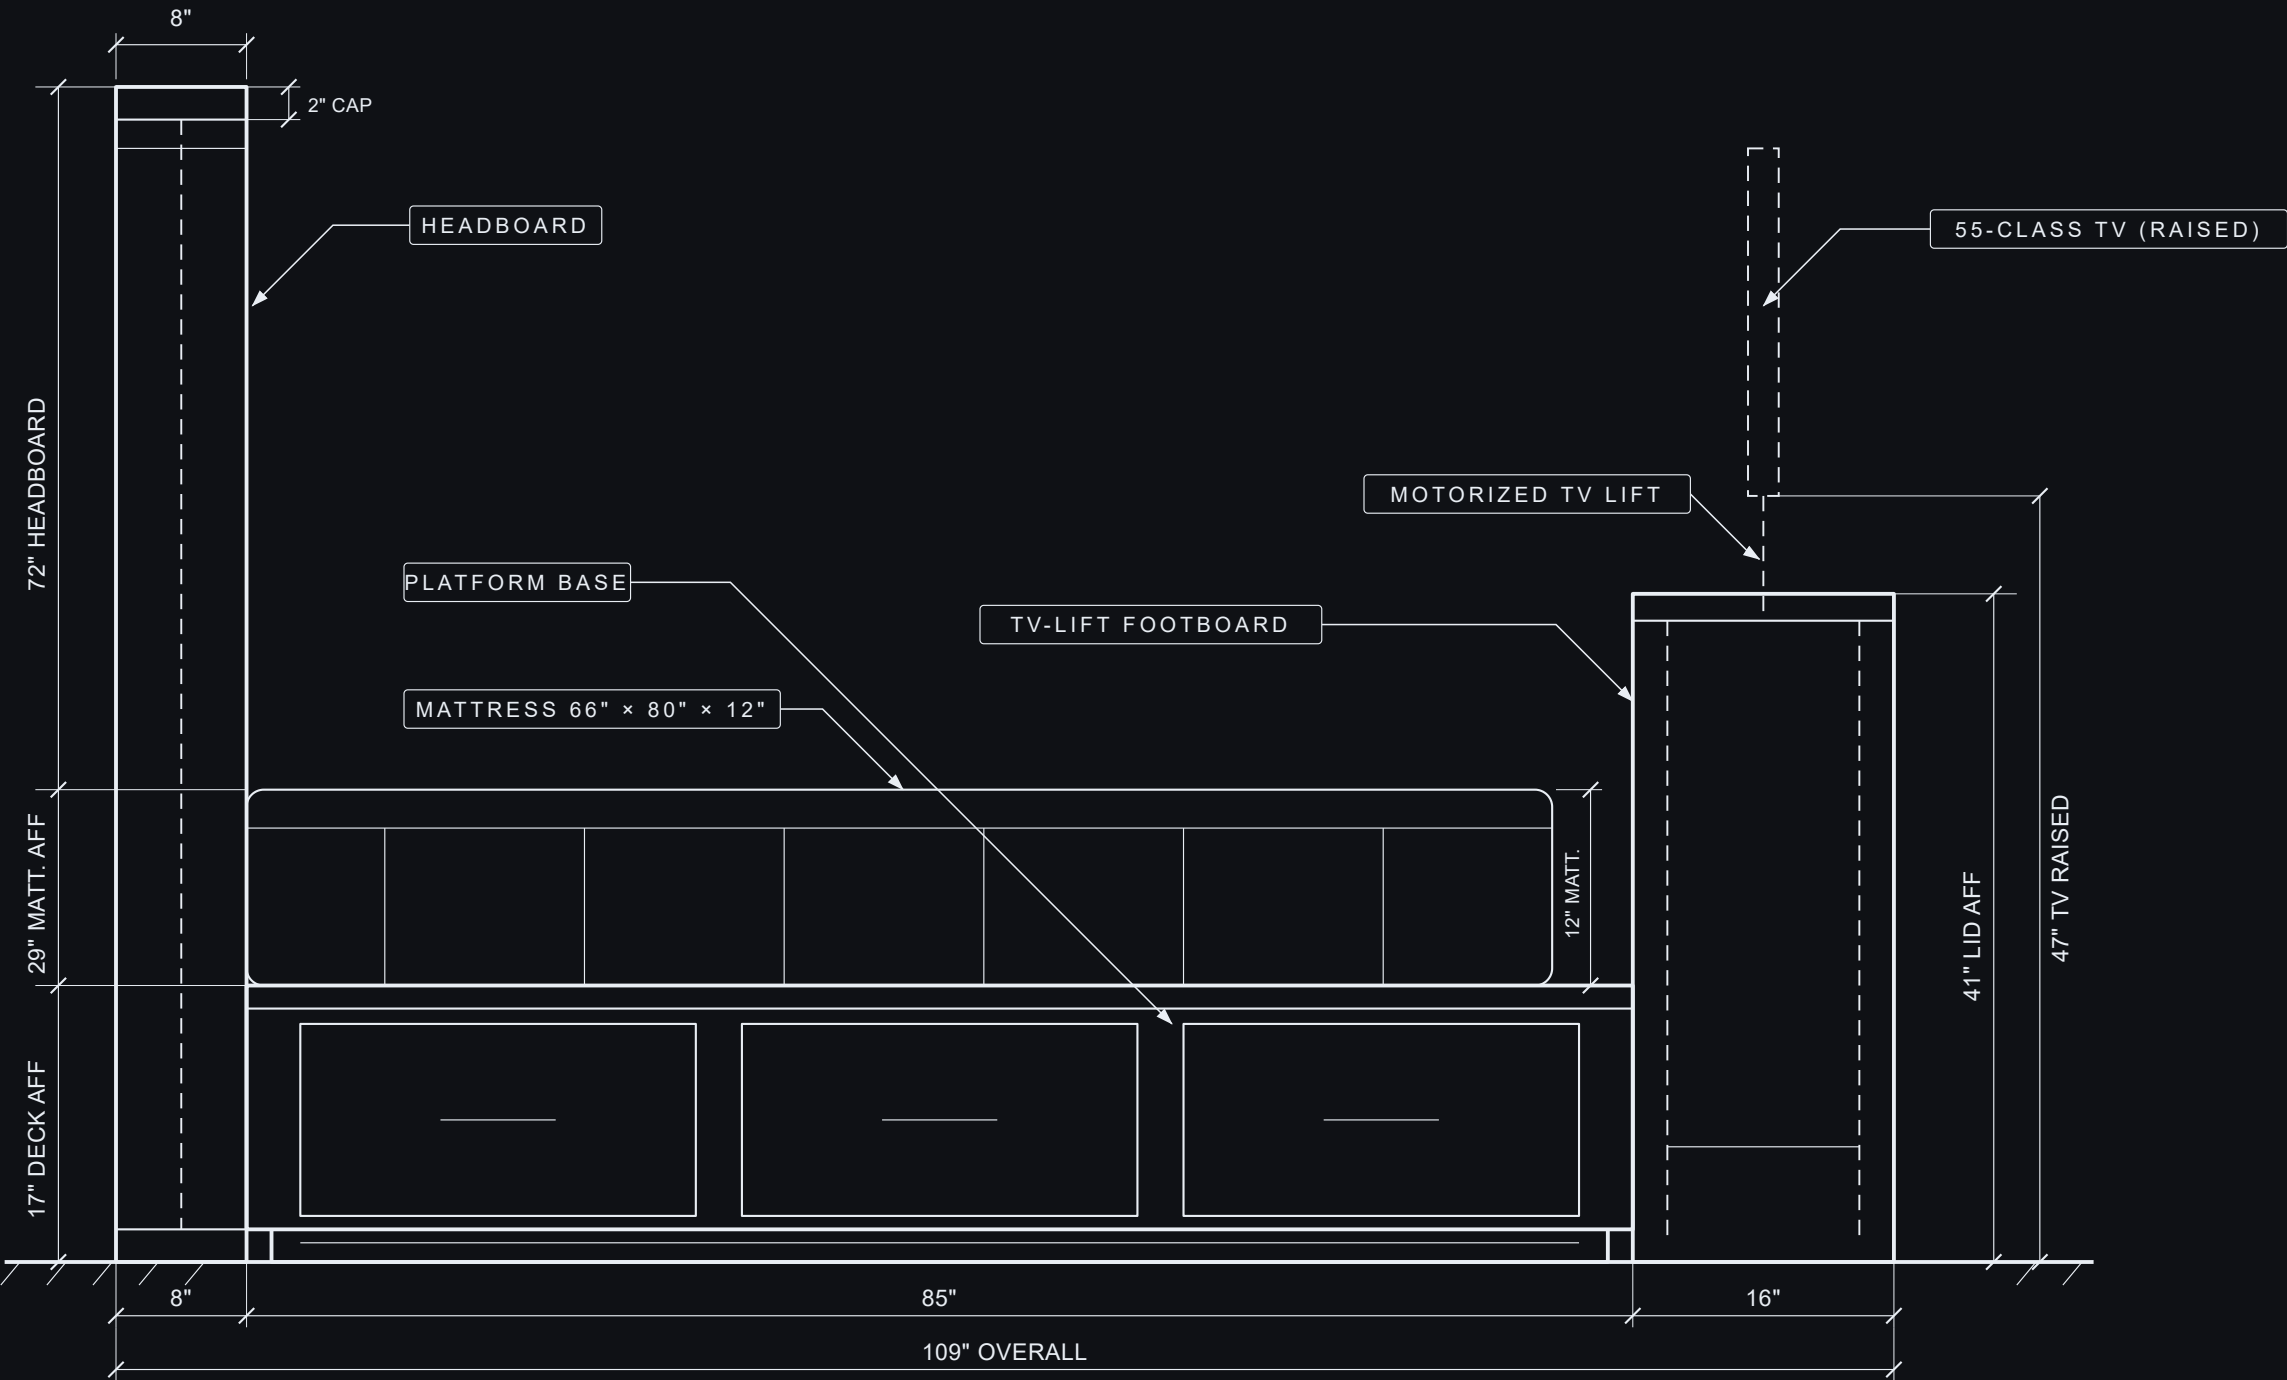

SIDE VIEW



PROJECT HEIRLOOM BED	
DRAWING Side view	DRAWING NO. Bed-Side_Blueprint
REV 1.4	SHEET 1 OF 1