


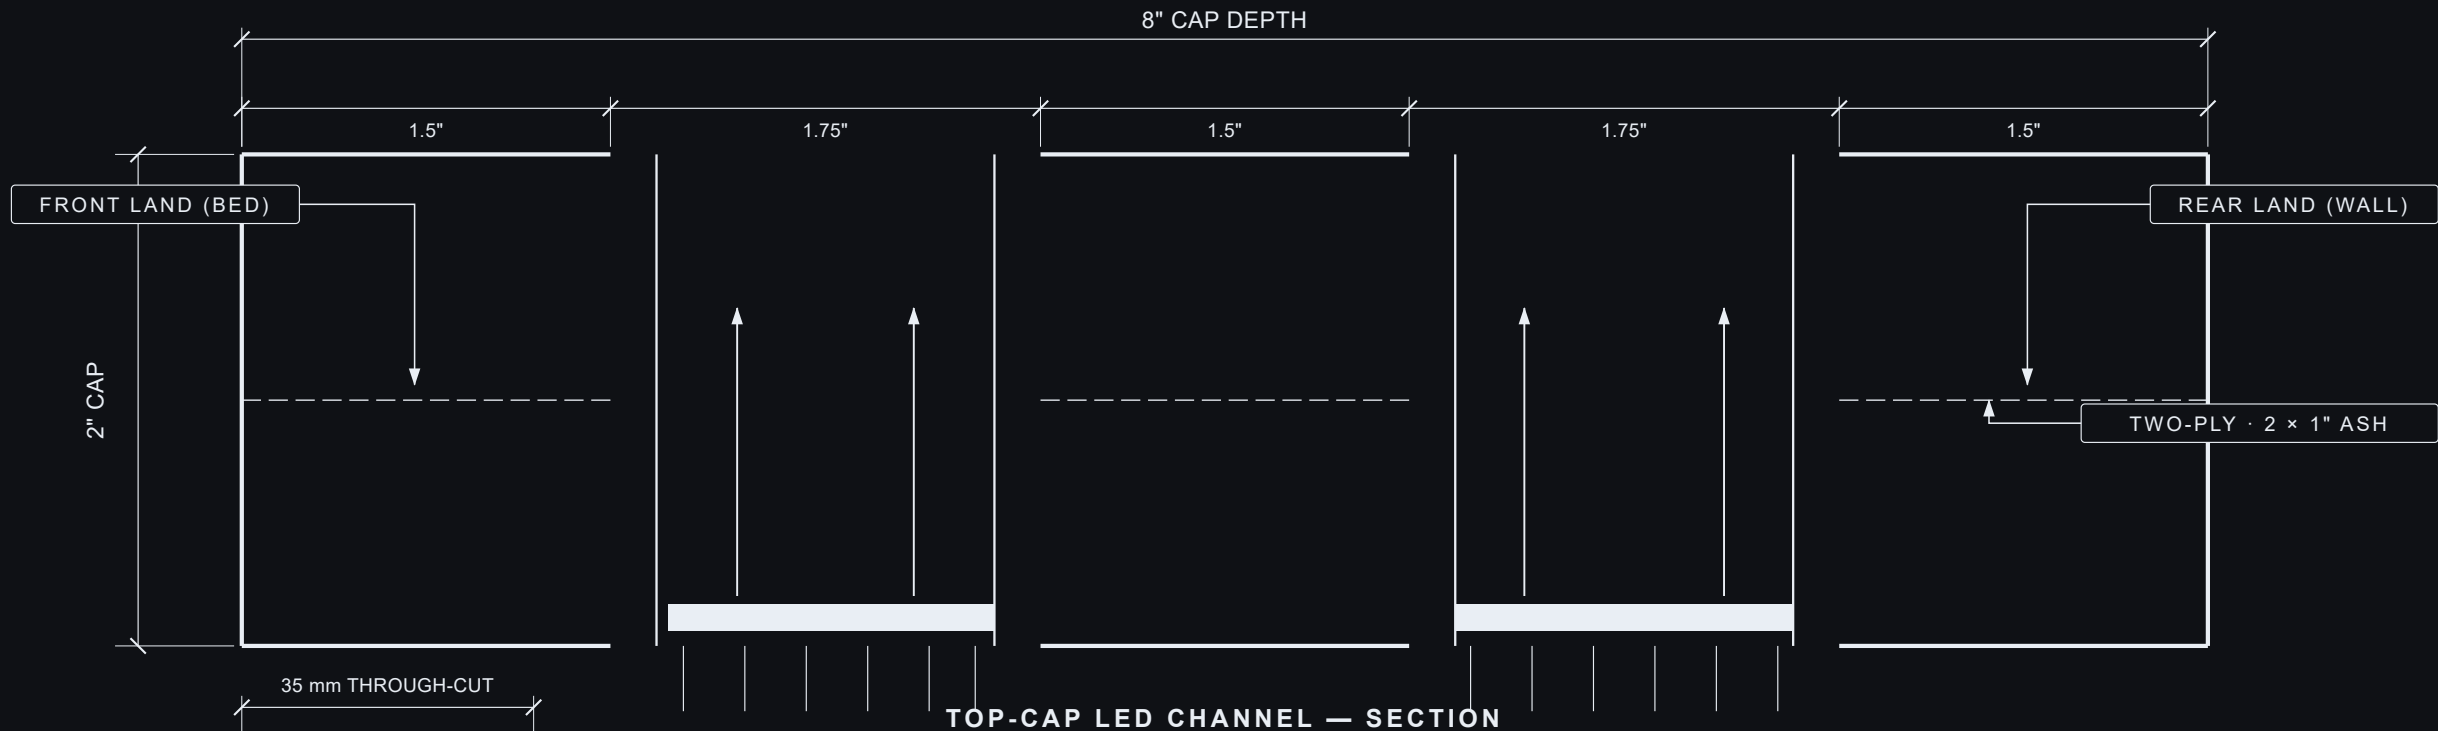

GRAPHIC SCALE (INCHES) · s = 128 px/in



PROJECT HEIRLOOM BED	
DRAWING Top-Cap LED Channel	DRAWING NO. TopCap-LED_Blueprint
REV 1.4	SHEET 1 OF 1