



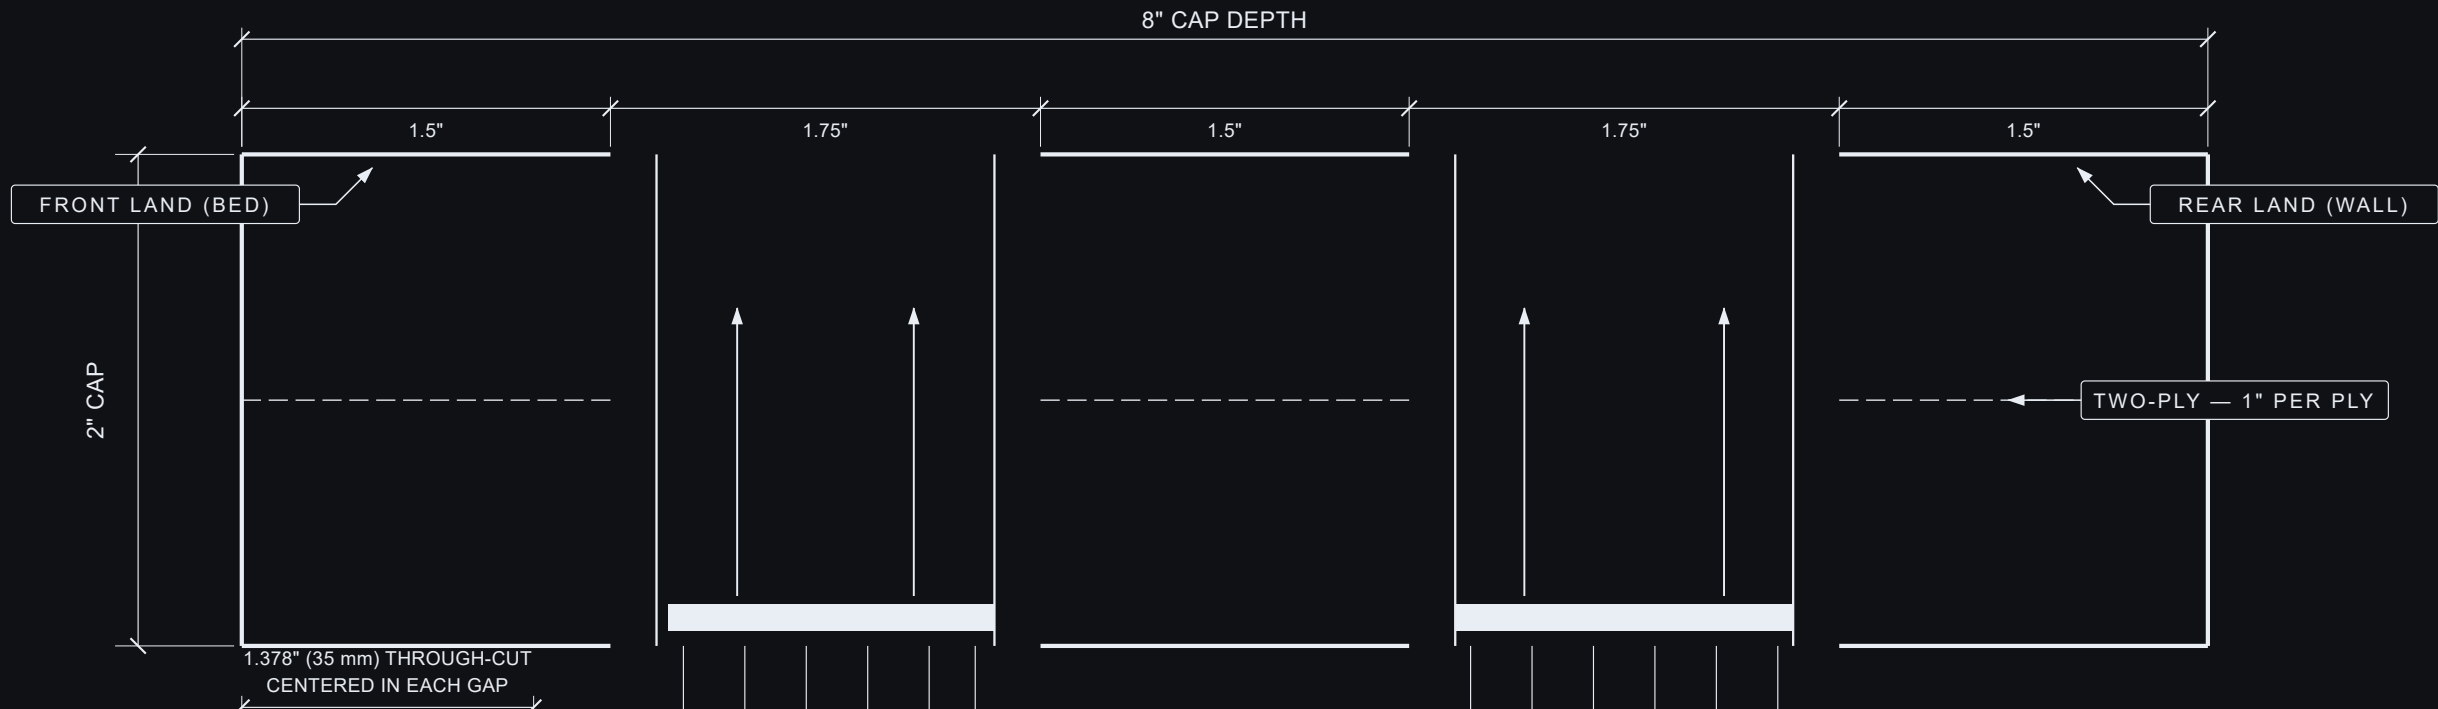

TOP-CAP LED CHANNEL — SECTION

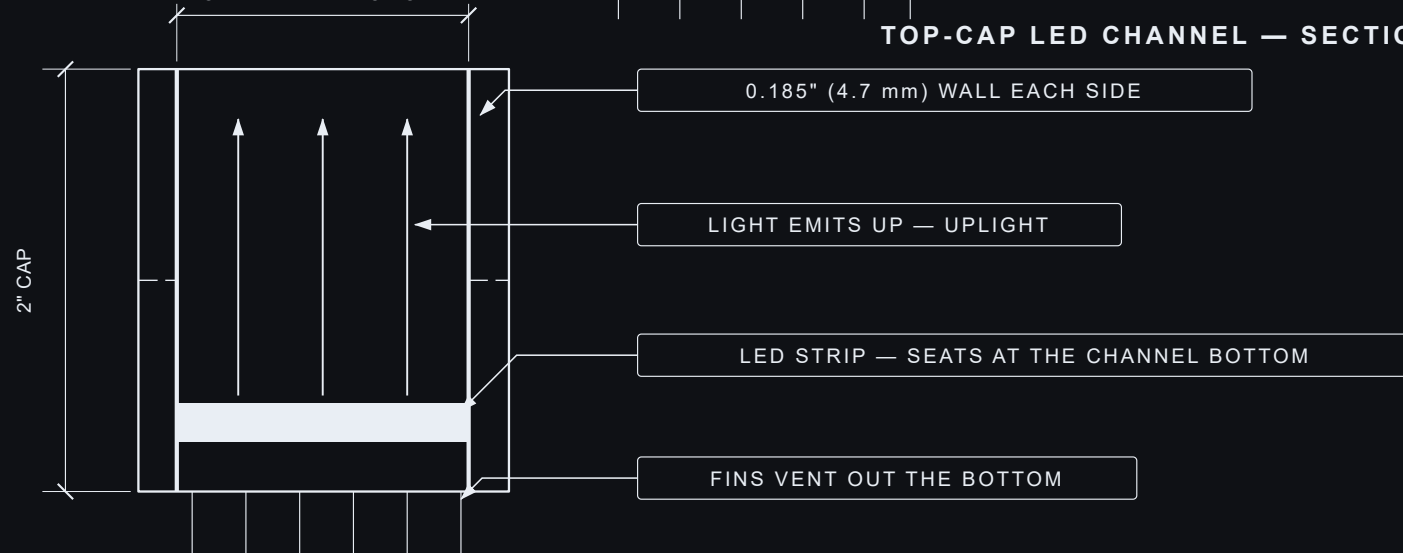

DETAIL A — ENLARGED CHANNEL



PROJECT HEIRLOOM BED	
DRAWING Top-Cap LED Channel	DRAWING NO. TopCap-LED_Blueprint
REV 1.8	SHEET 1 OF 1