



TOP-CAP LED CHANNEL — SECTION

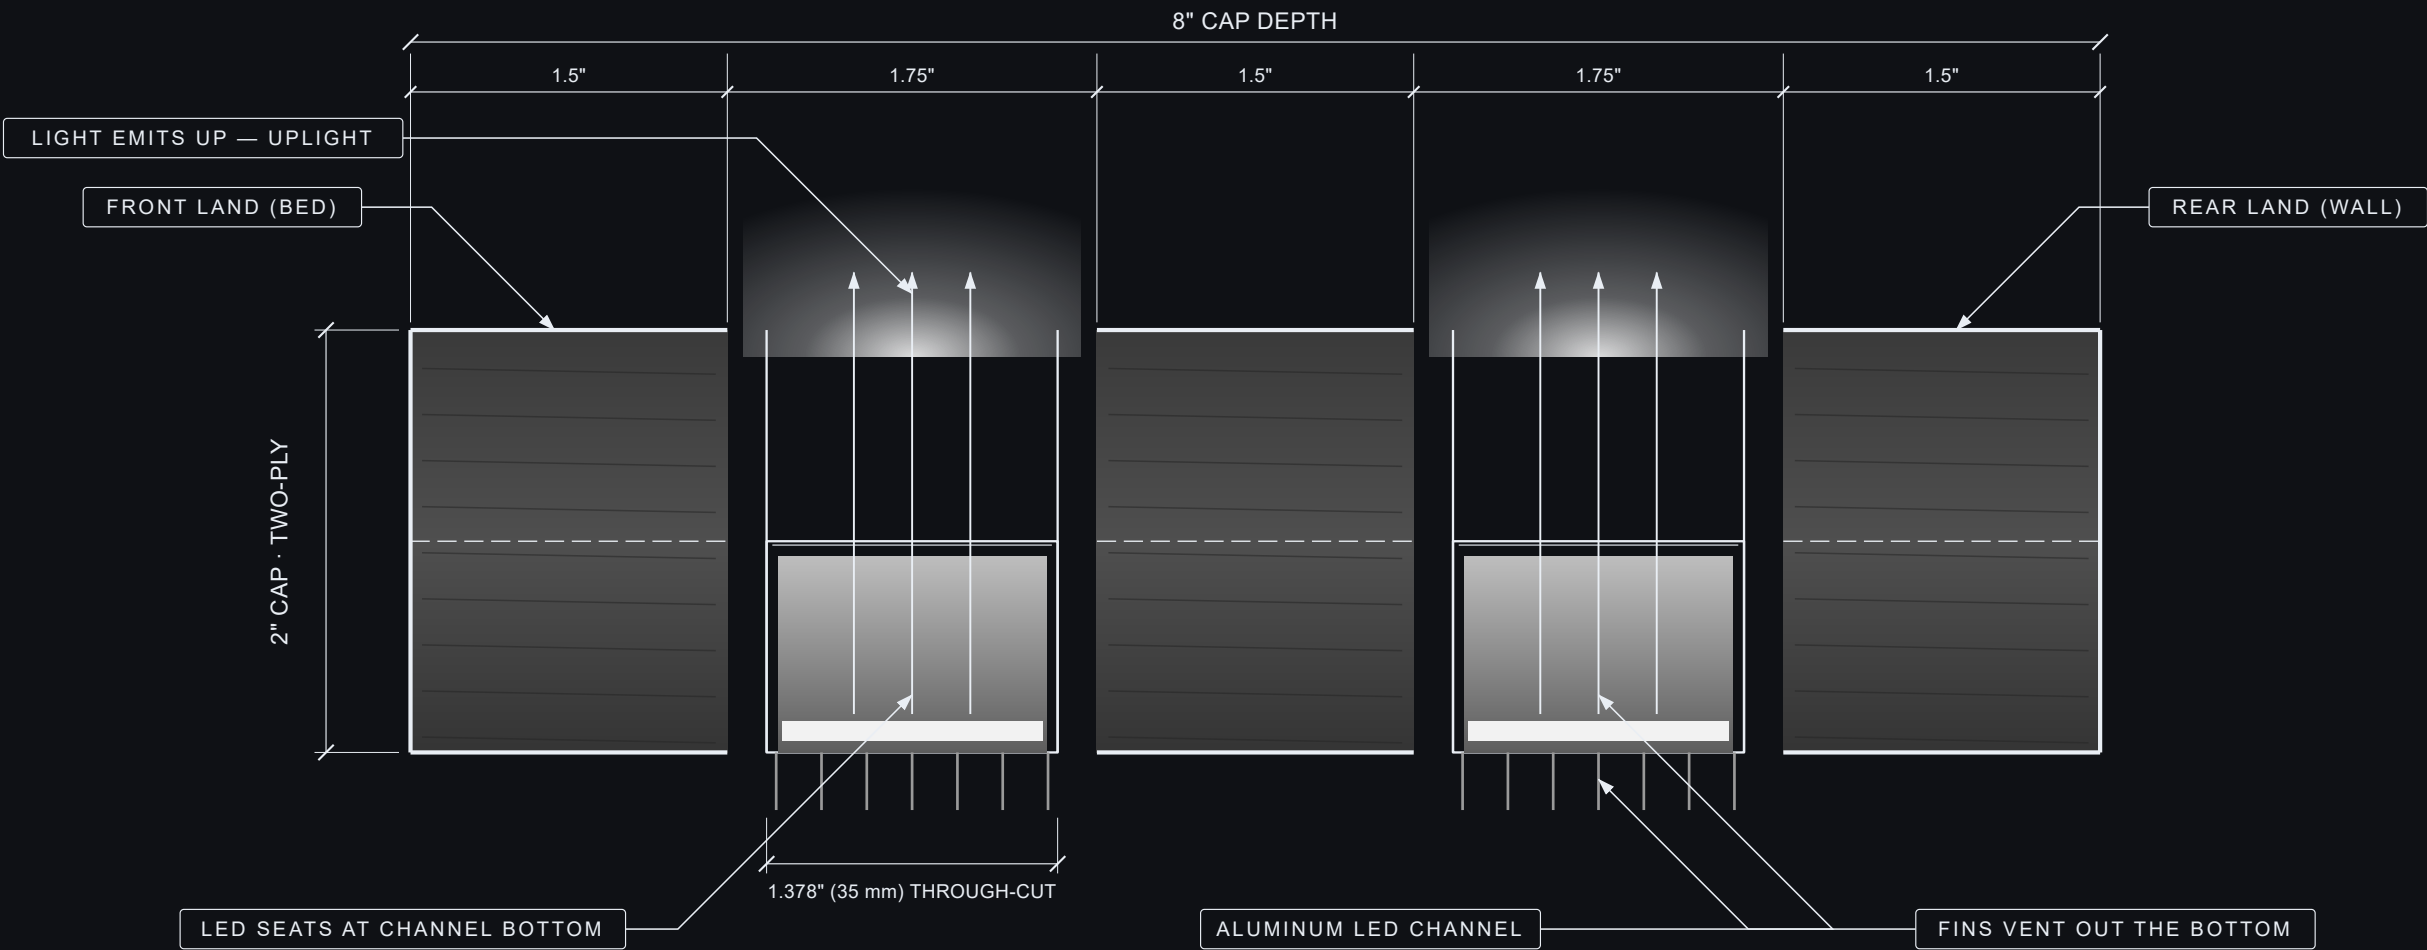


PROJECT	HEIRLOOM BED	SHEET	1 OF 2
DRAWING NO.	TopCap-LED_Blueprint		
LAST UPDATE	2026-06-22 8:49 AM	REV	1.22

TOP-CAP — CONTINUOUS 130" RUN (ISOMETRIC)

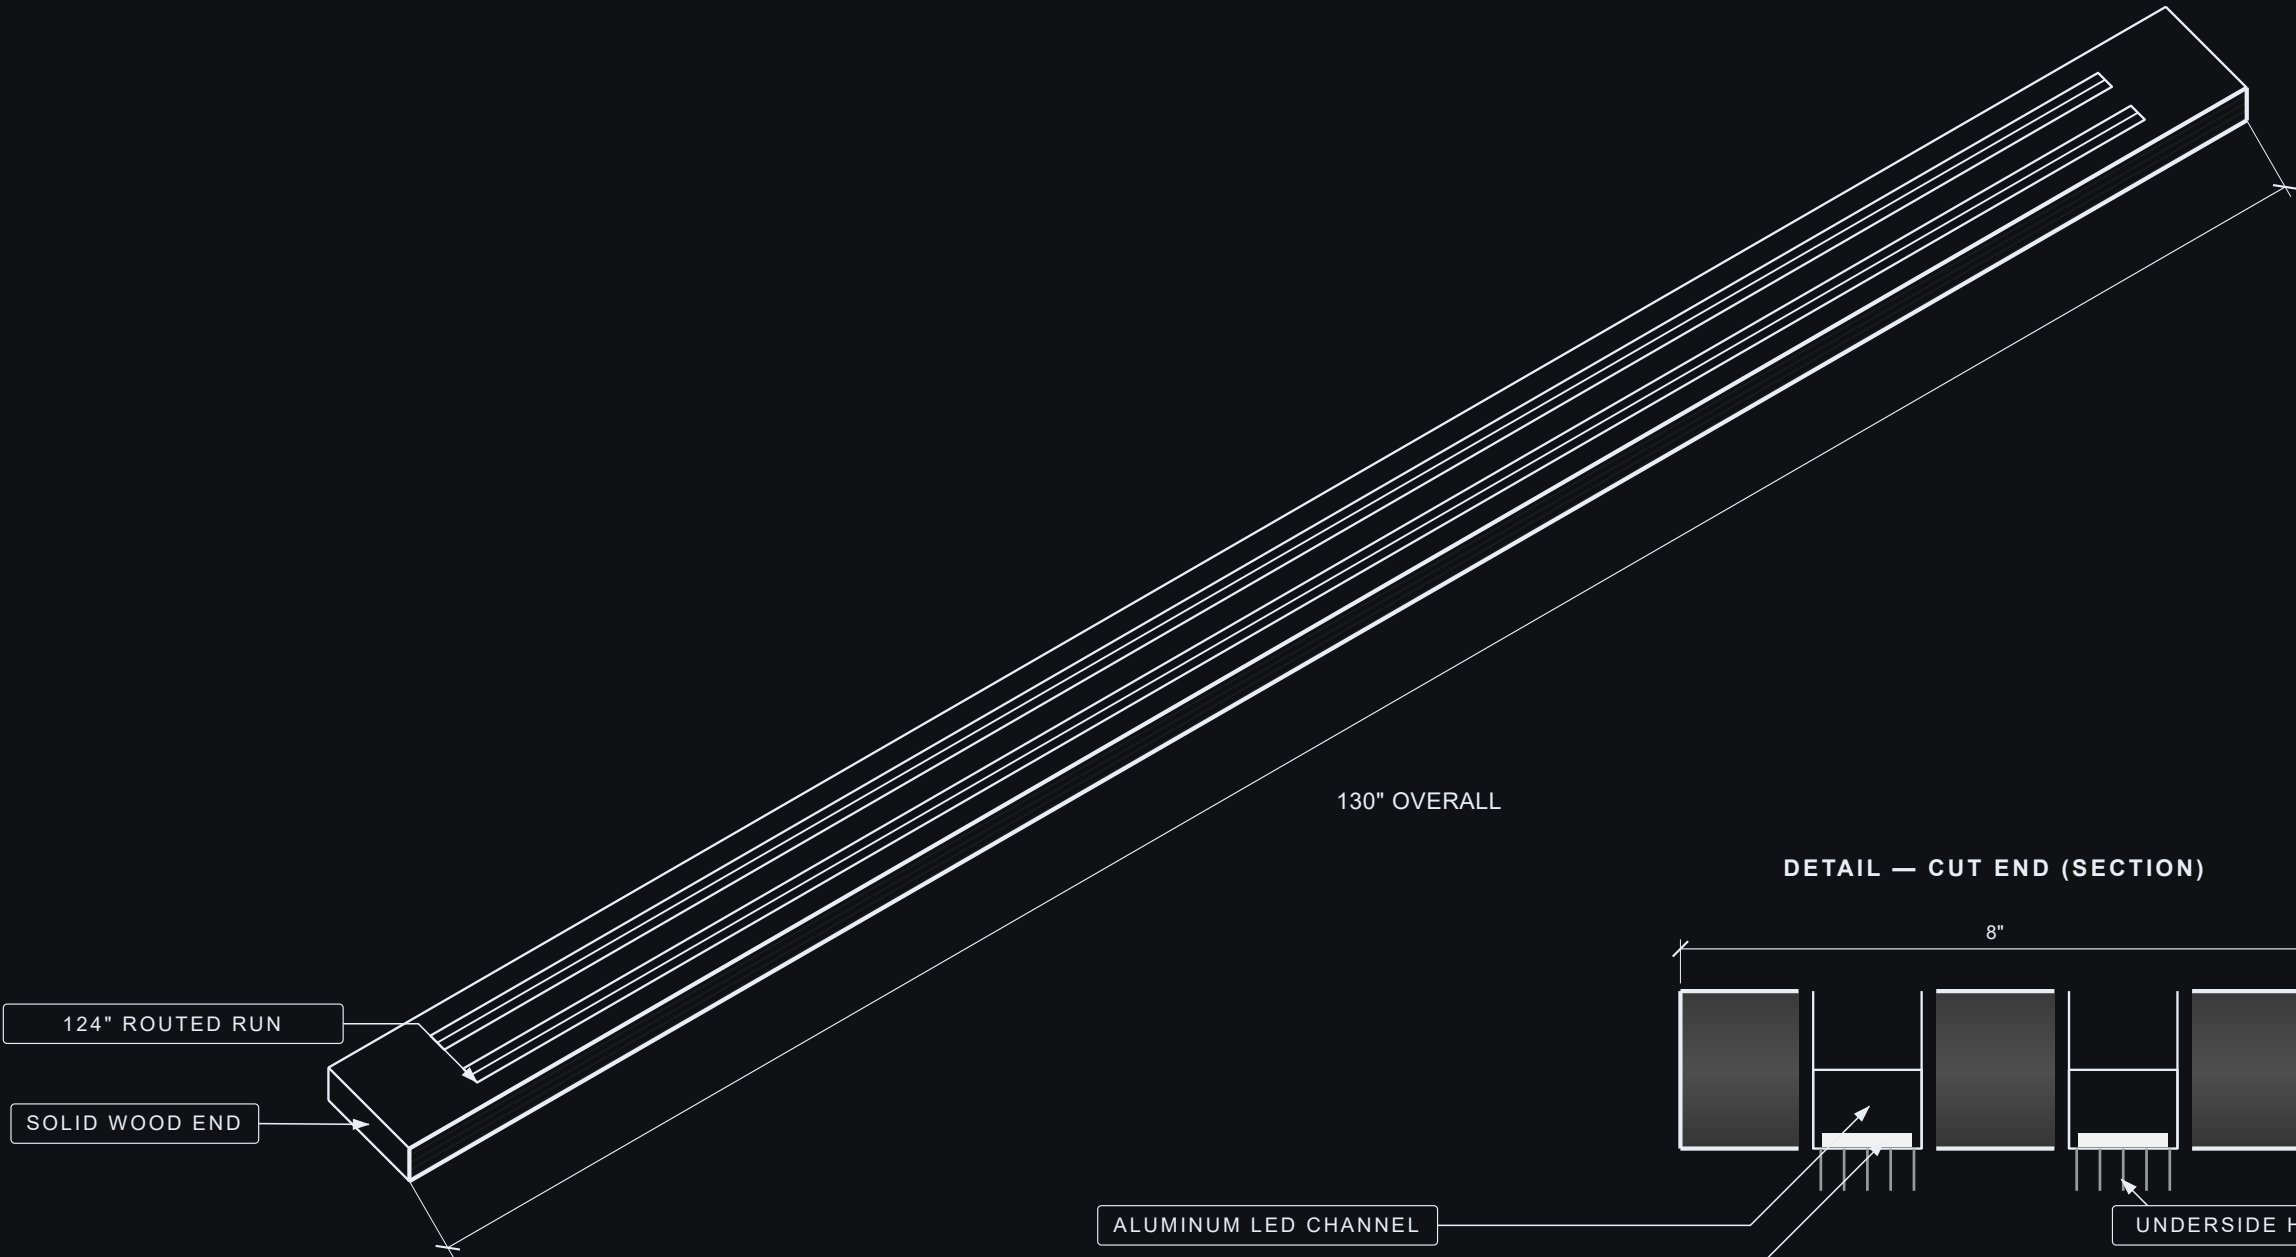

130" OVERALL

DETAIL — CUT END (SECTION)

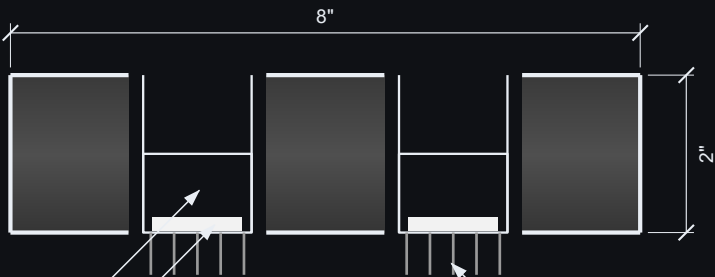

UNDERSIDE HEATSINK FINS

PROJECT	HEIRLOOM BED	SHEET 2 OF 2
DRAWING NO.	TopCap-LED_Blueprint	
LAST UPDATE	2026-06-22 8:49 AM	REV 1.22