

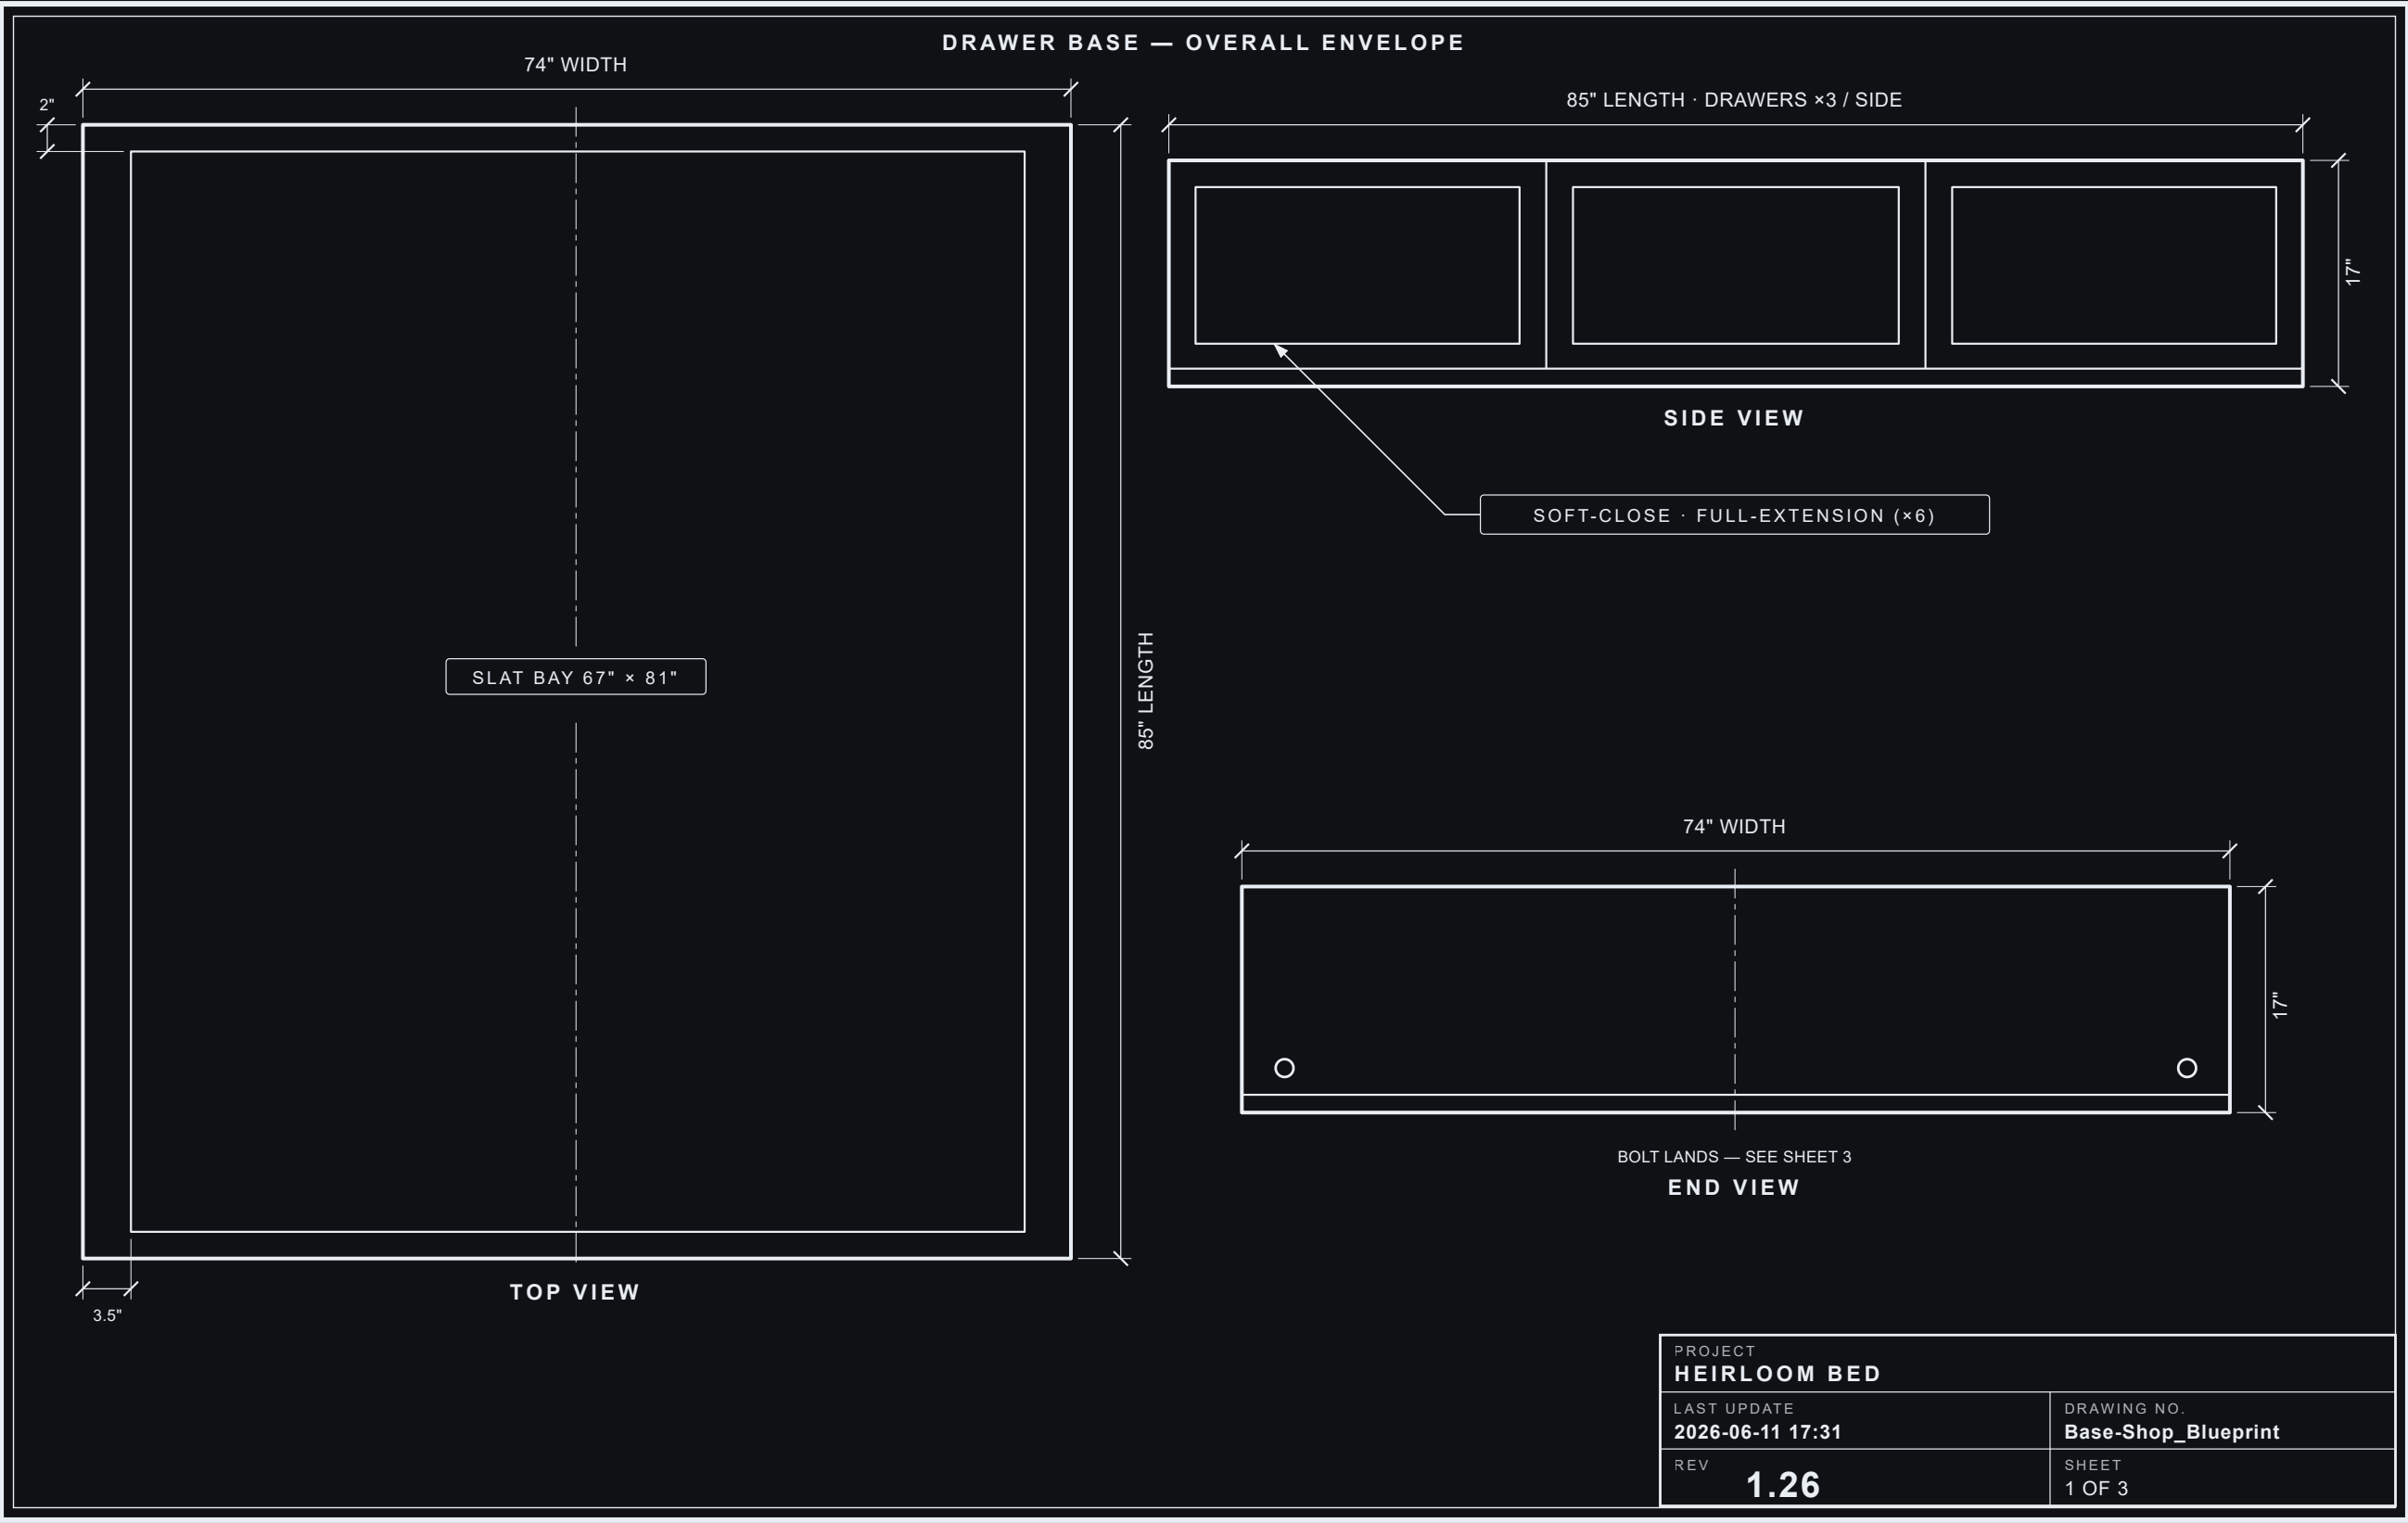


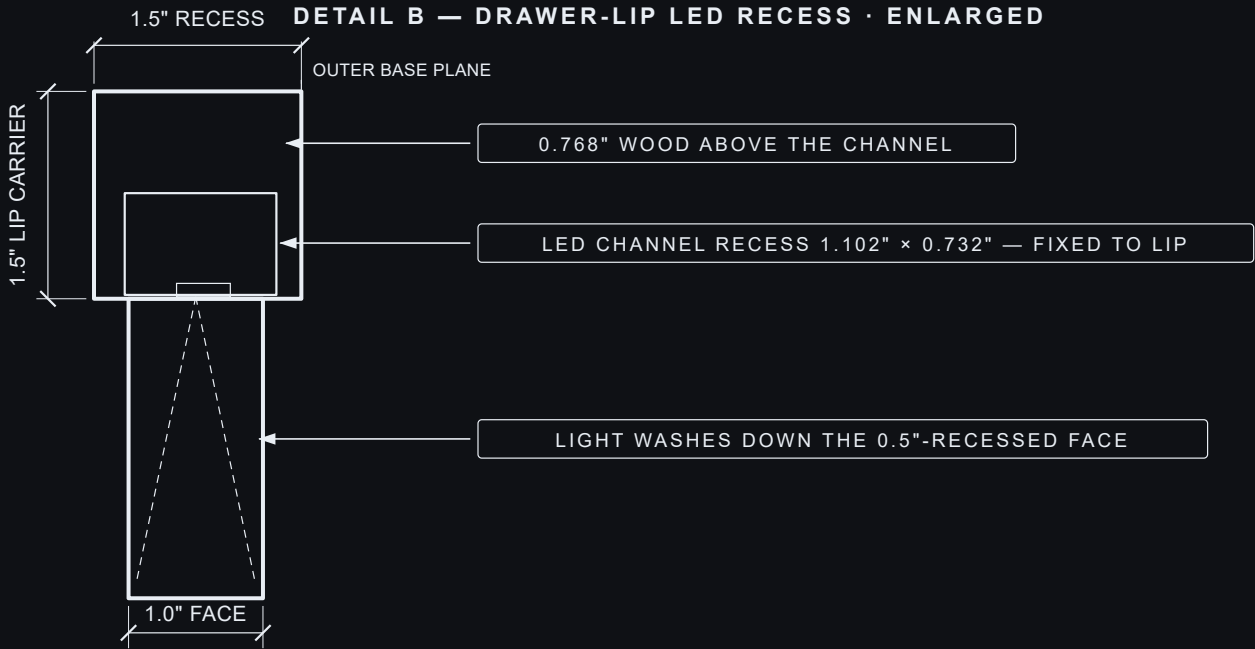



SECTION DETAILS

SECTION A-A · TRANSVERSE (ACROSS THE WIDTH)

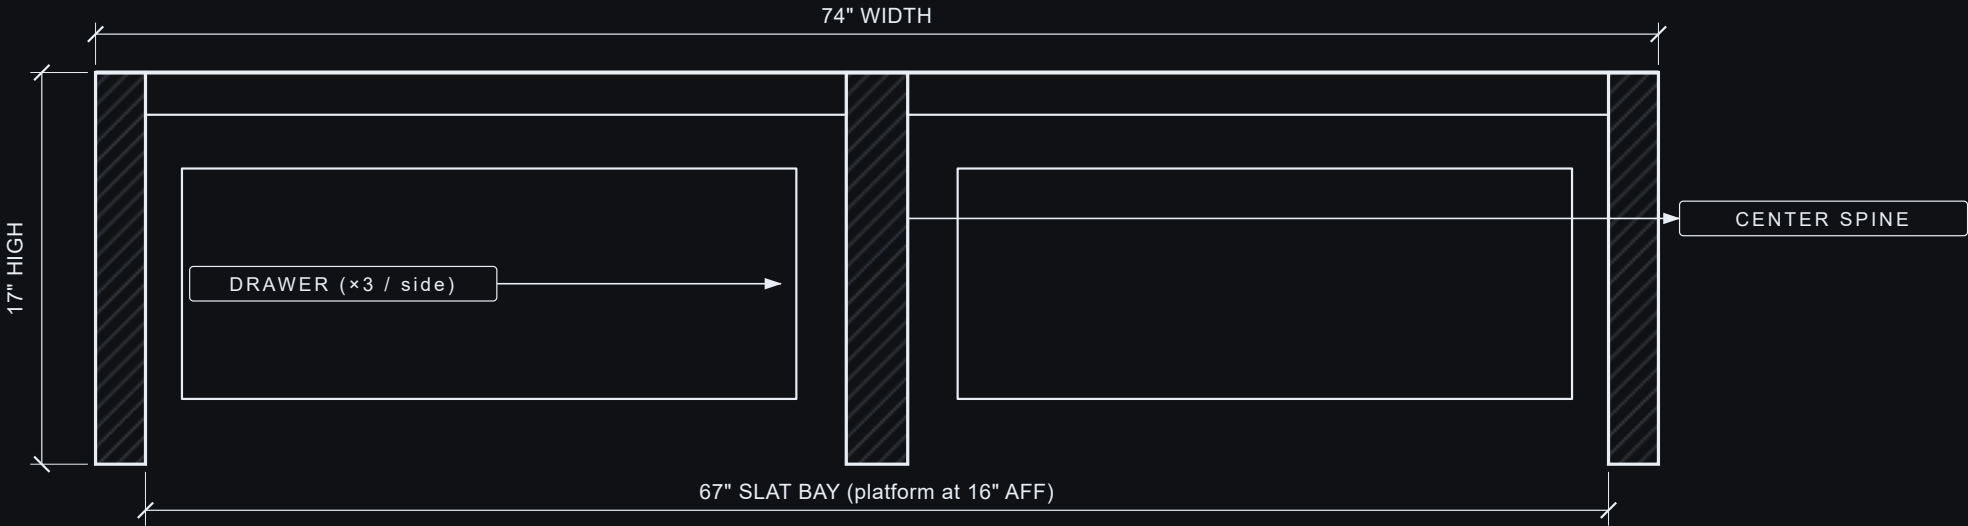

PROJECT HEIRLOOM BED	
LAST UPDATE 2026-06-11 17:31	DRAWING NO. Base-Shop_Blueprint
REV 1.26	SHEET 2 OF 3

CRITICAL INTERFACES — BASE BOLT LANDS

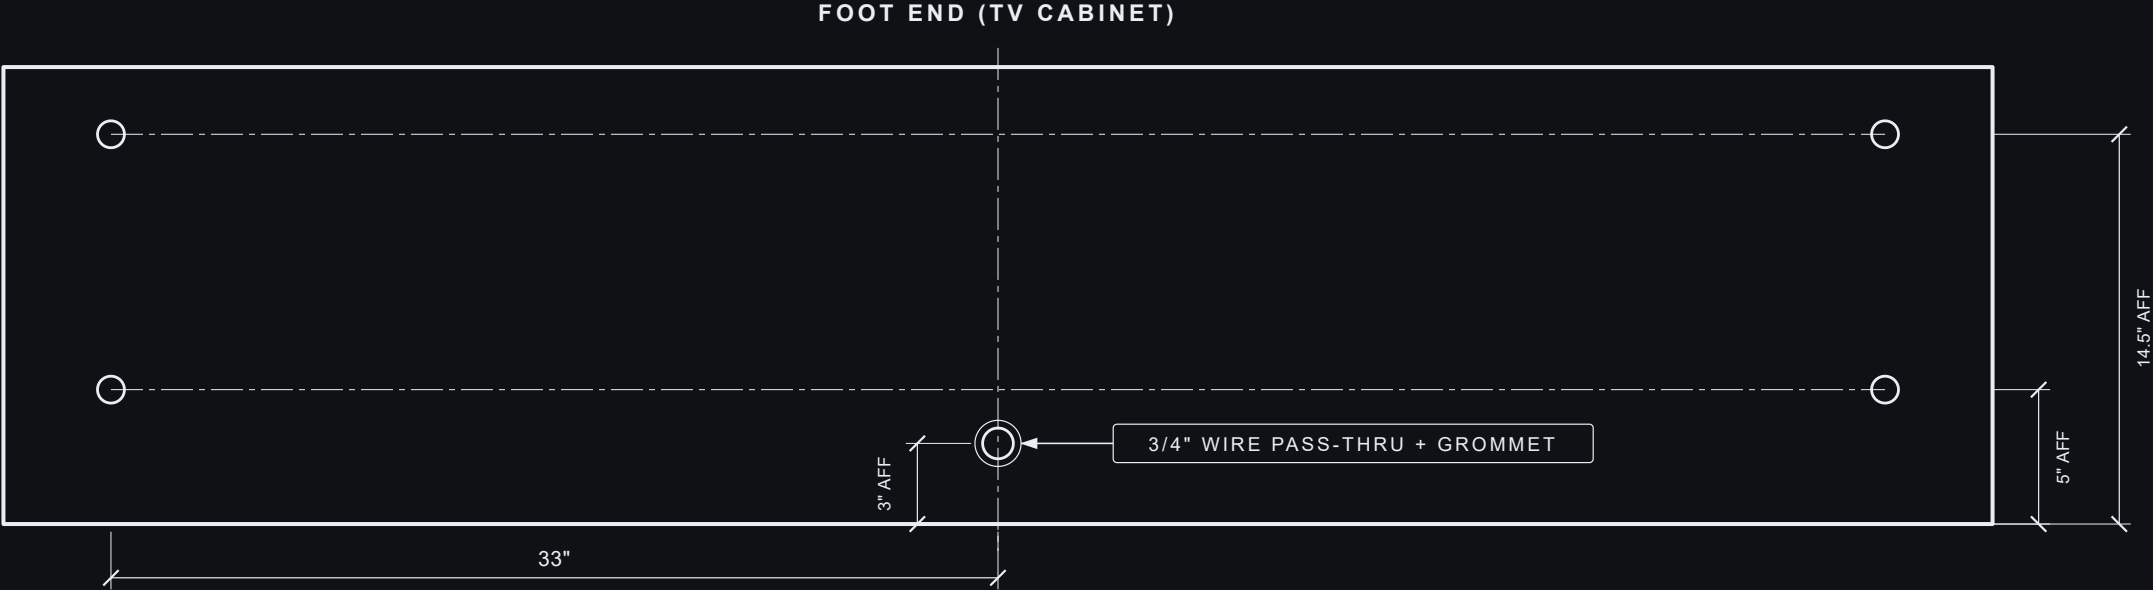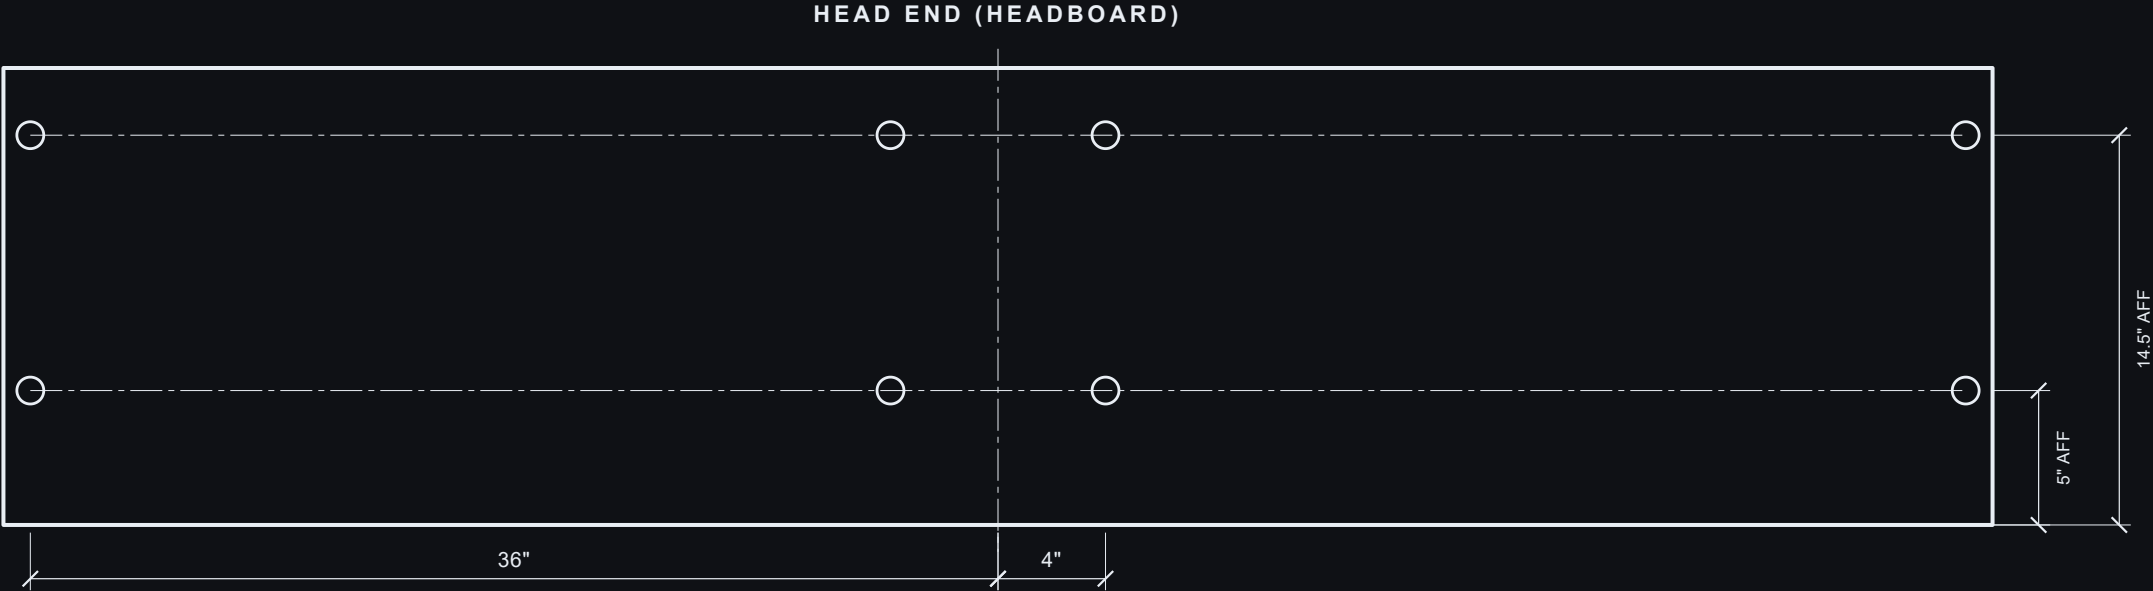

PROJECT HEIRLOOM BED	
LAST UPDATE 2026-06-11 17:31	DRAWING NO. Base-Shop_Blueprint
REV 1.26	SHEET 3 OF 3