


FRONT VIEW — WHOLE BED · TV CABINET REMOVED

130" HEADBOARD (OVERALL)

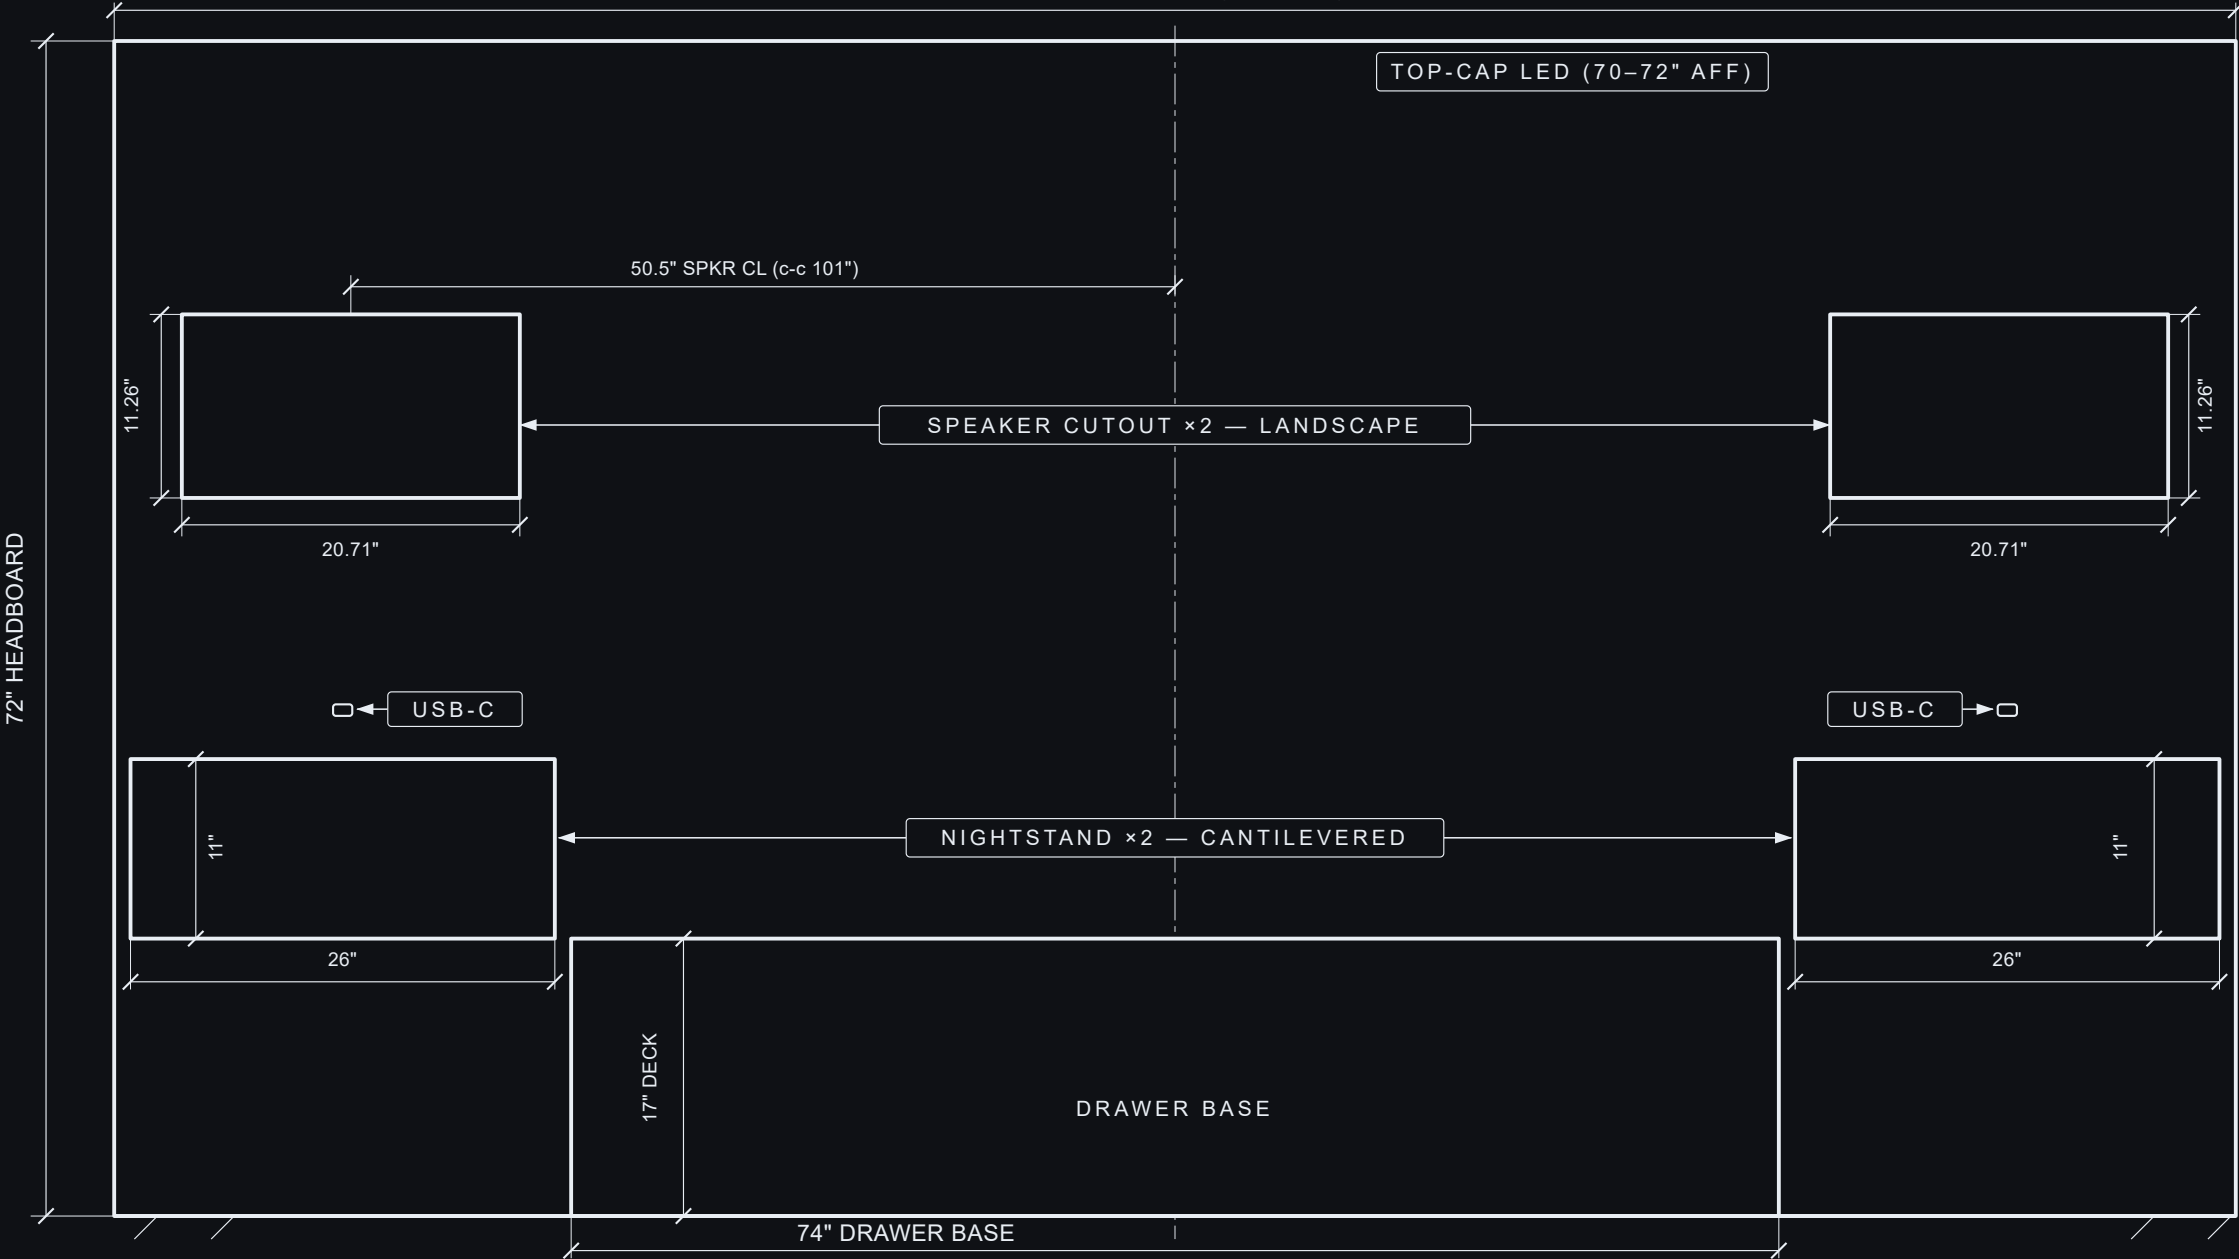

TV CABINET (FOOTBOARD) REMOVED — SEE TV-Cabinet_Blueprint

PROJECT HEIRLOOM BED	
LAST UPDATE 2026-06-11 17:31	DRAWING NO. Bed-Front_Blueprint
REV 4.1	SHEET 1 OF 1