


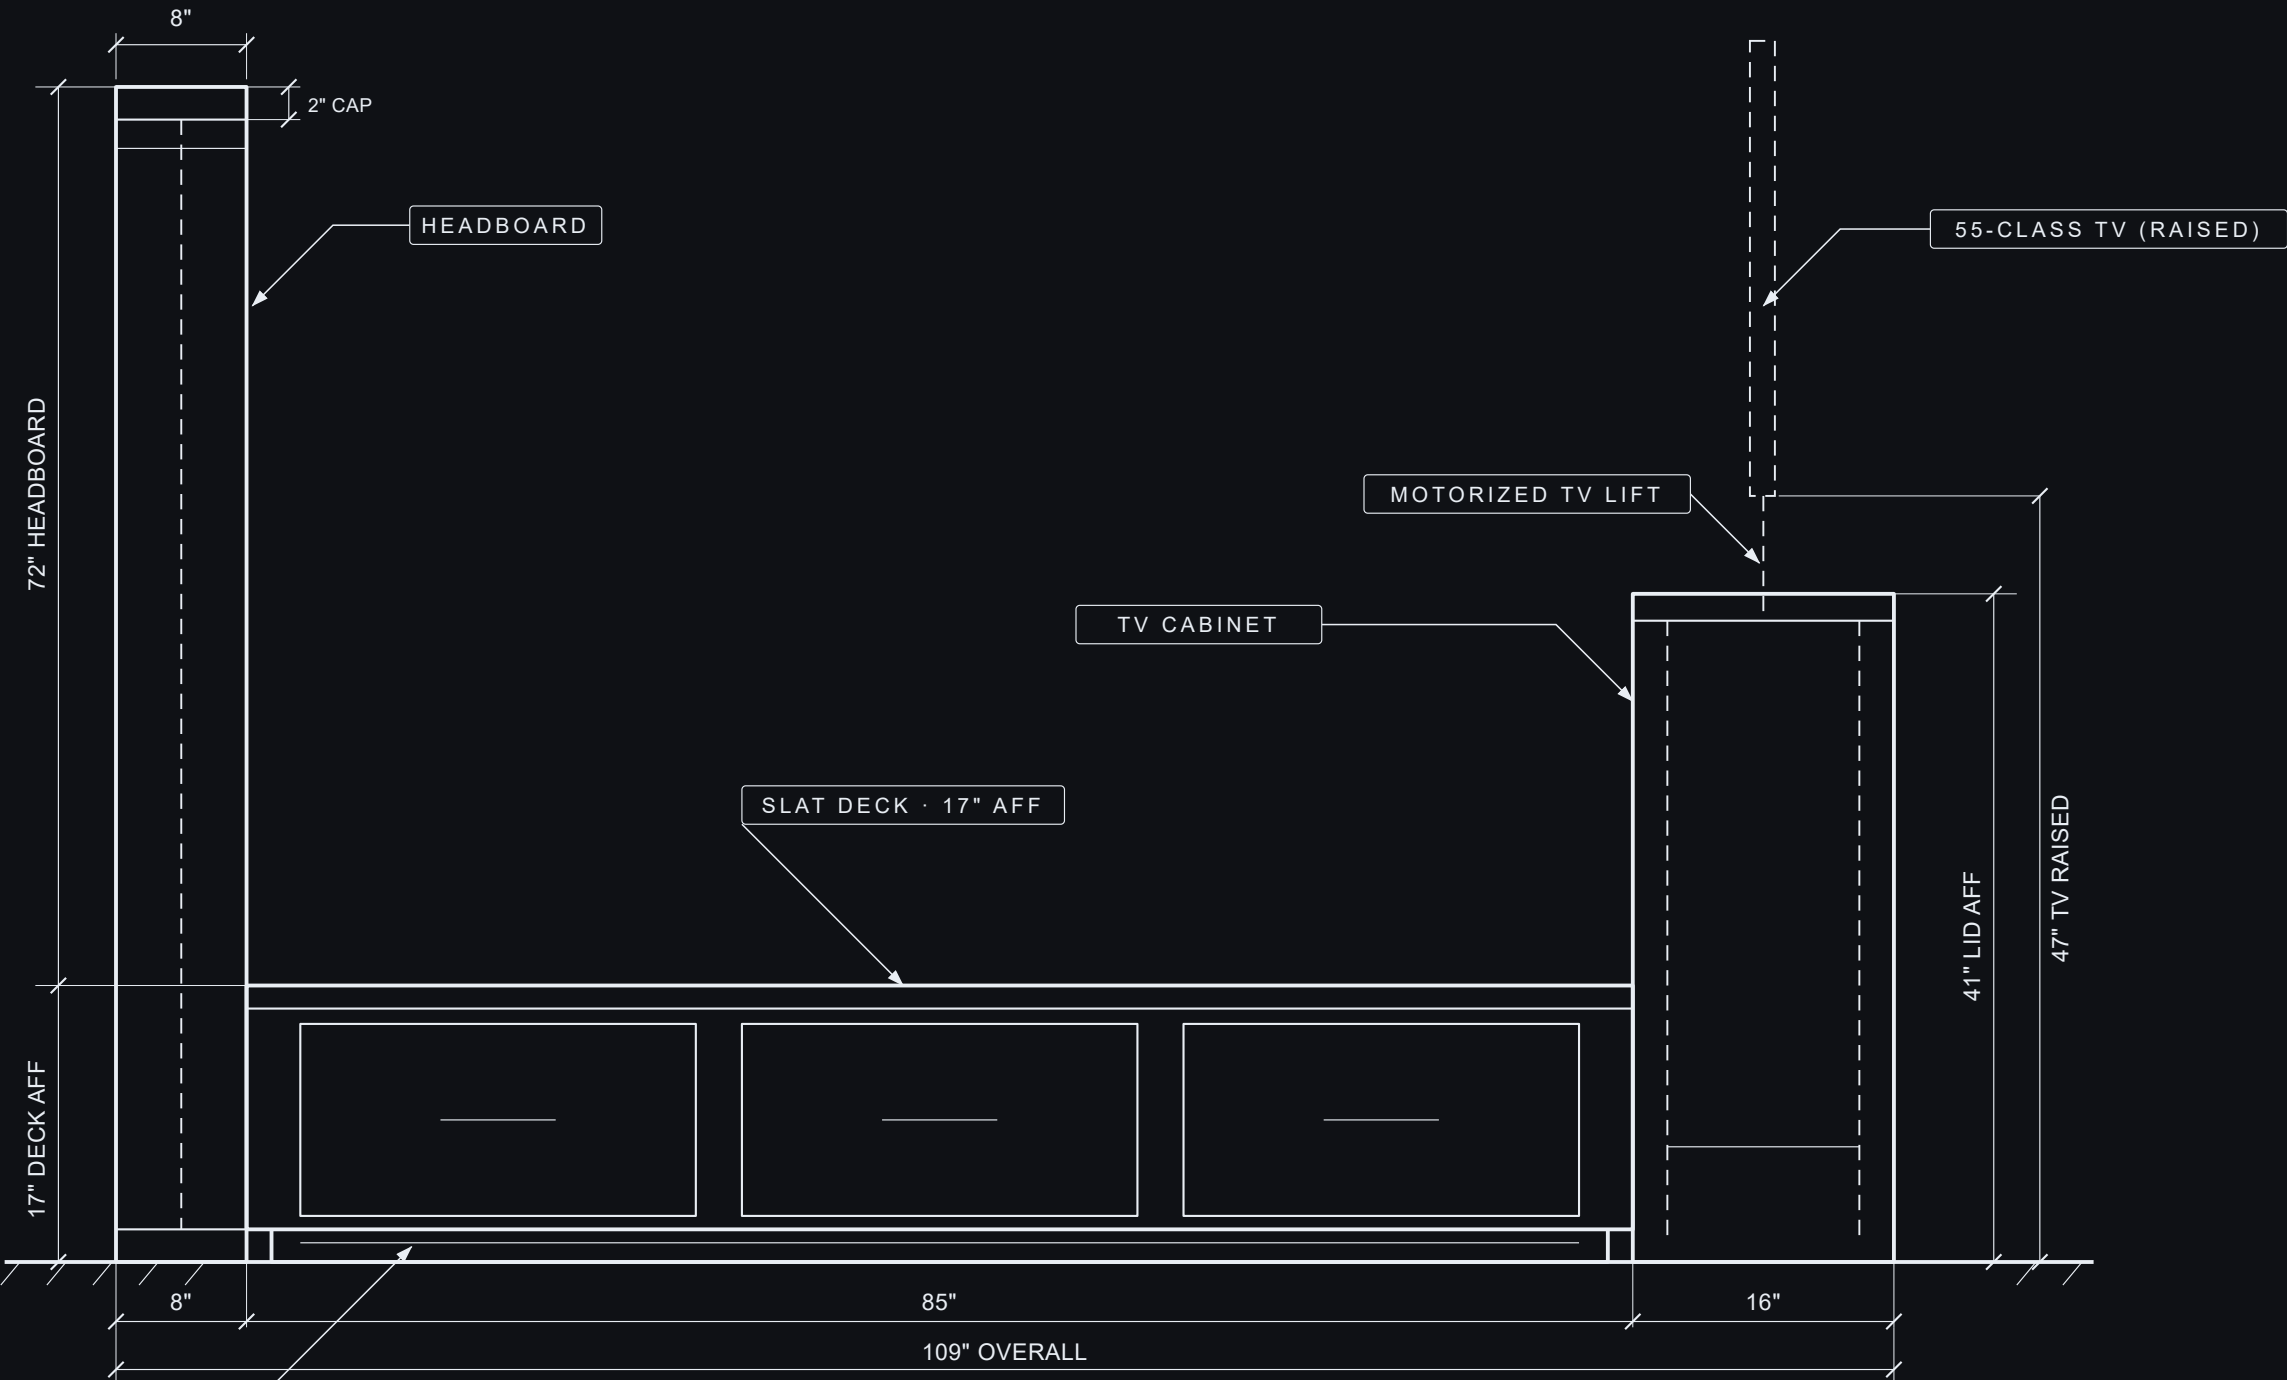

SIDE VIEW

|                                 |                                   |
|---------------------------------|-----------------------------------|
| PROJECT<br>HEIRLOOM BED         |                                   |
| LAST UPDATE<br>2026-06-11 17:31 | DRAWING NO.<br>Bed-Side_Blueprint |
| REV<br>1.14                     | SHEET<br>1 OF 1                   |