


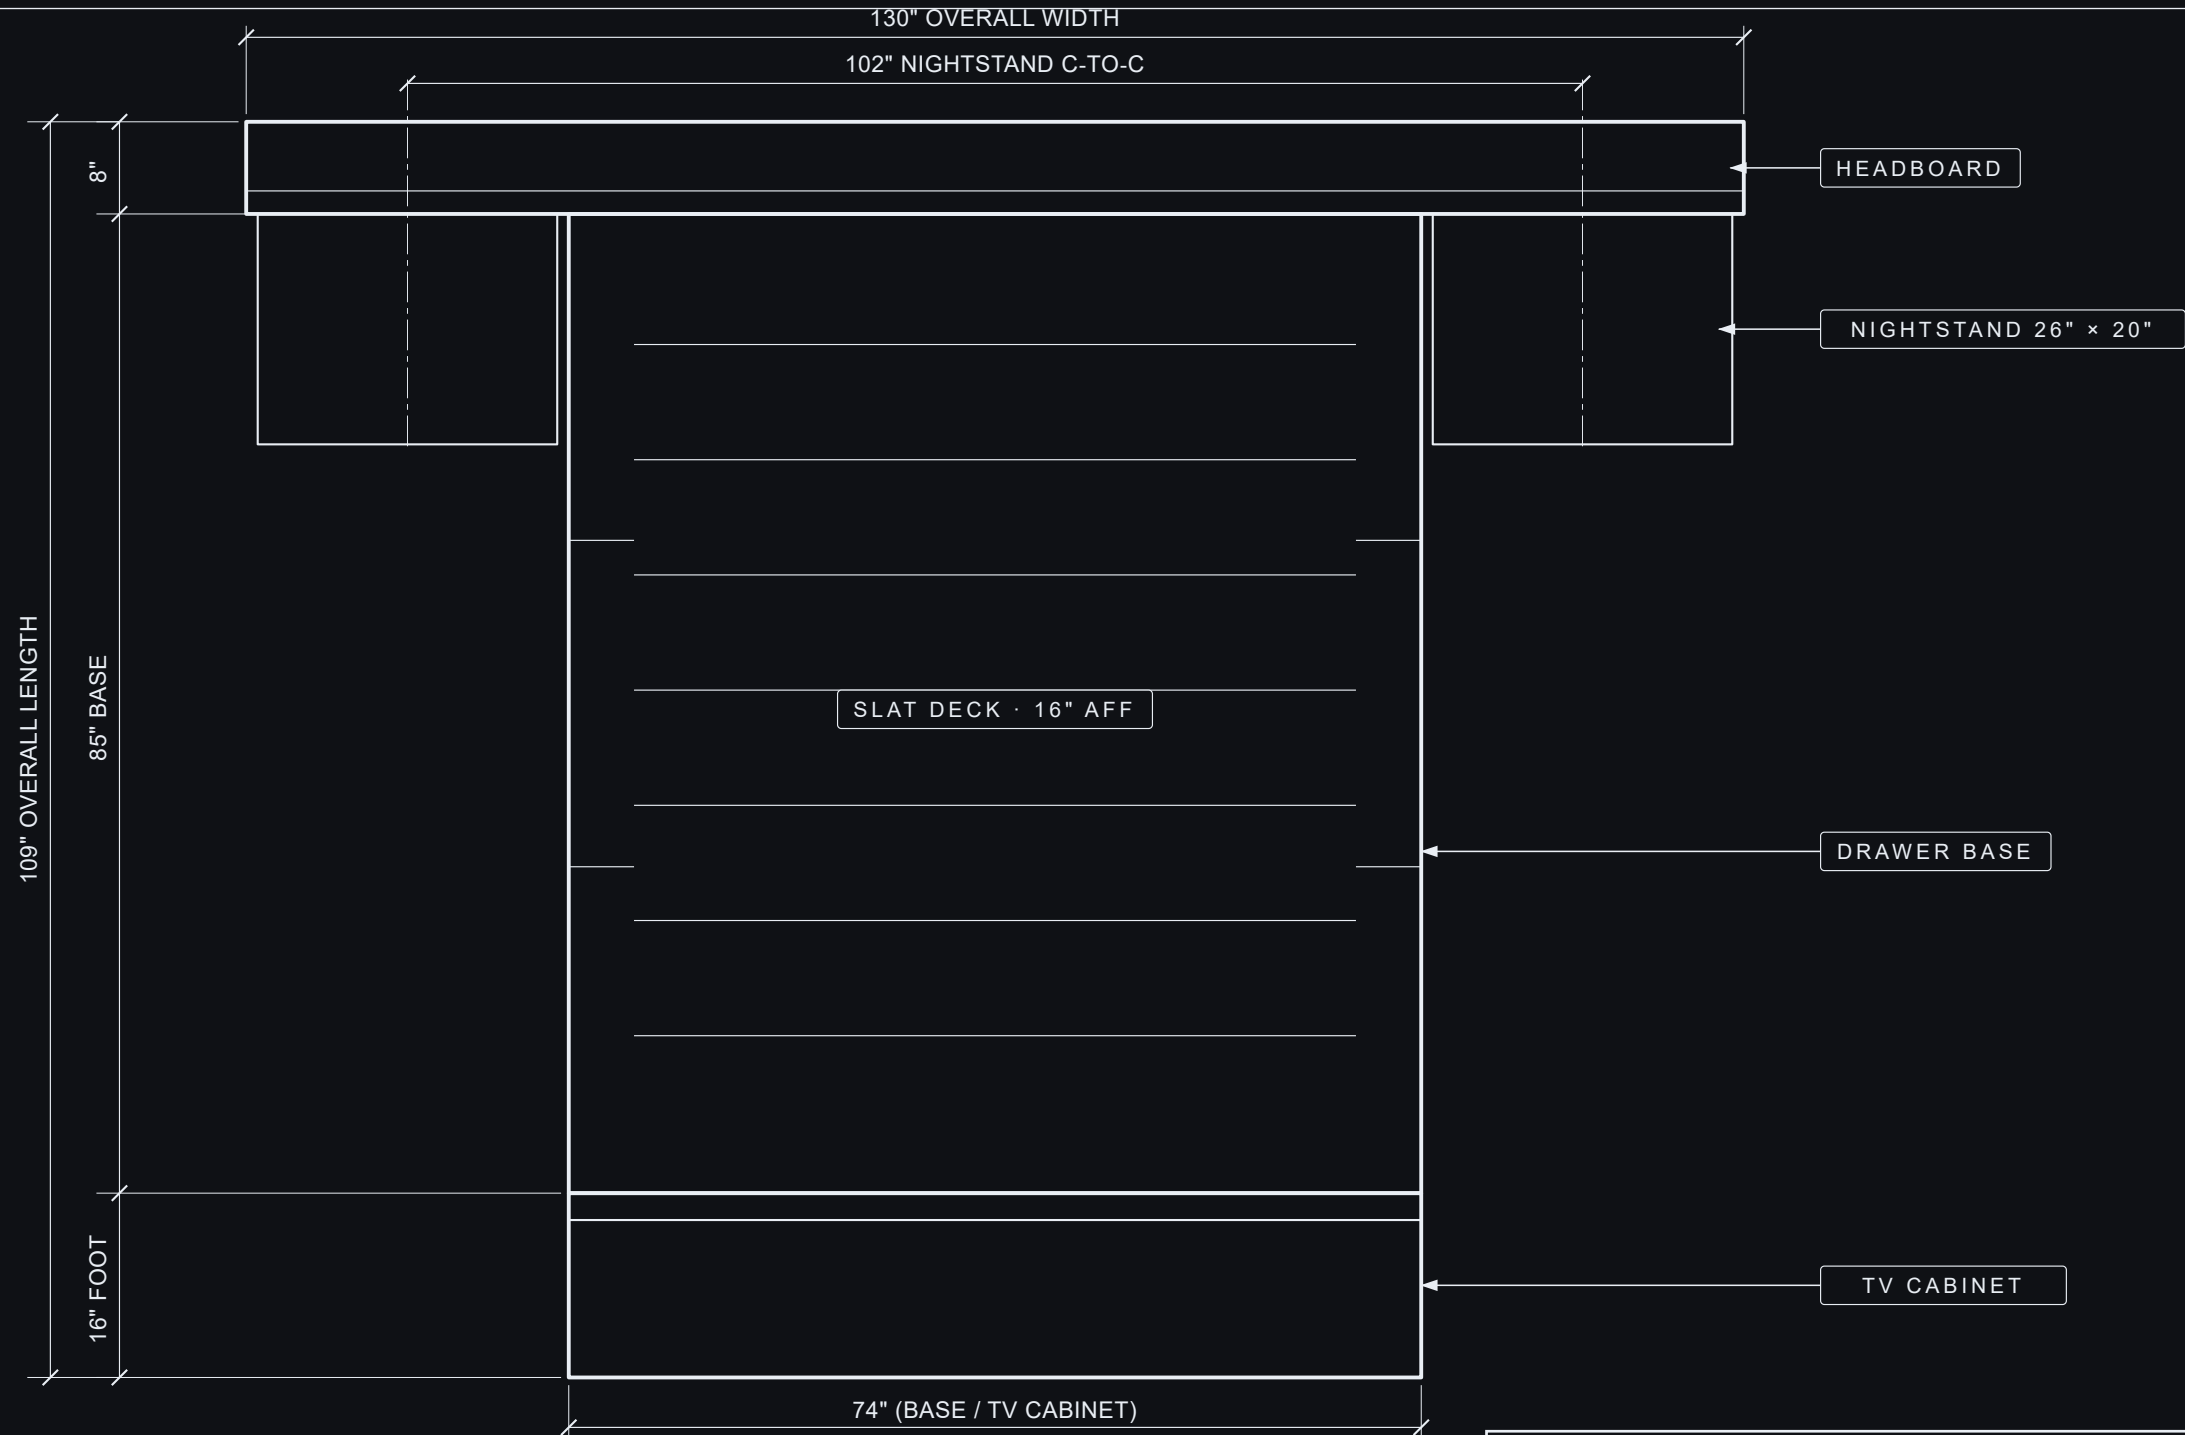

TOP VIEW

PROJECT HEIRLOOM BED	
LAST UPDATE 2026-06-11 17:31	DRAWING NO. Bed-Top_Blueprint
REV 3.0	SHEET 1 OF 1