
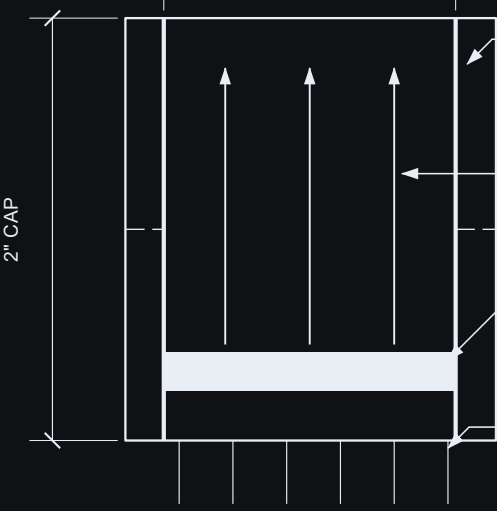


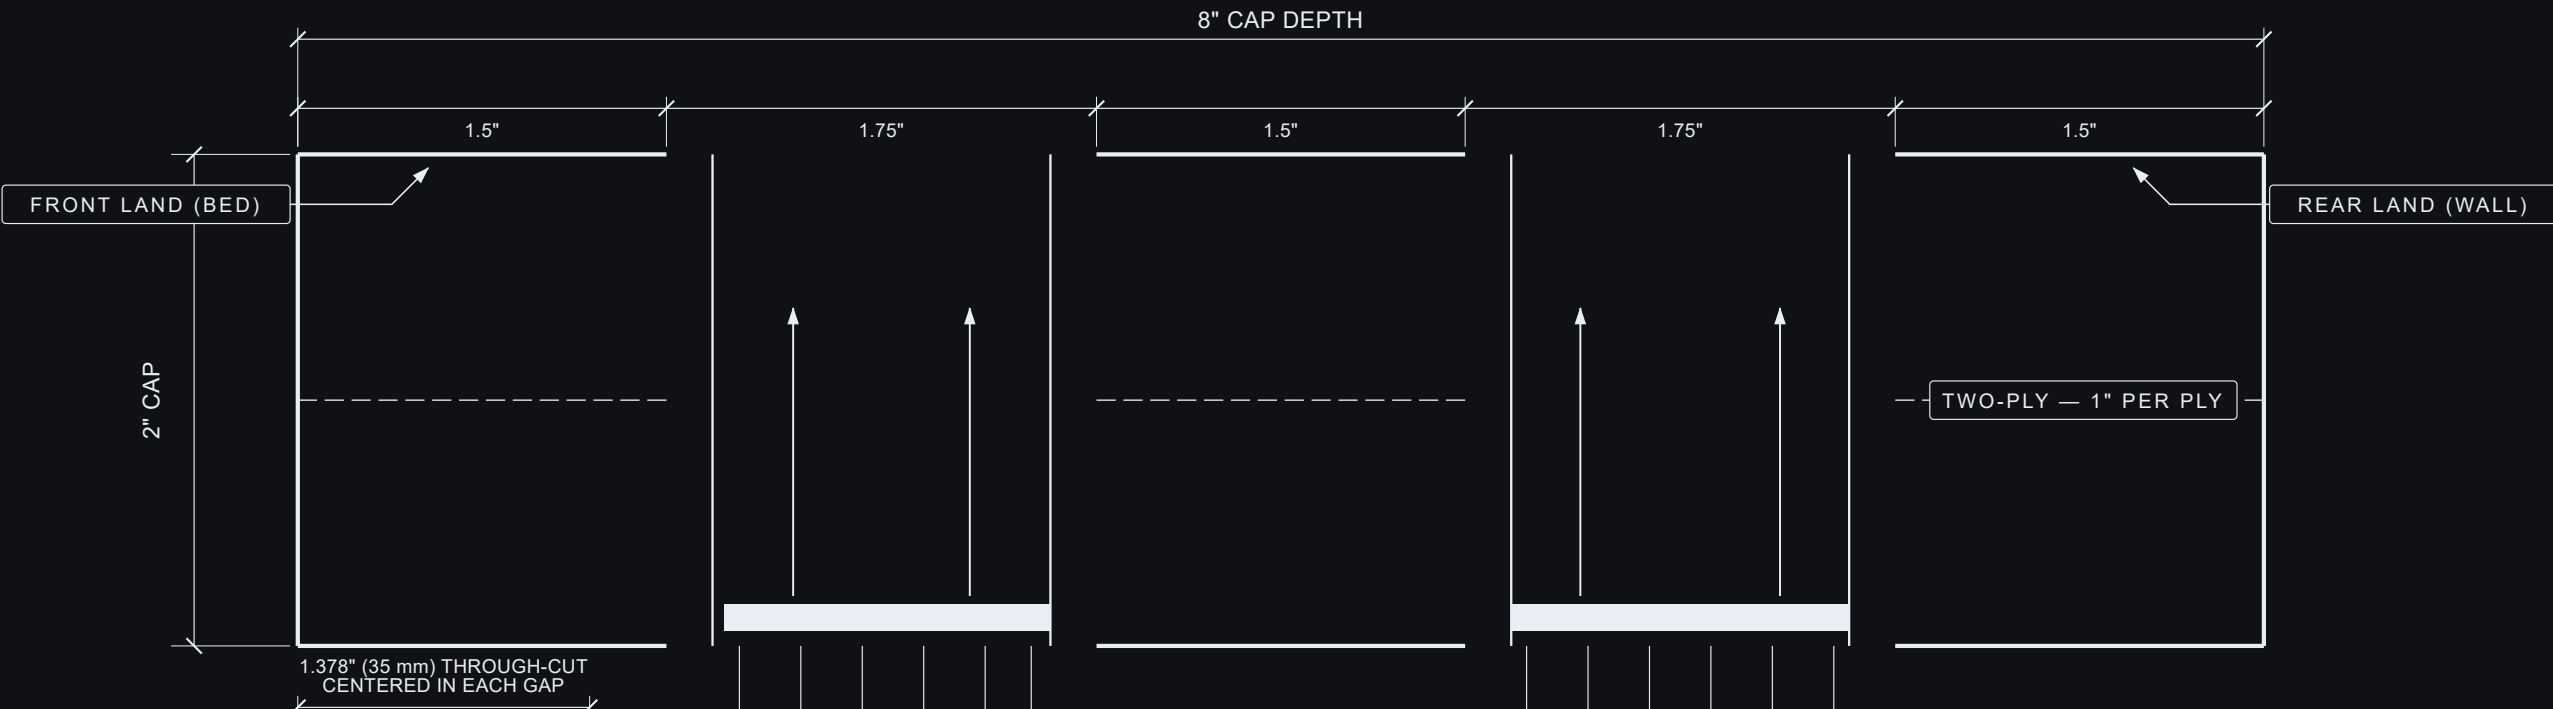

PROJECT HEIRLOOM BED	
LAST UPDATE 2026-06-11 17:31	DRAWING NO. TopCap-LED_Blueprint
REV 1.11	SHEET 1 OF 1