





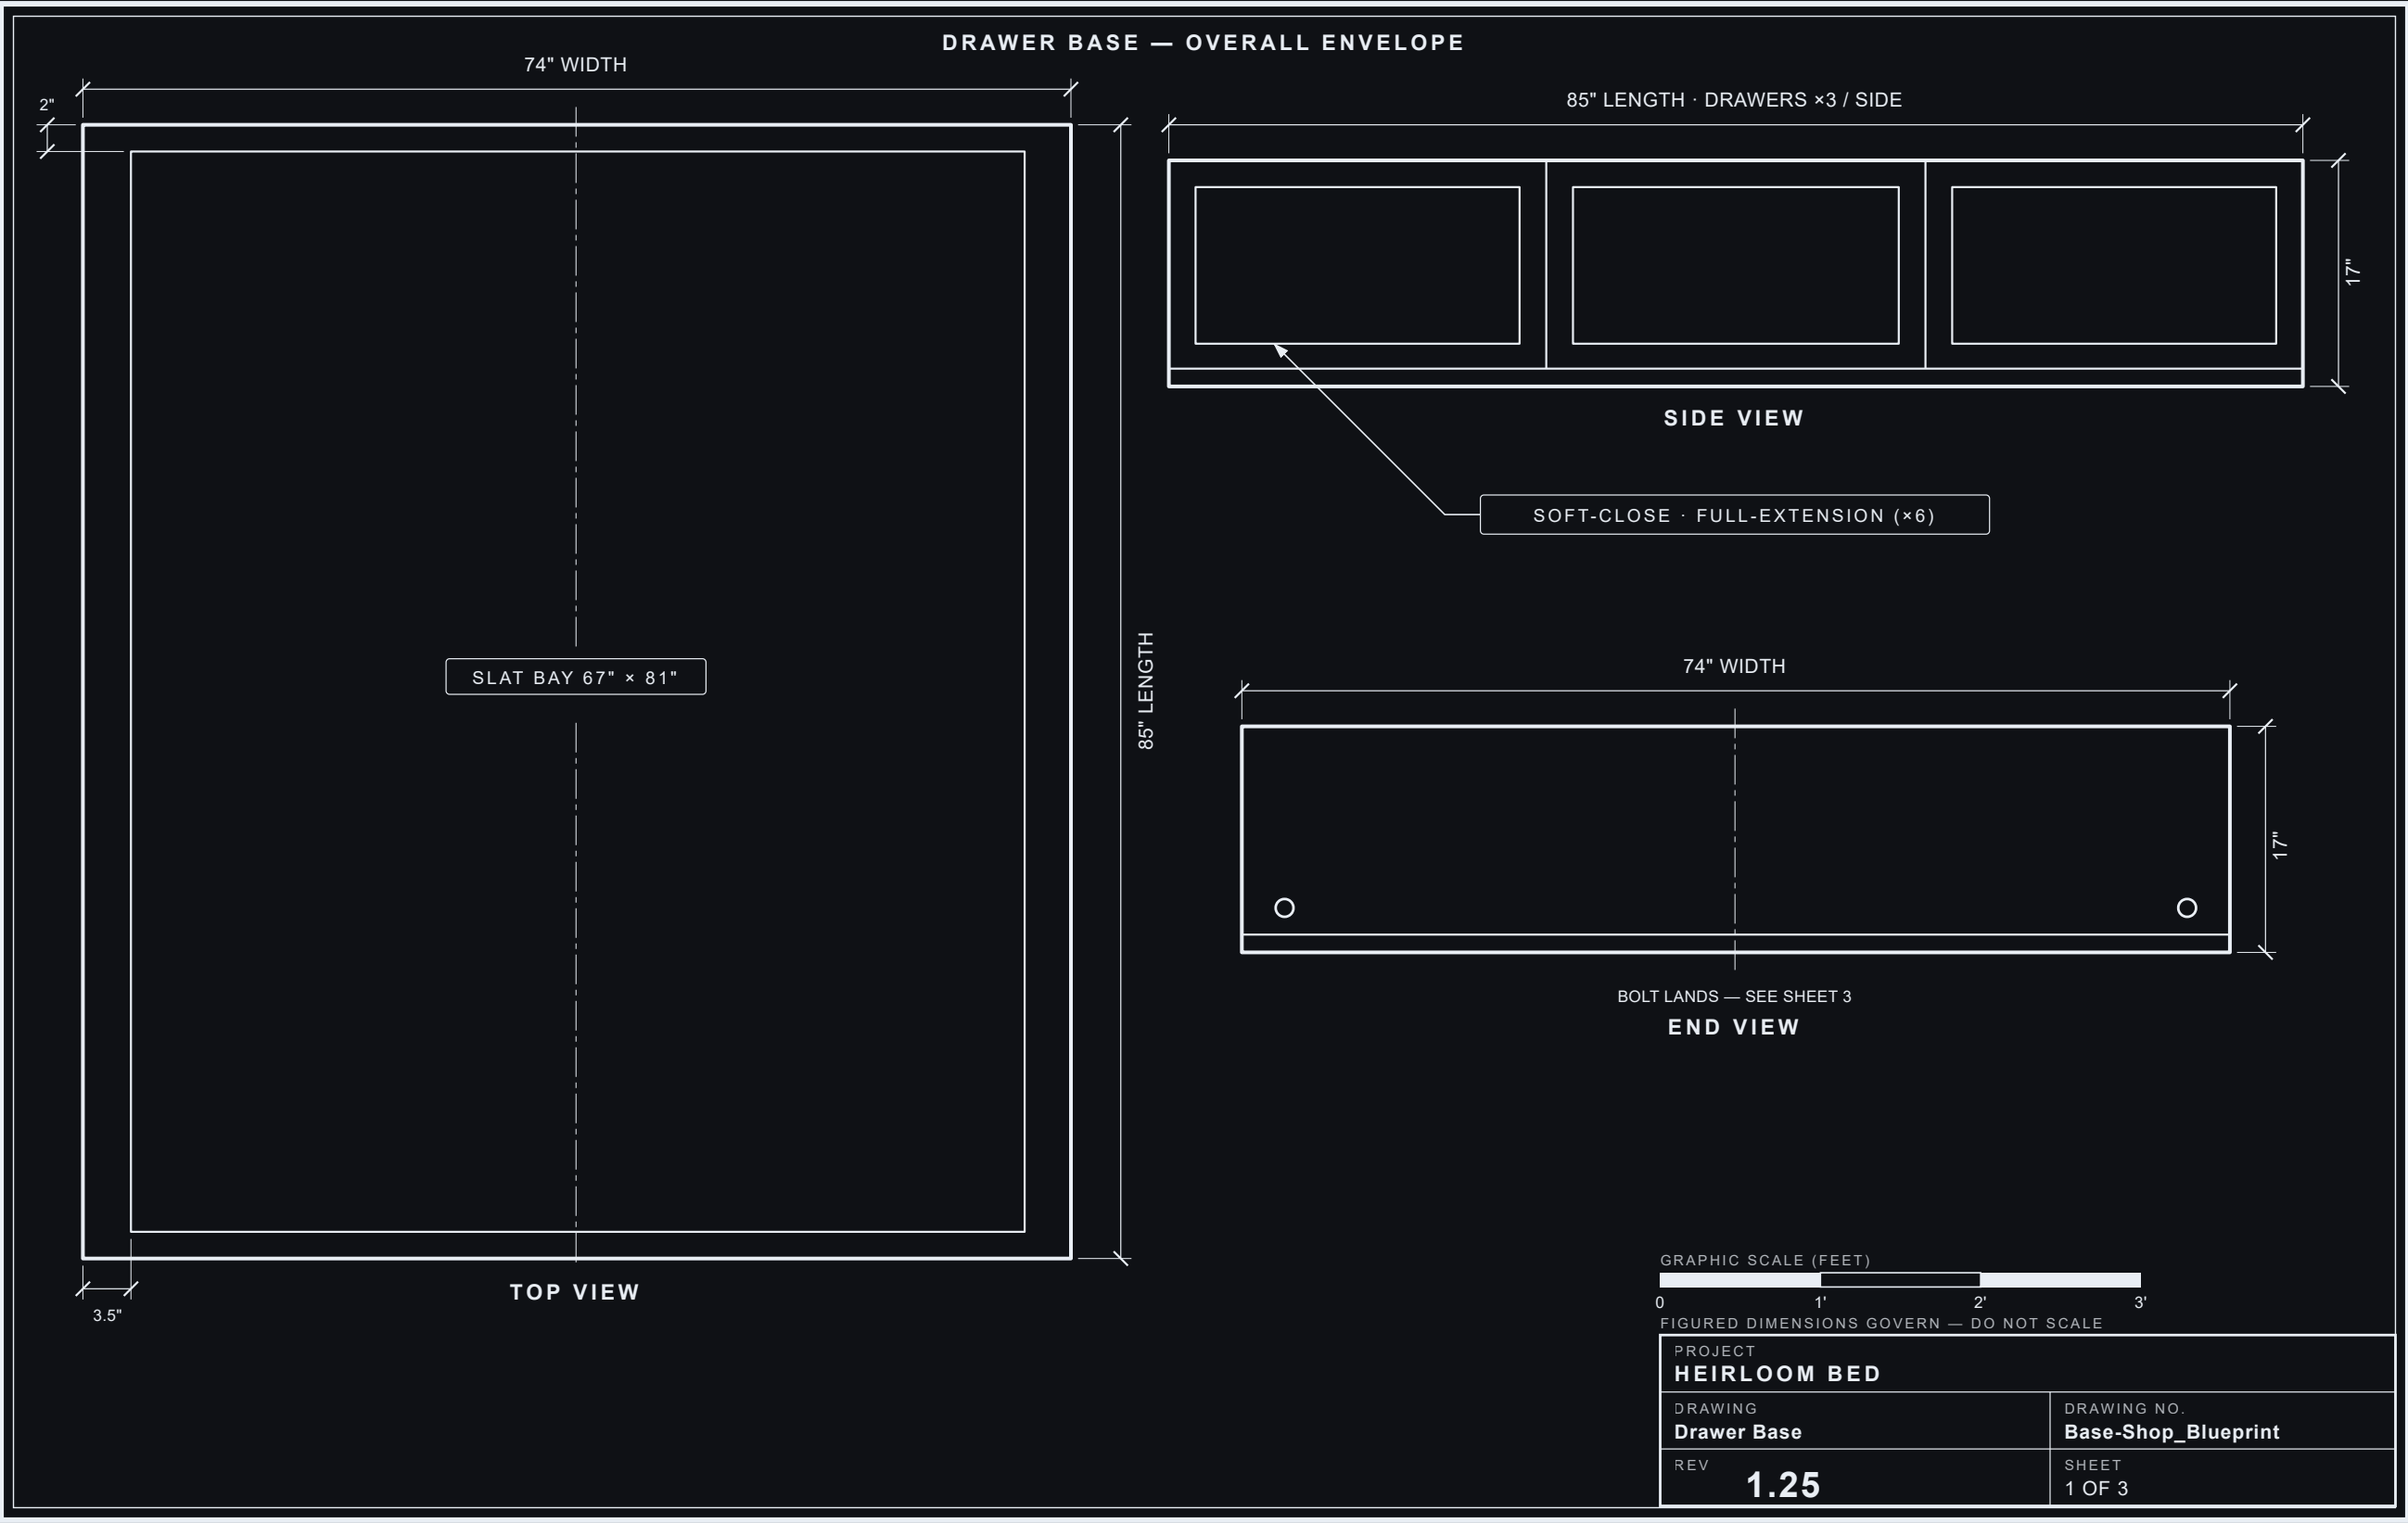


SECTION A-A · TRANSVERSE (ACROSS THE WIDTH)

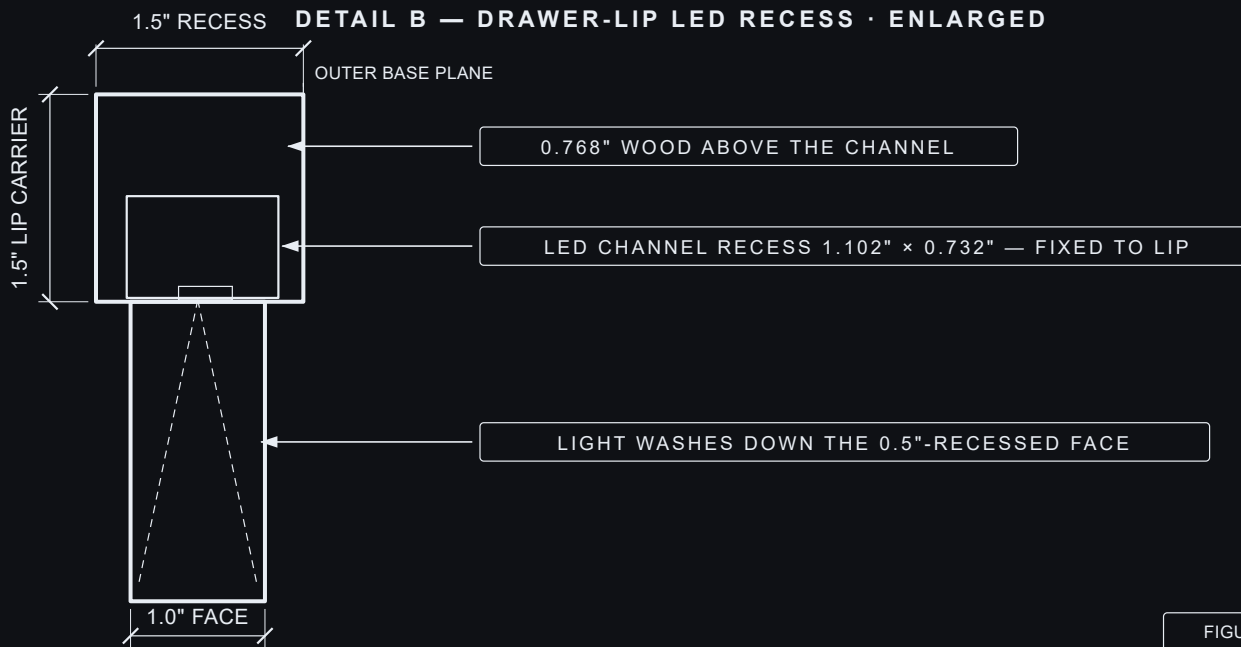

PROJECT HEIRLOOM BED	
DRAWING Drawer Base	DRAWING NO. Base-Shop_Blueprint
REV 1.25	SHEET 2 OF 3

CRITICAL INTERFACES — BASE BOLT LANDS

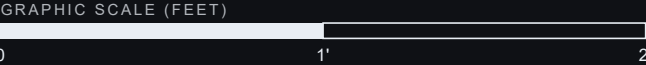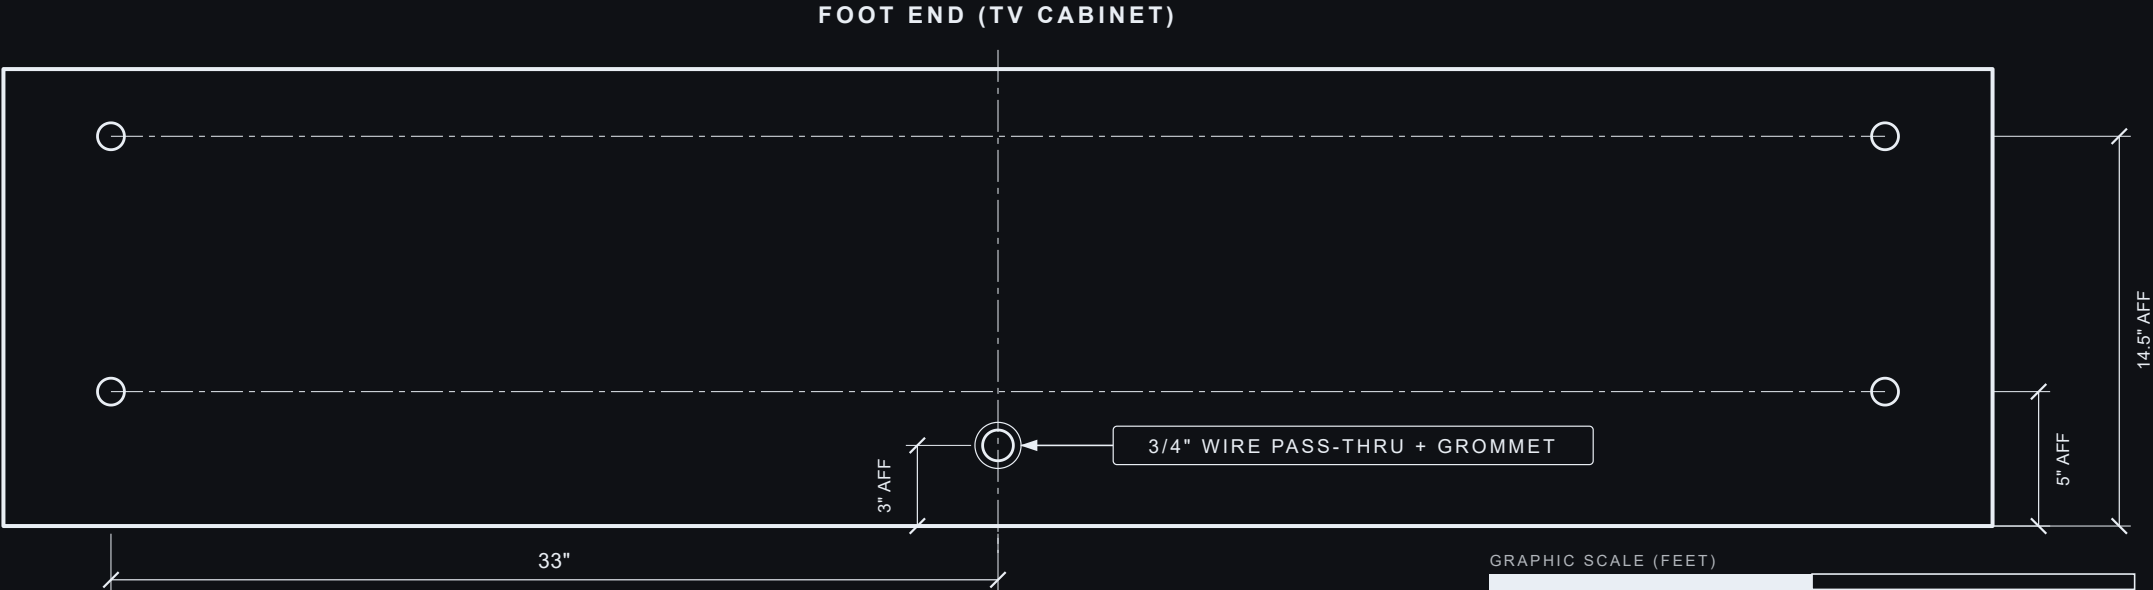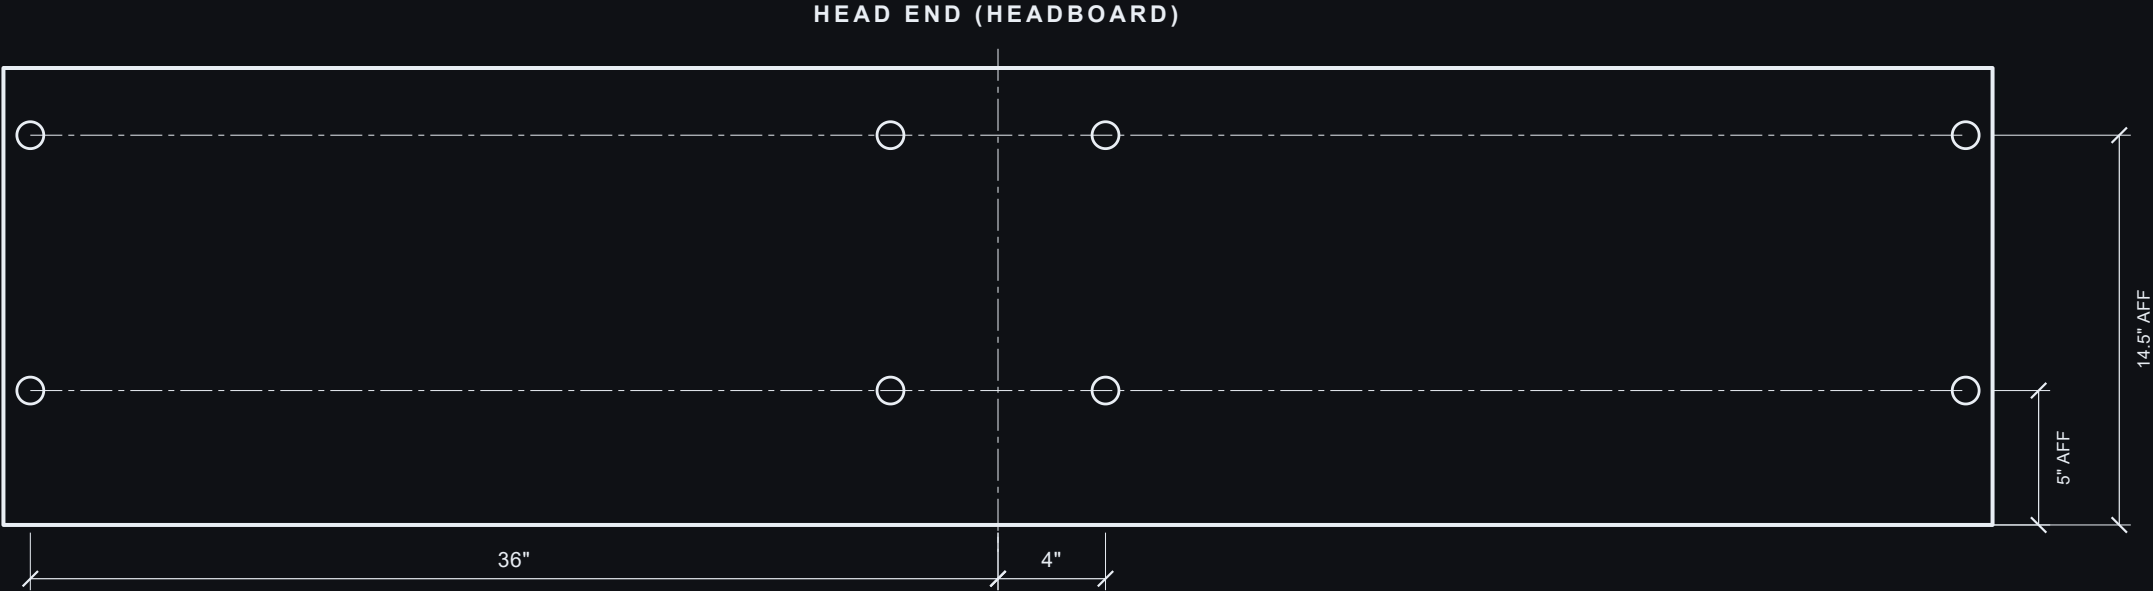

FIGURED DIMENSIONS GOVERN — DO NOT SCALE

PROJECT HEIRLOOM BED	
DRAWING Drawer Base	DRAWING NO. Base-Shop_Blueprint
REV 1.25	SHEET 3 OF 3