


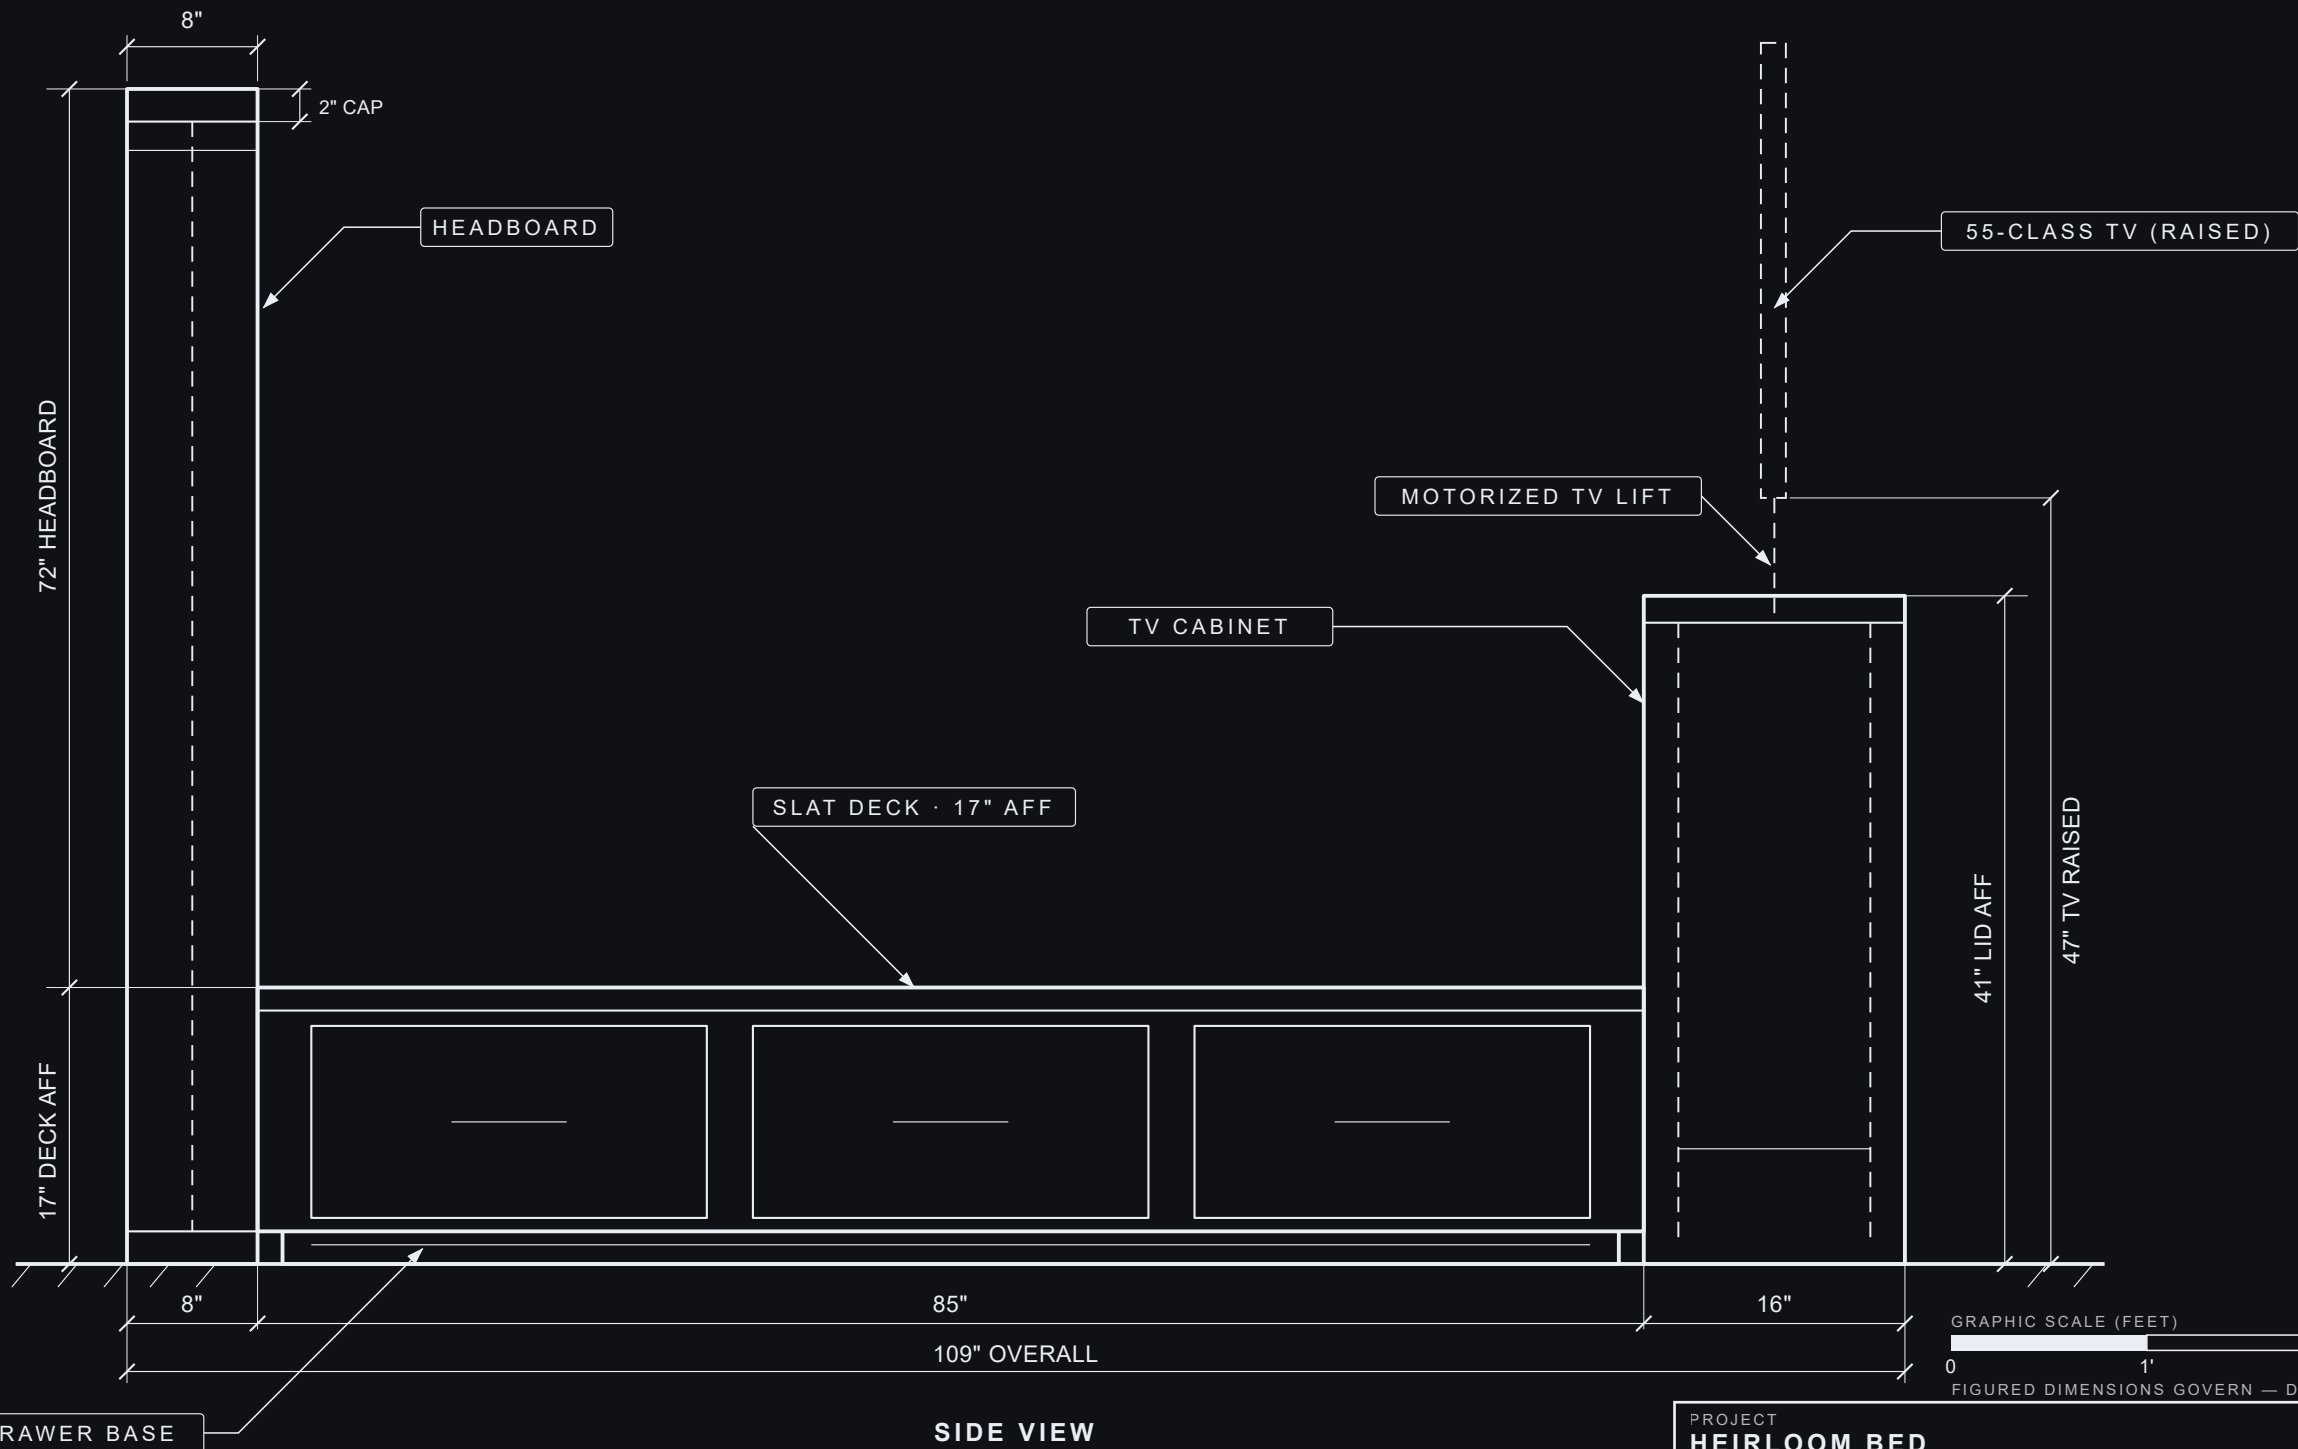

SIDE VIEW

PROJECT HEIRLOOM BED	
DRAWING Side view	DRAWING NO. Bed-Side_Blueprint
REV 1.13	SHEET 1 OF 1