


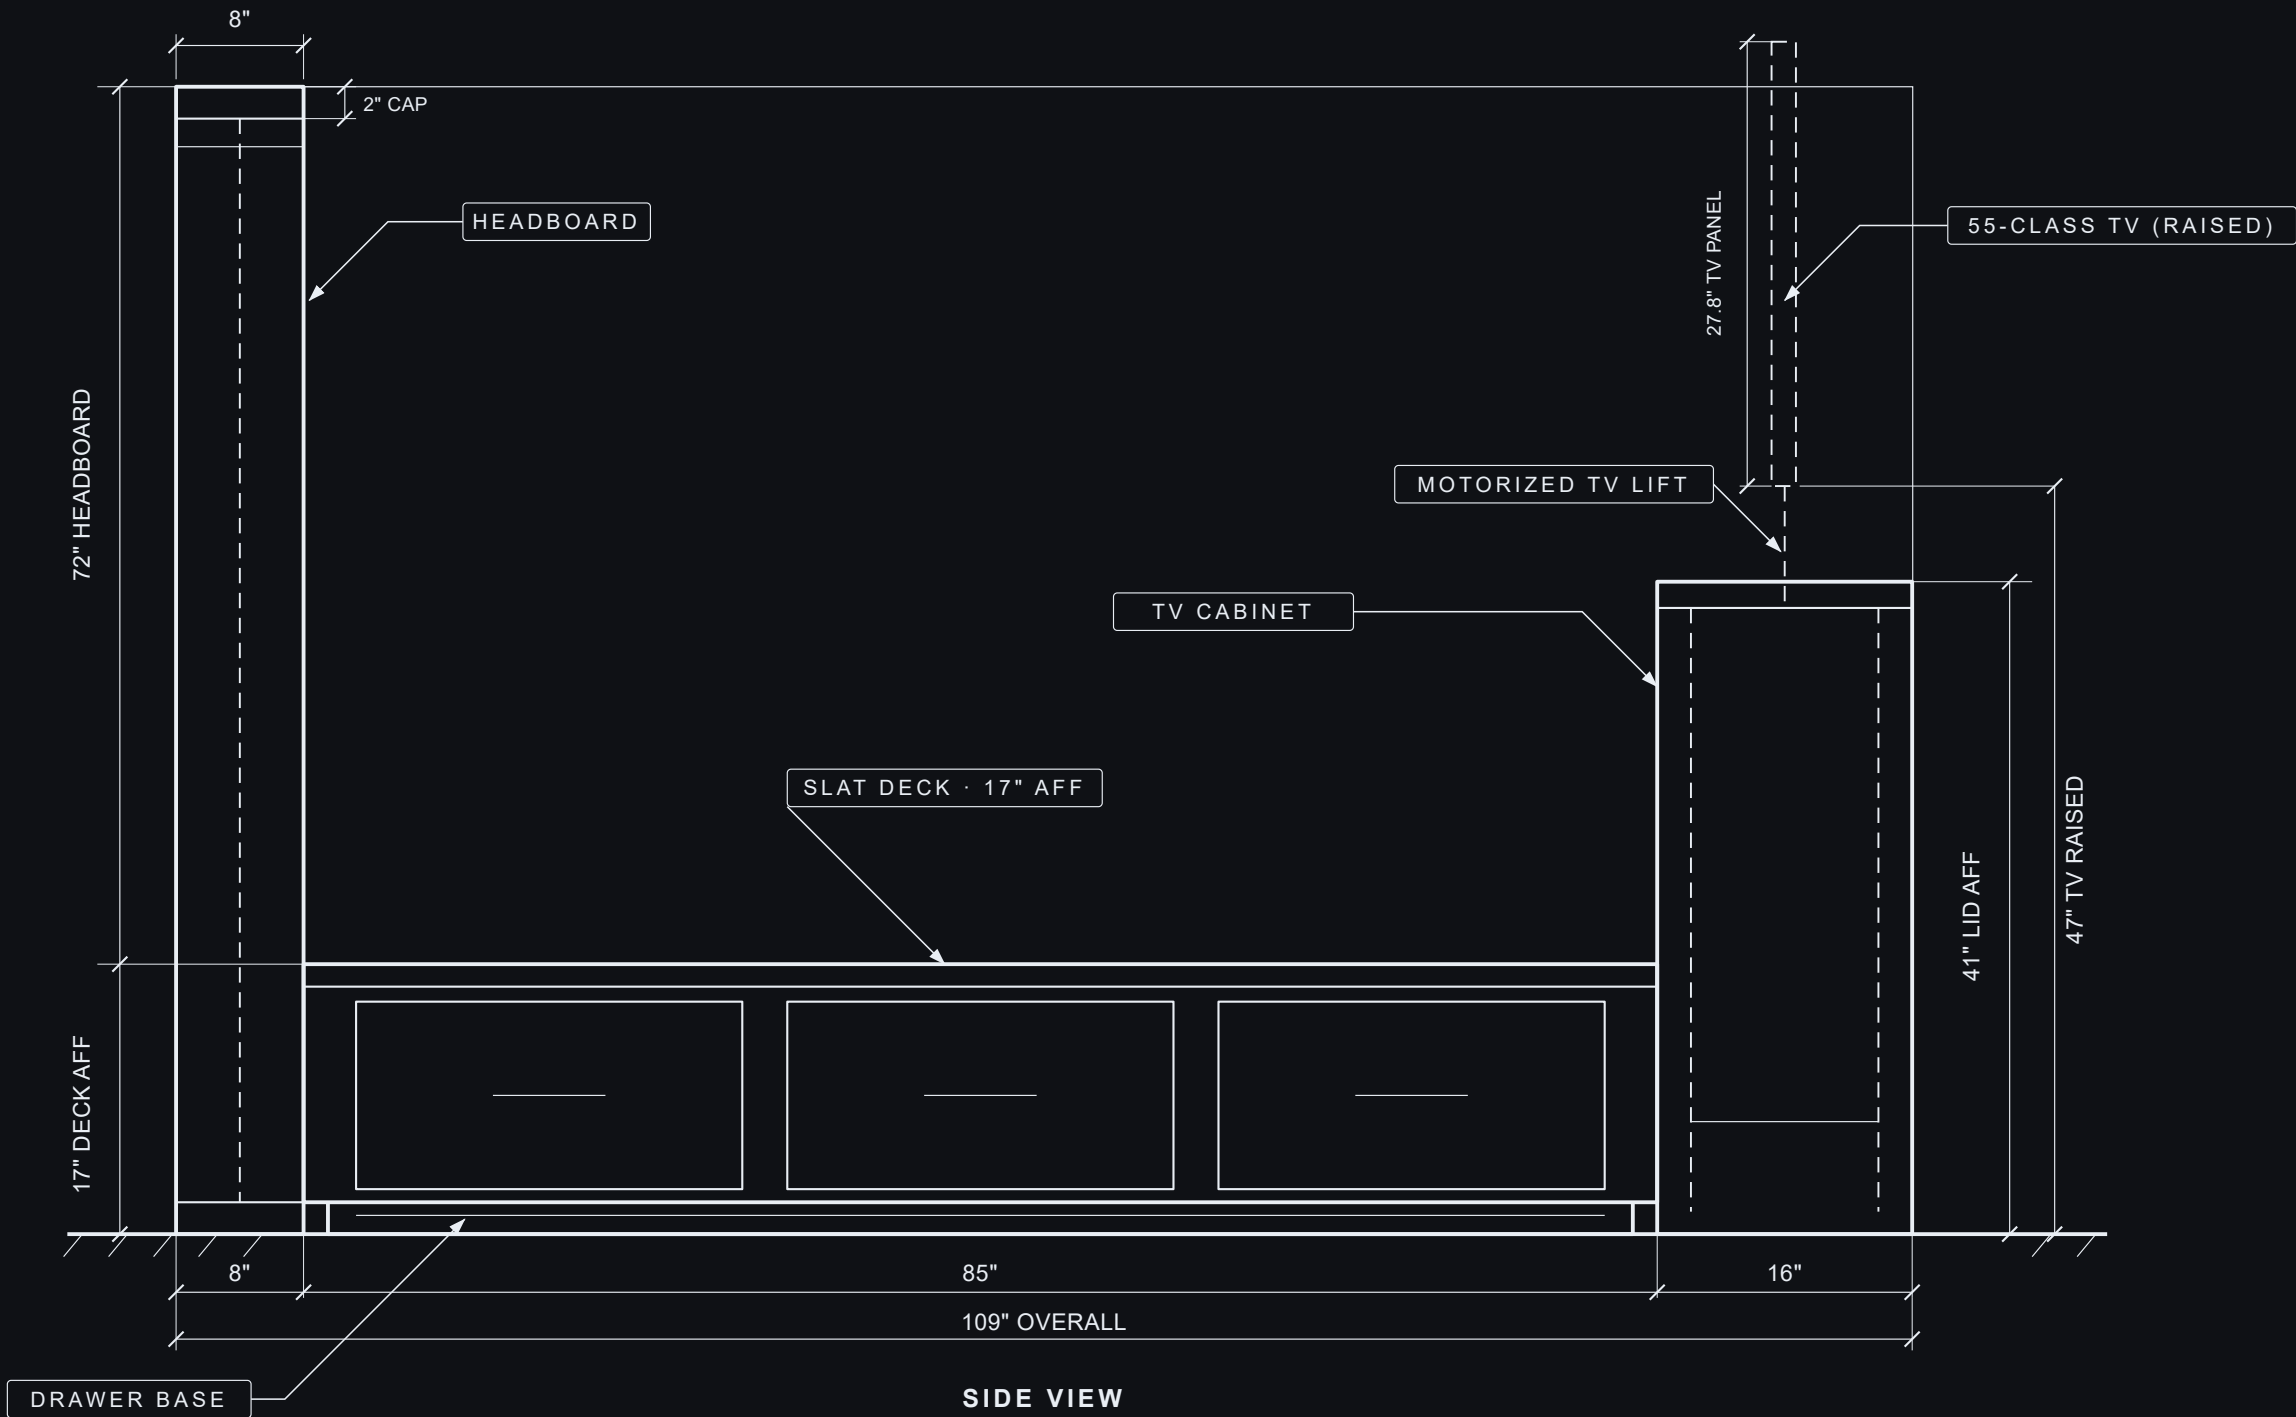

PROJECT	HEIRLOOM BED	SHEET 1 OF 1
DRAWING NO.	Bed-Side_Blueprint	
LAST UPDATE	2026-06-12 12:33 AM	REV 1.20