


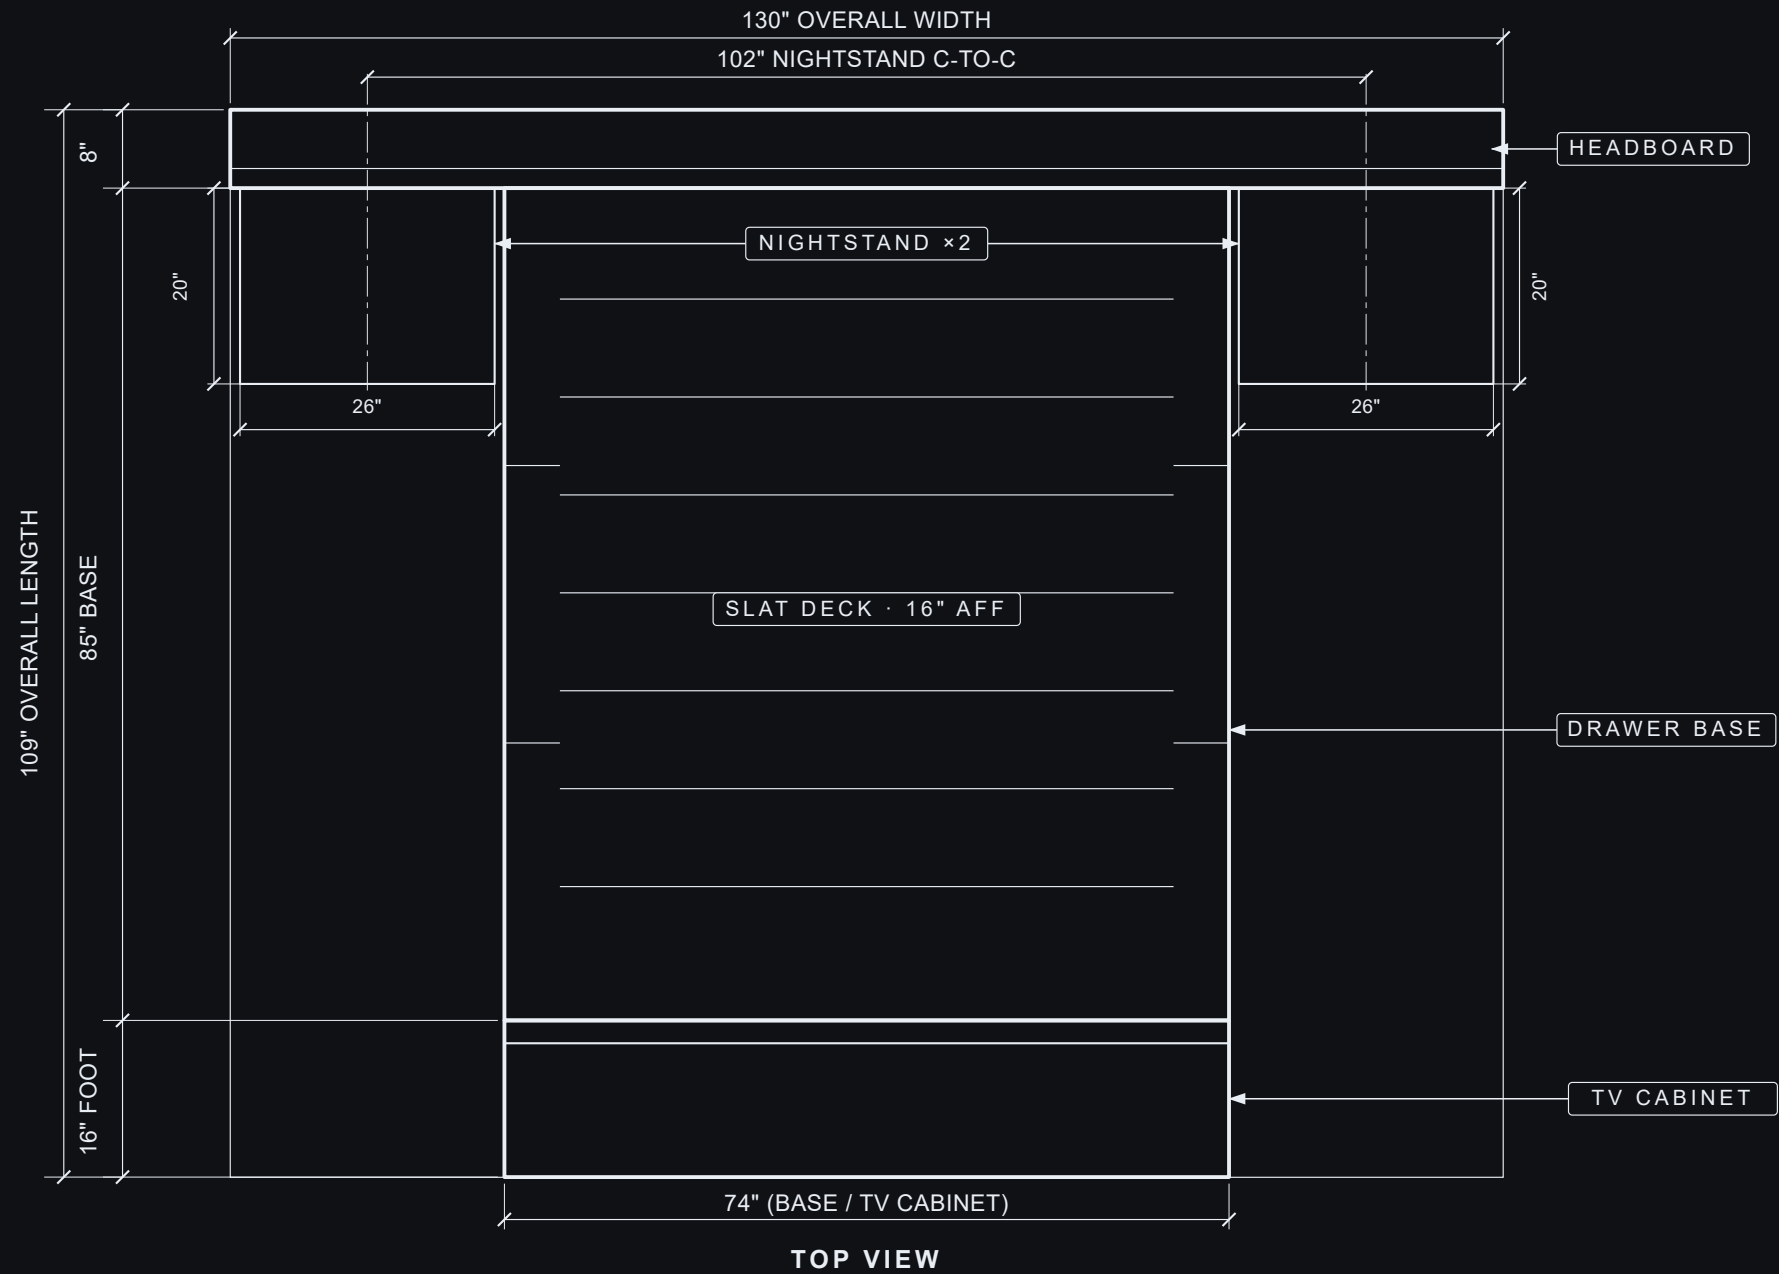

PROJECT	HEIRLOOM BED	SHEET 1 OF 1
DRAWING NO.	Bed-Top_Blueprint	
LAST UPDATE	2026-06-12 12:41 AM	REV 3.6