


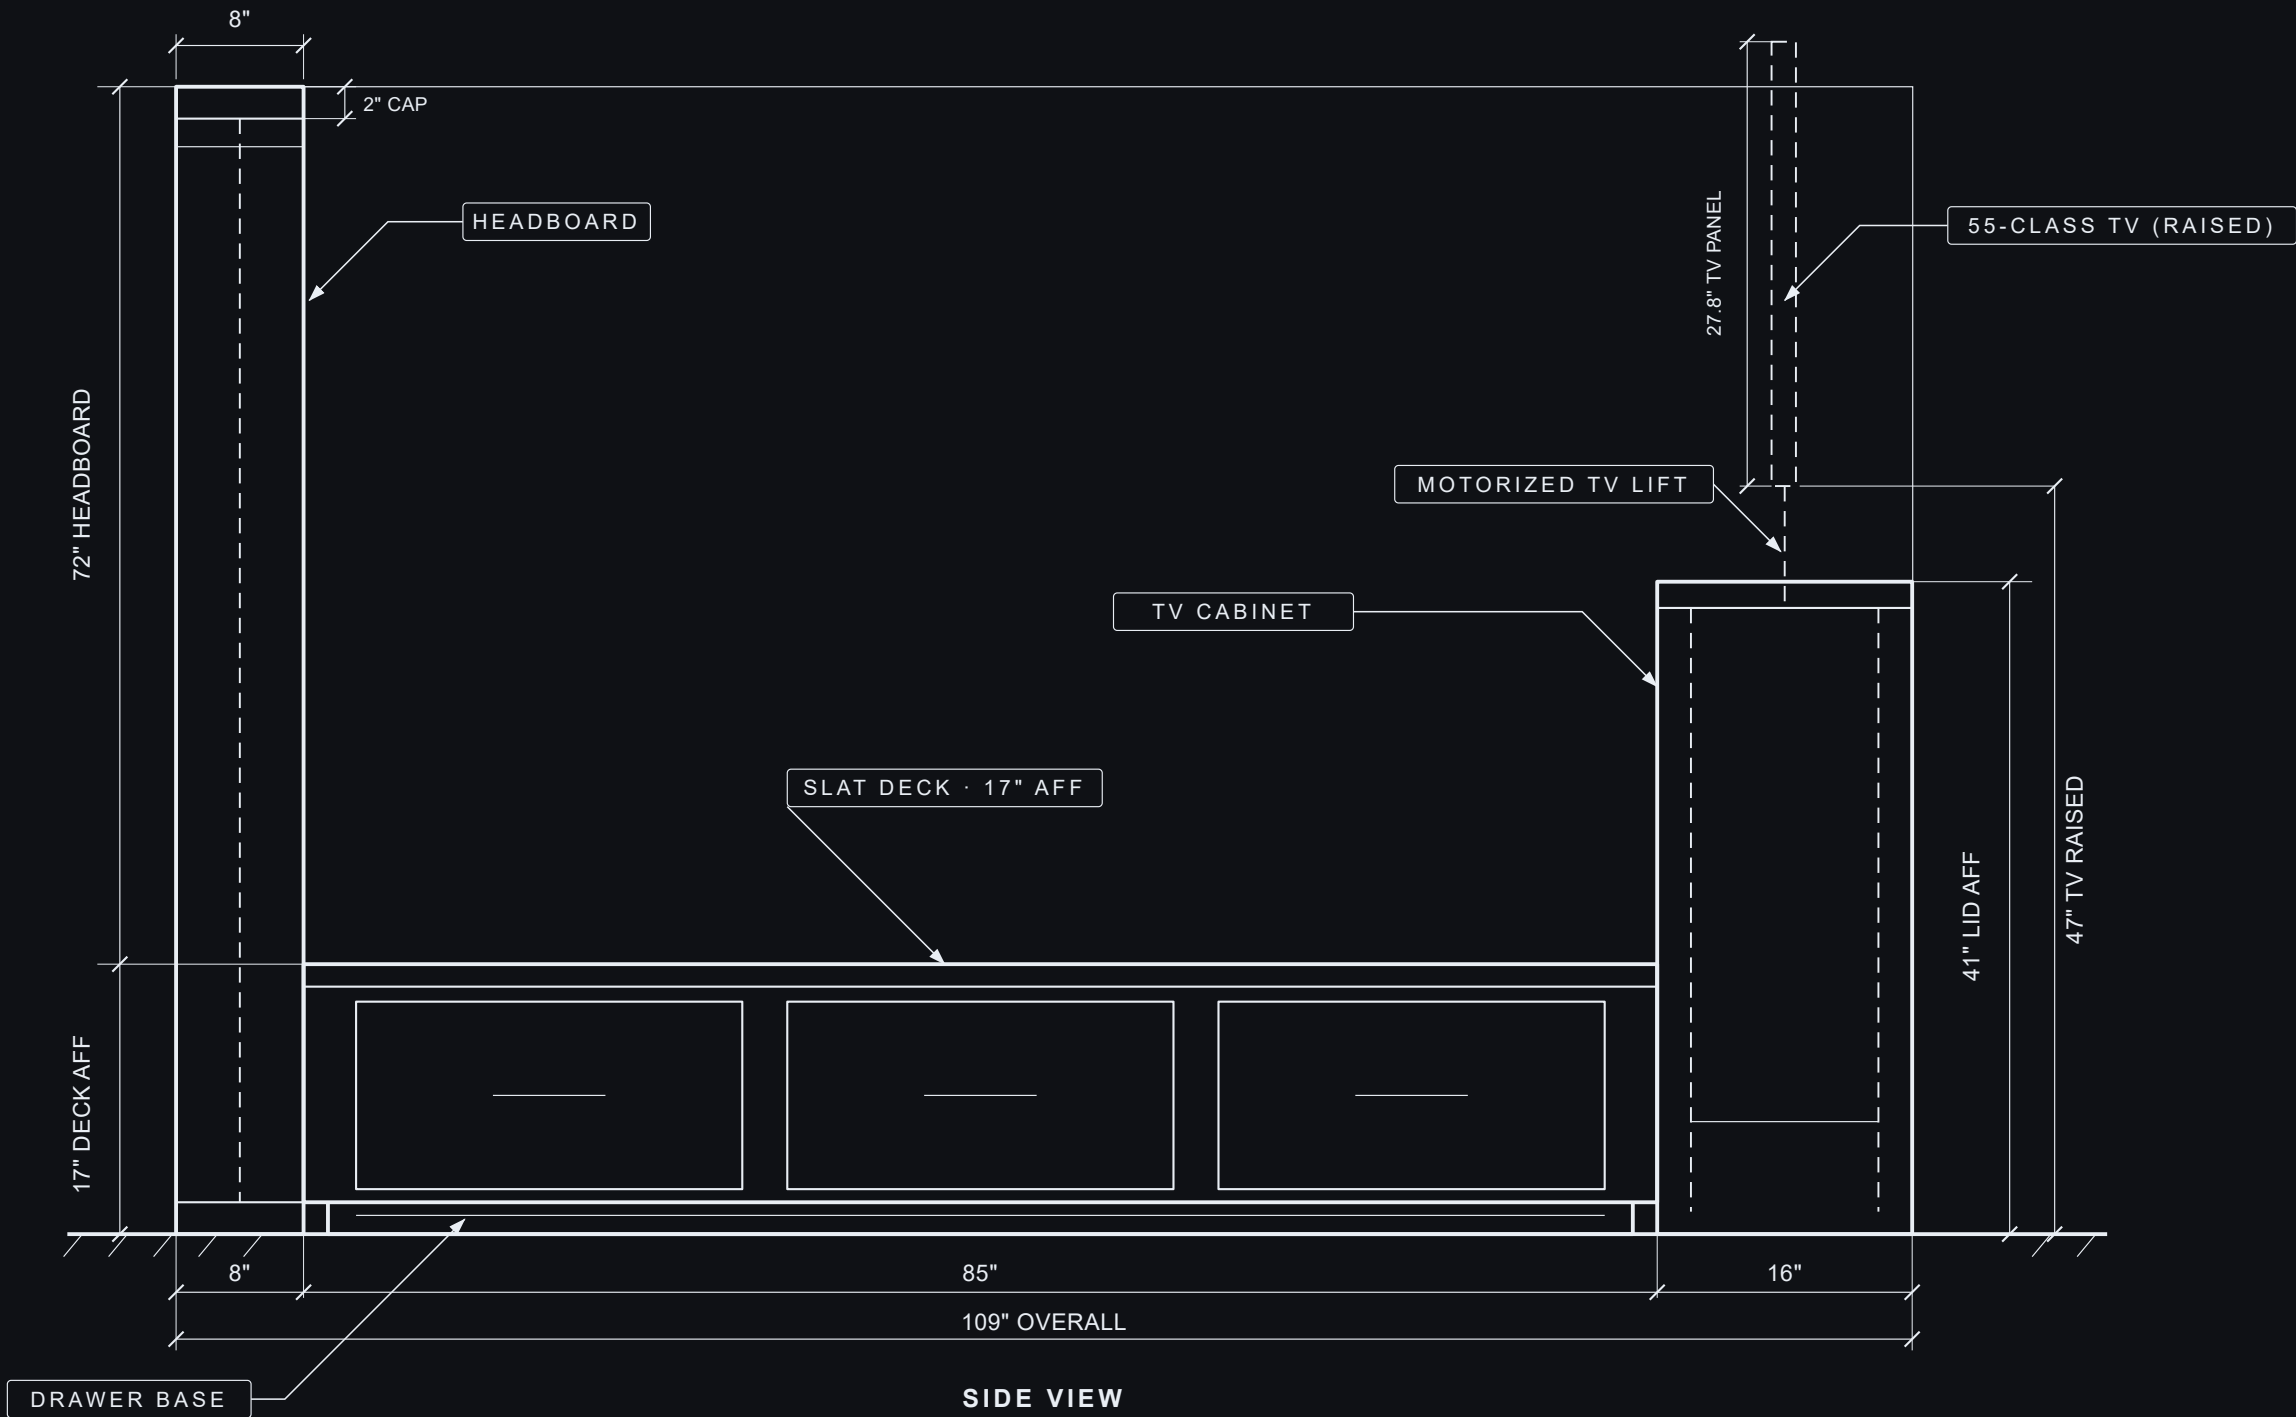

|             |                     |              |
|-------------|---------------------|--------------|
| PROJECT     | HEIRLOOM BED        | SHEET 1 OF 1 |
| DRAWING NO. | Bed-Side_Blueprint  |              |
| LAST UPDATE | 2026-06-19 11:39 AM | REV 1.21     |