


FRONT VIEW — WHOLE BED · TV CABINET REMOVED

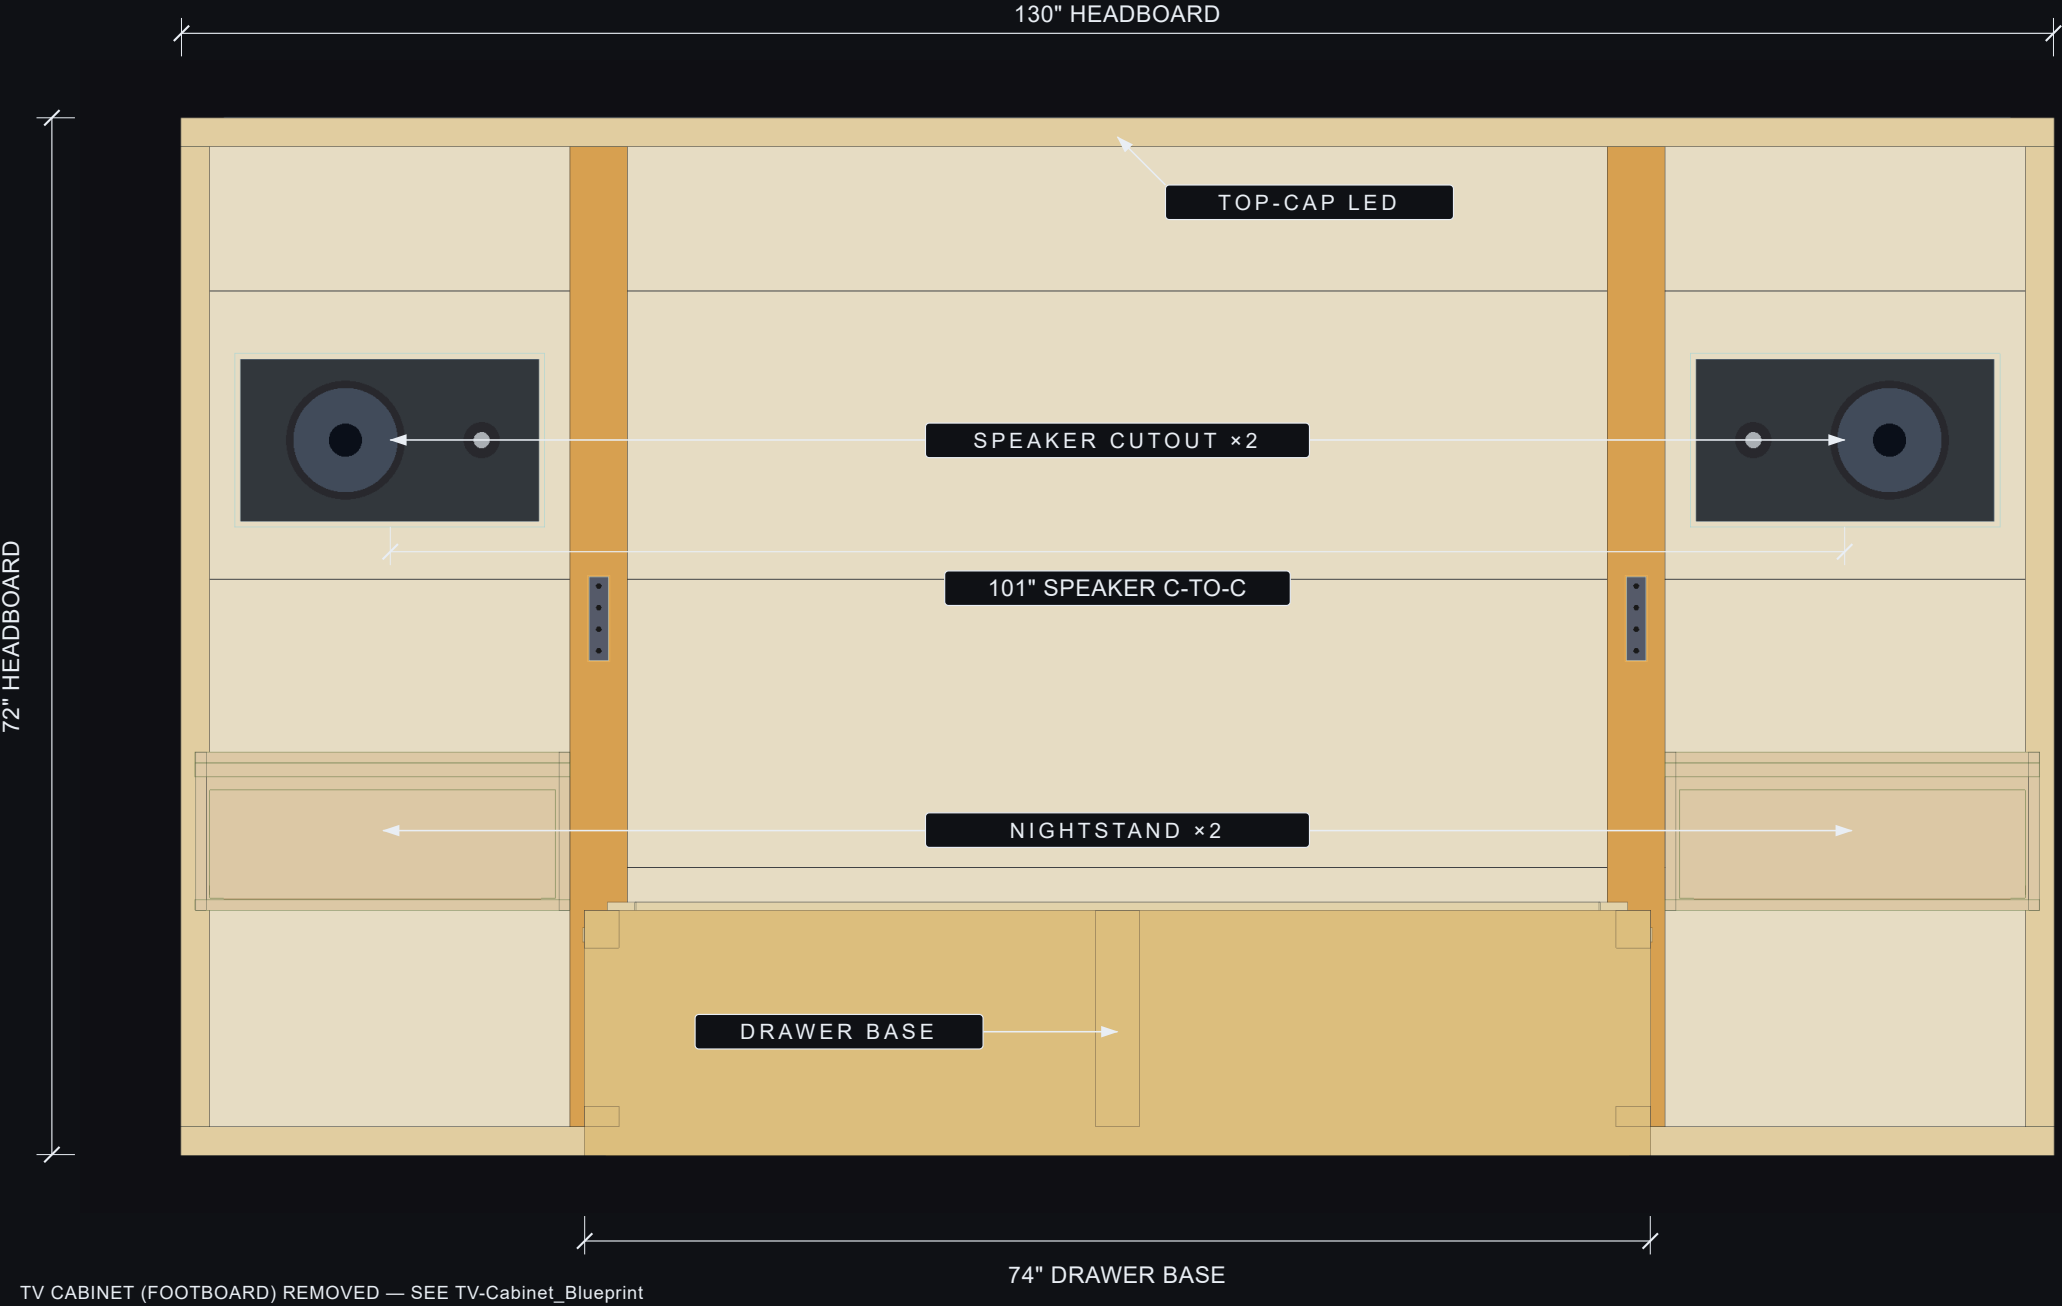

PROJECT	HEIRLOOM BED	SHEET 1 OF 1
DRAWING NO.	Bed-Front_Blueprint	
LAST UPDATE	2026-06-20 9:10 AM	REV 4.10