

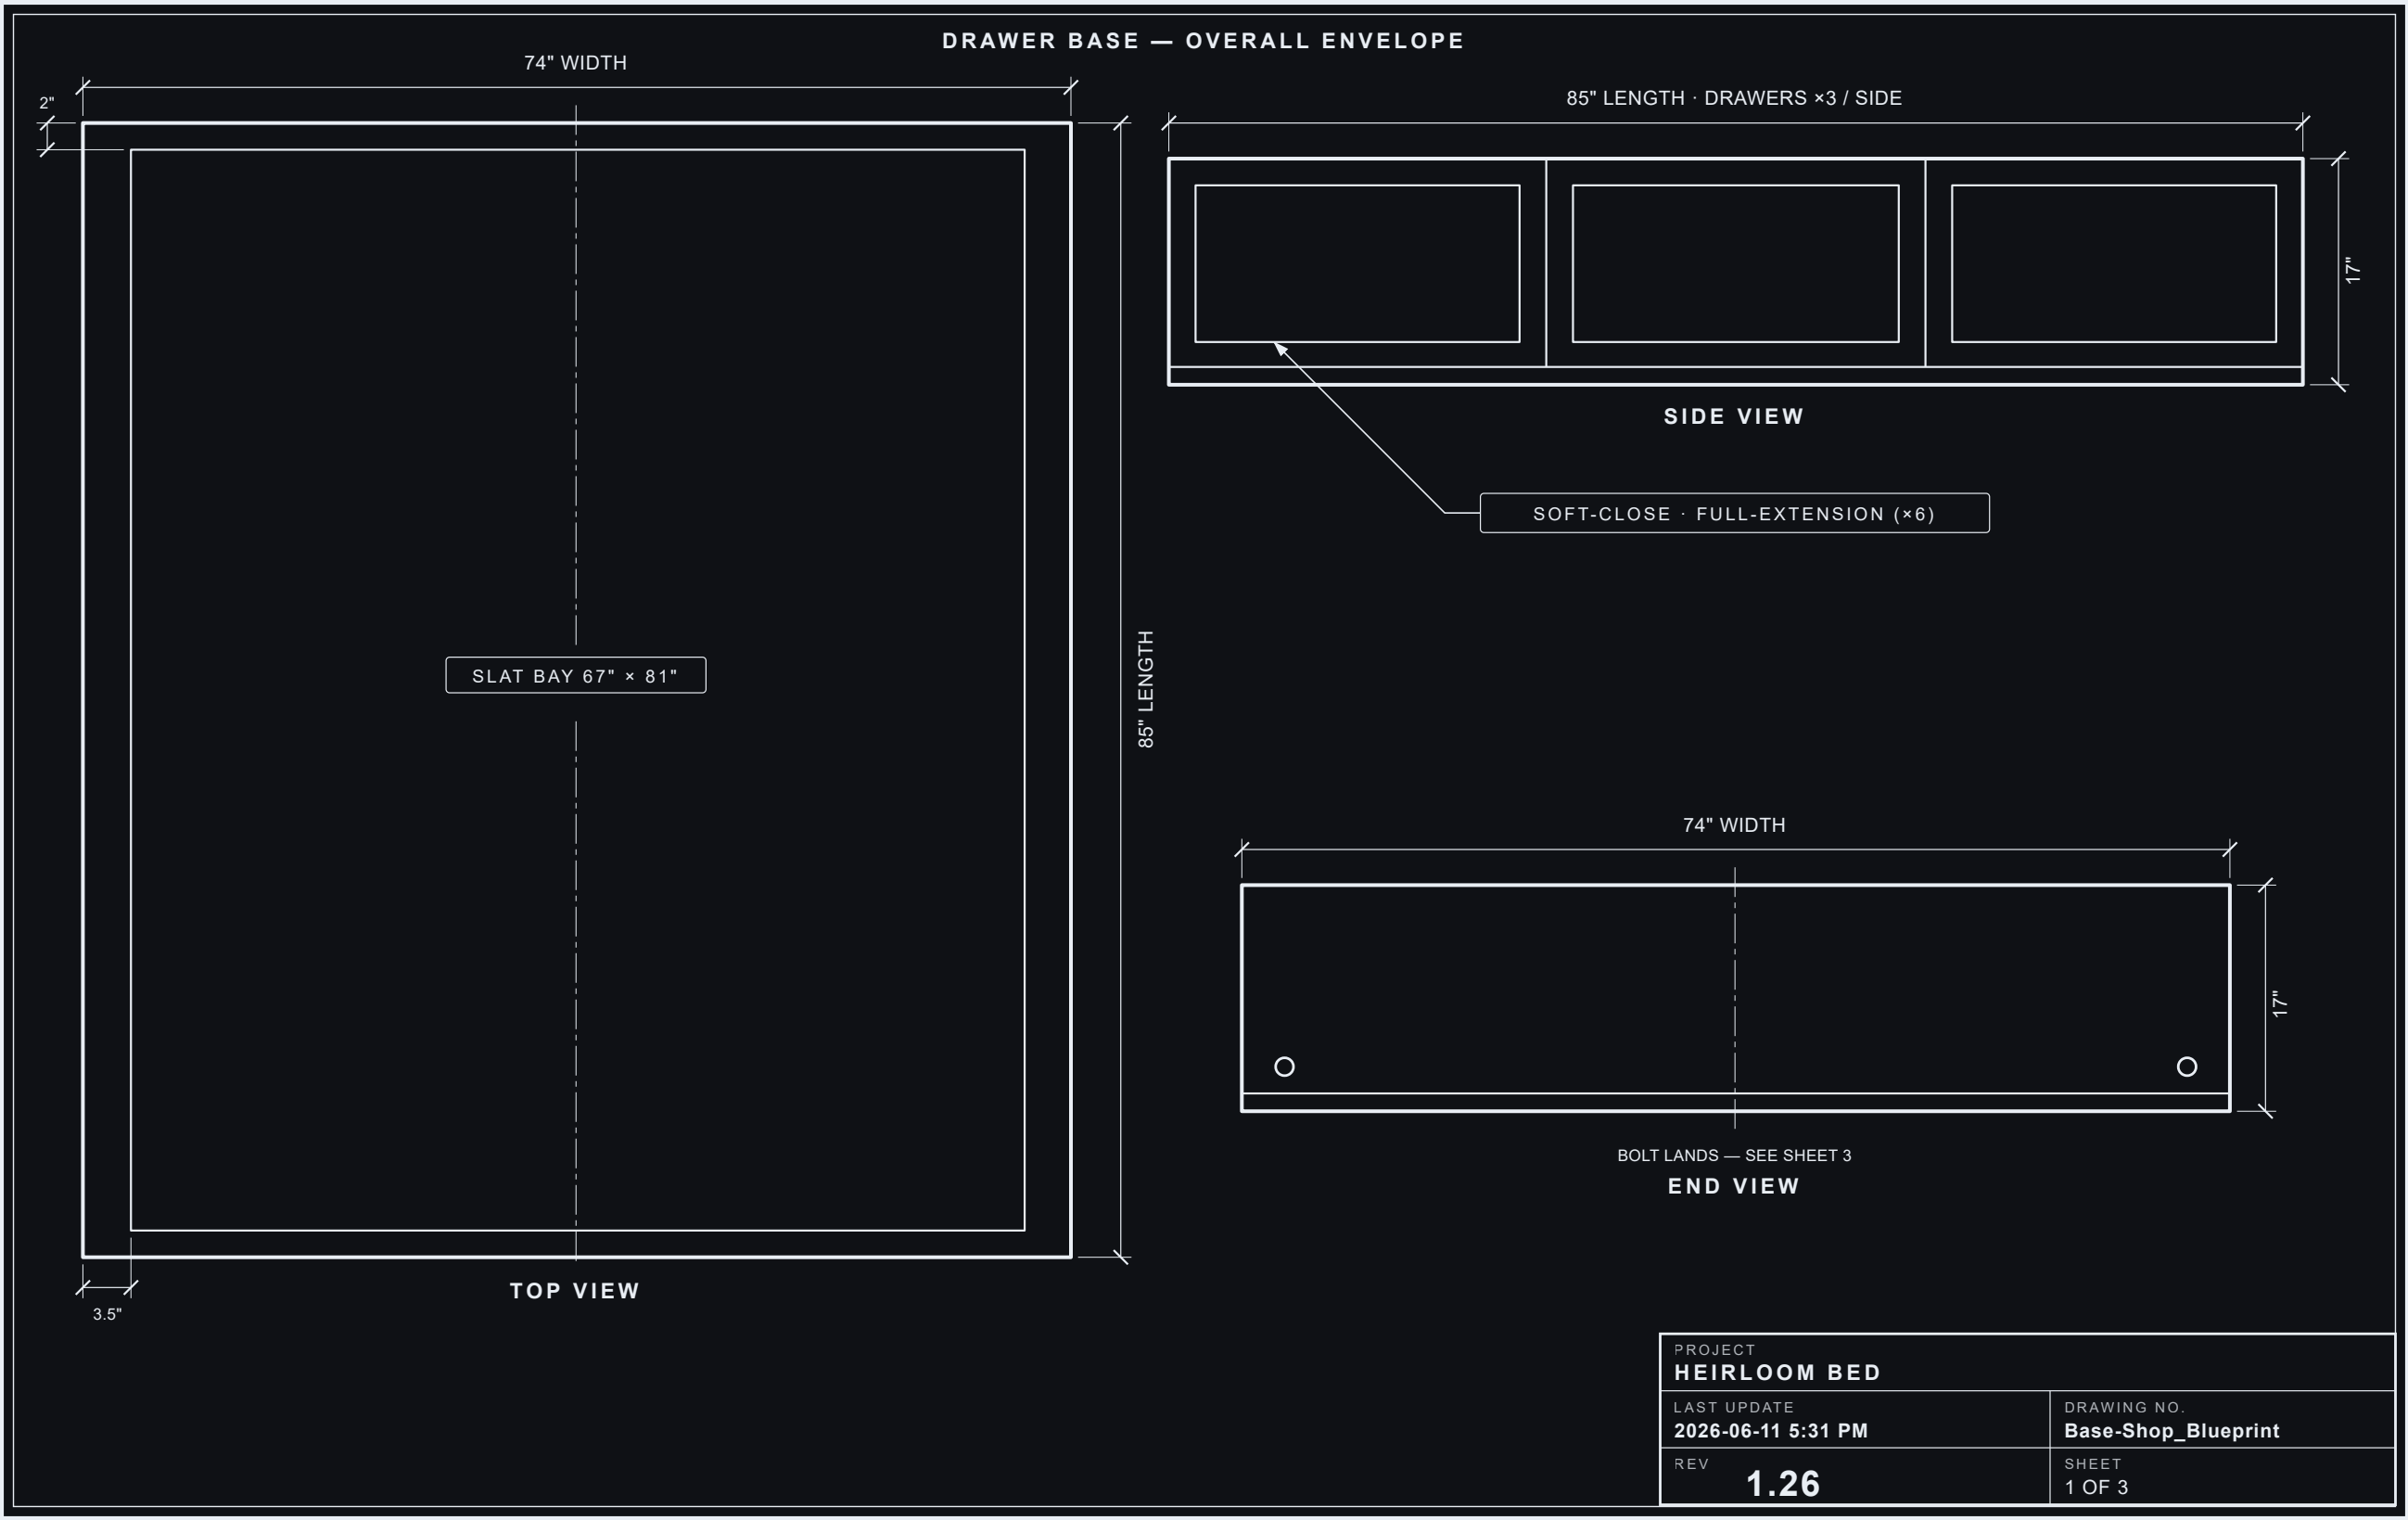


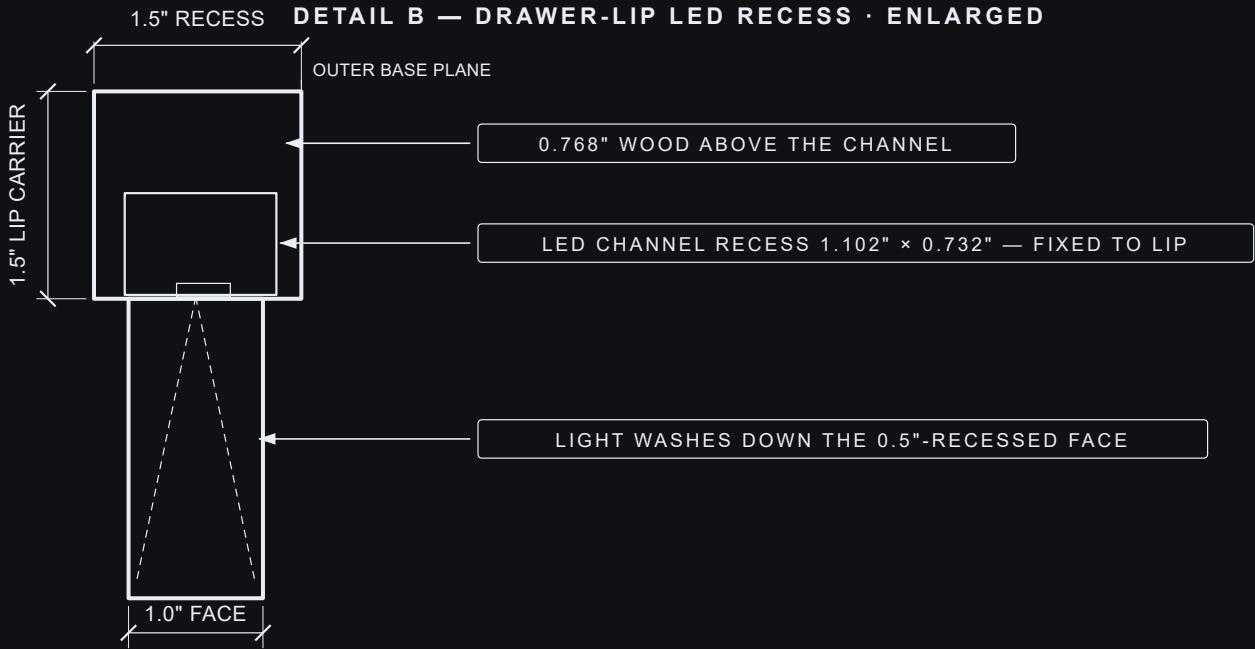

SECTION DETAILS


SECTION A-A · TRANSVERSE (ACROSS THE WIDTH)

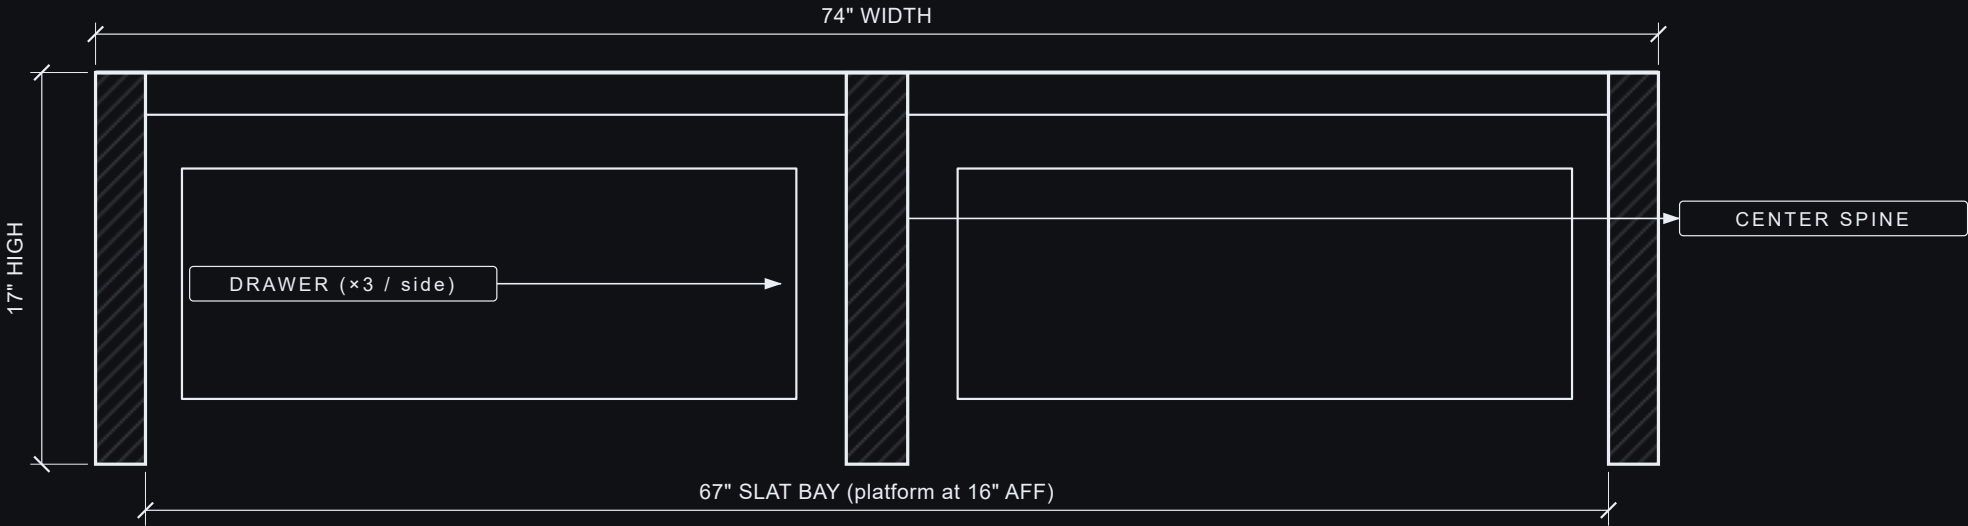


PROJECT HEIRLOOM BED	
LAST UPDATE 2026-06-11 5:31 PM	DRAWING NO. Base-Shop_Blueprint
REV 1.26	SHEET 2 OF 3

CRITICAL INTERFACES — BASE BOLT LANDS

HEAD END (HEADBOARD)

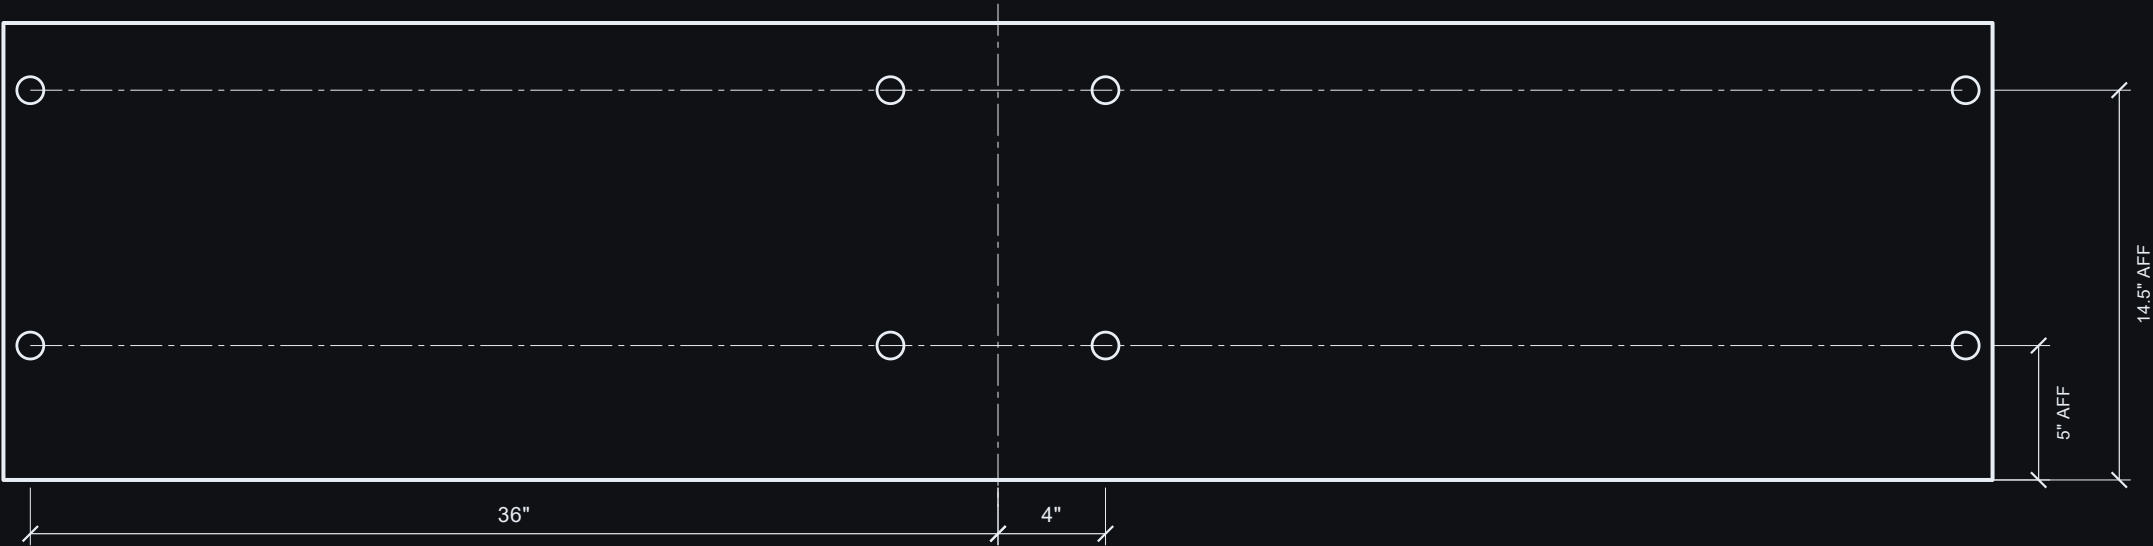

FOOT END (TV CABINET)

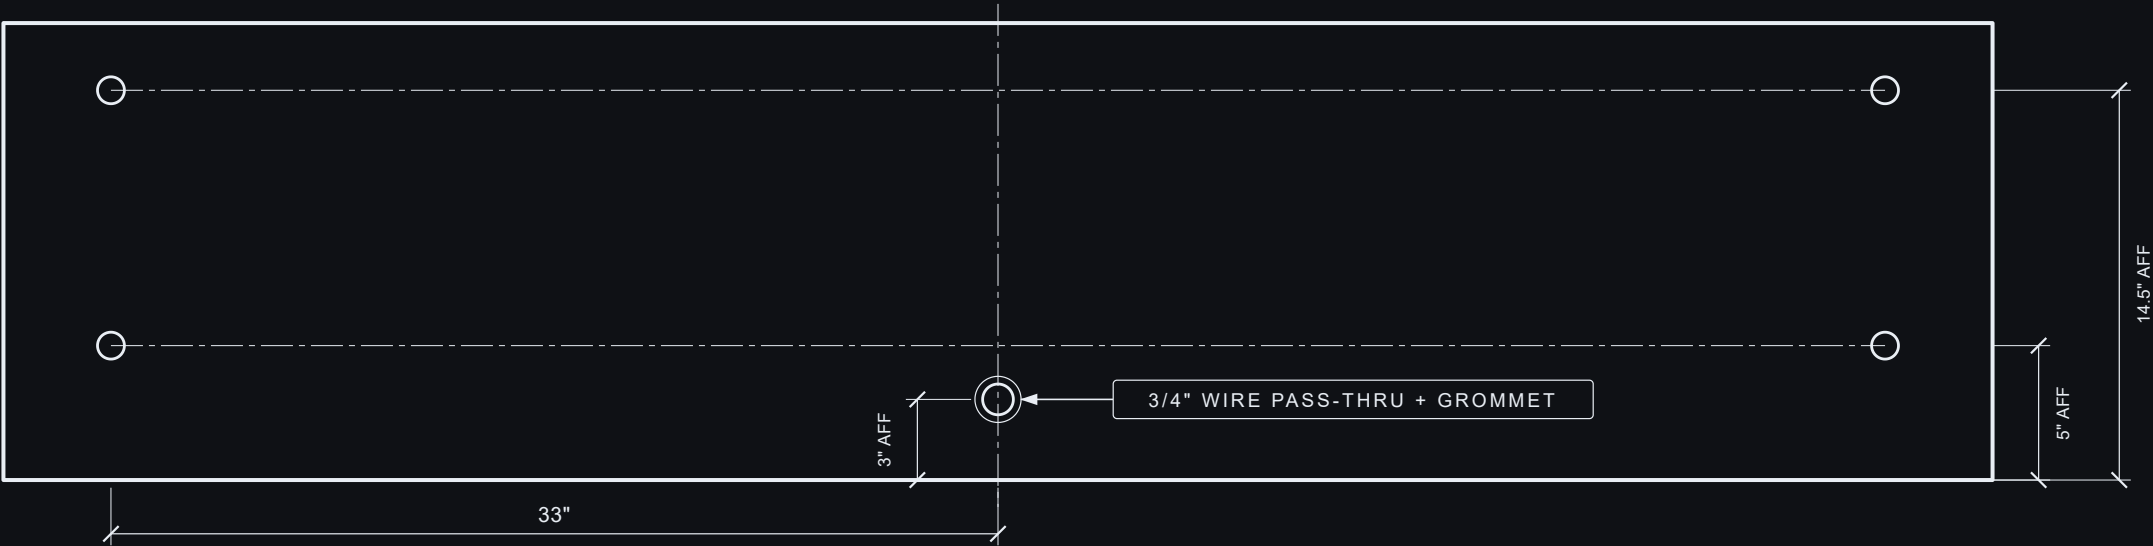

PROJECT HEIRLOOM BED	
LAST UPDATE 2026-06-11 5:31 PM	DRAWING NO. Base-Shop_Blueprint
REV 1.26	SHEET 3 OF 3