


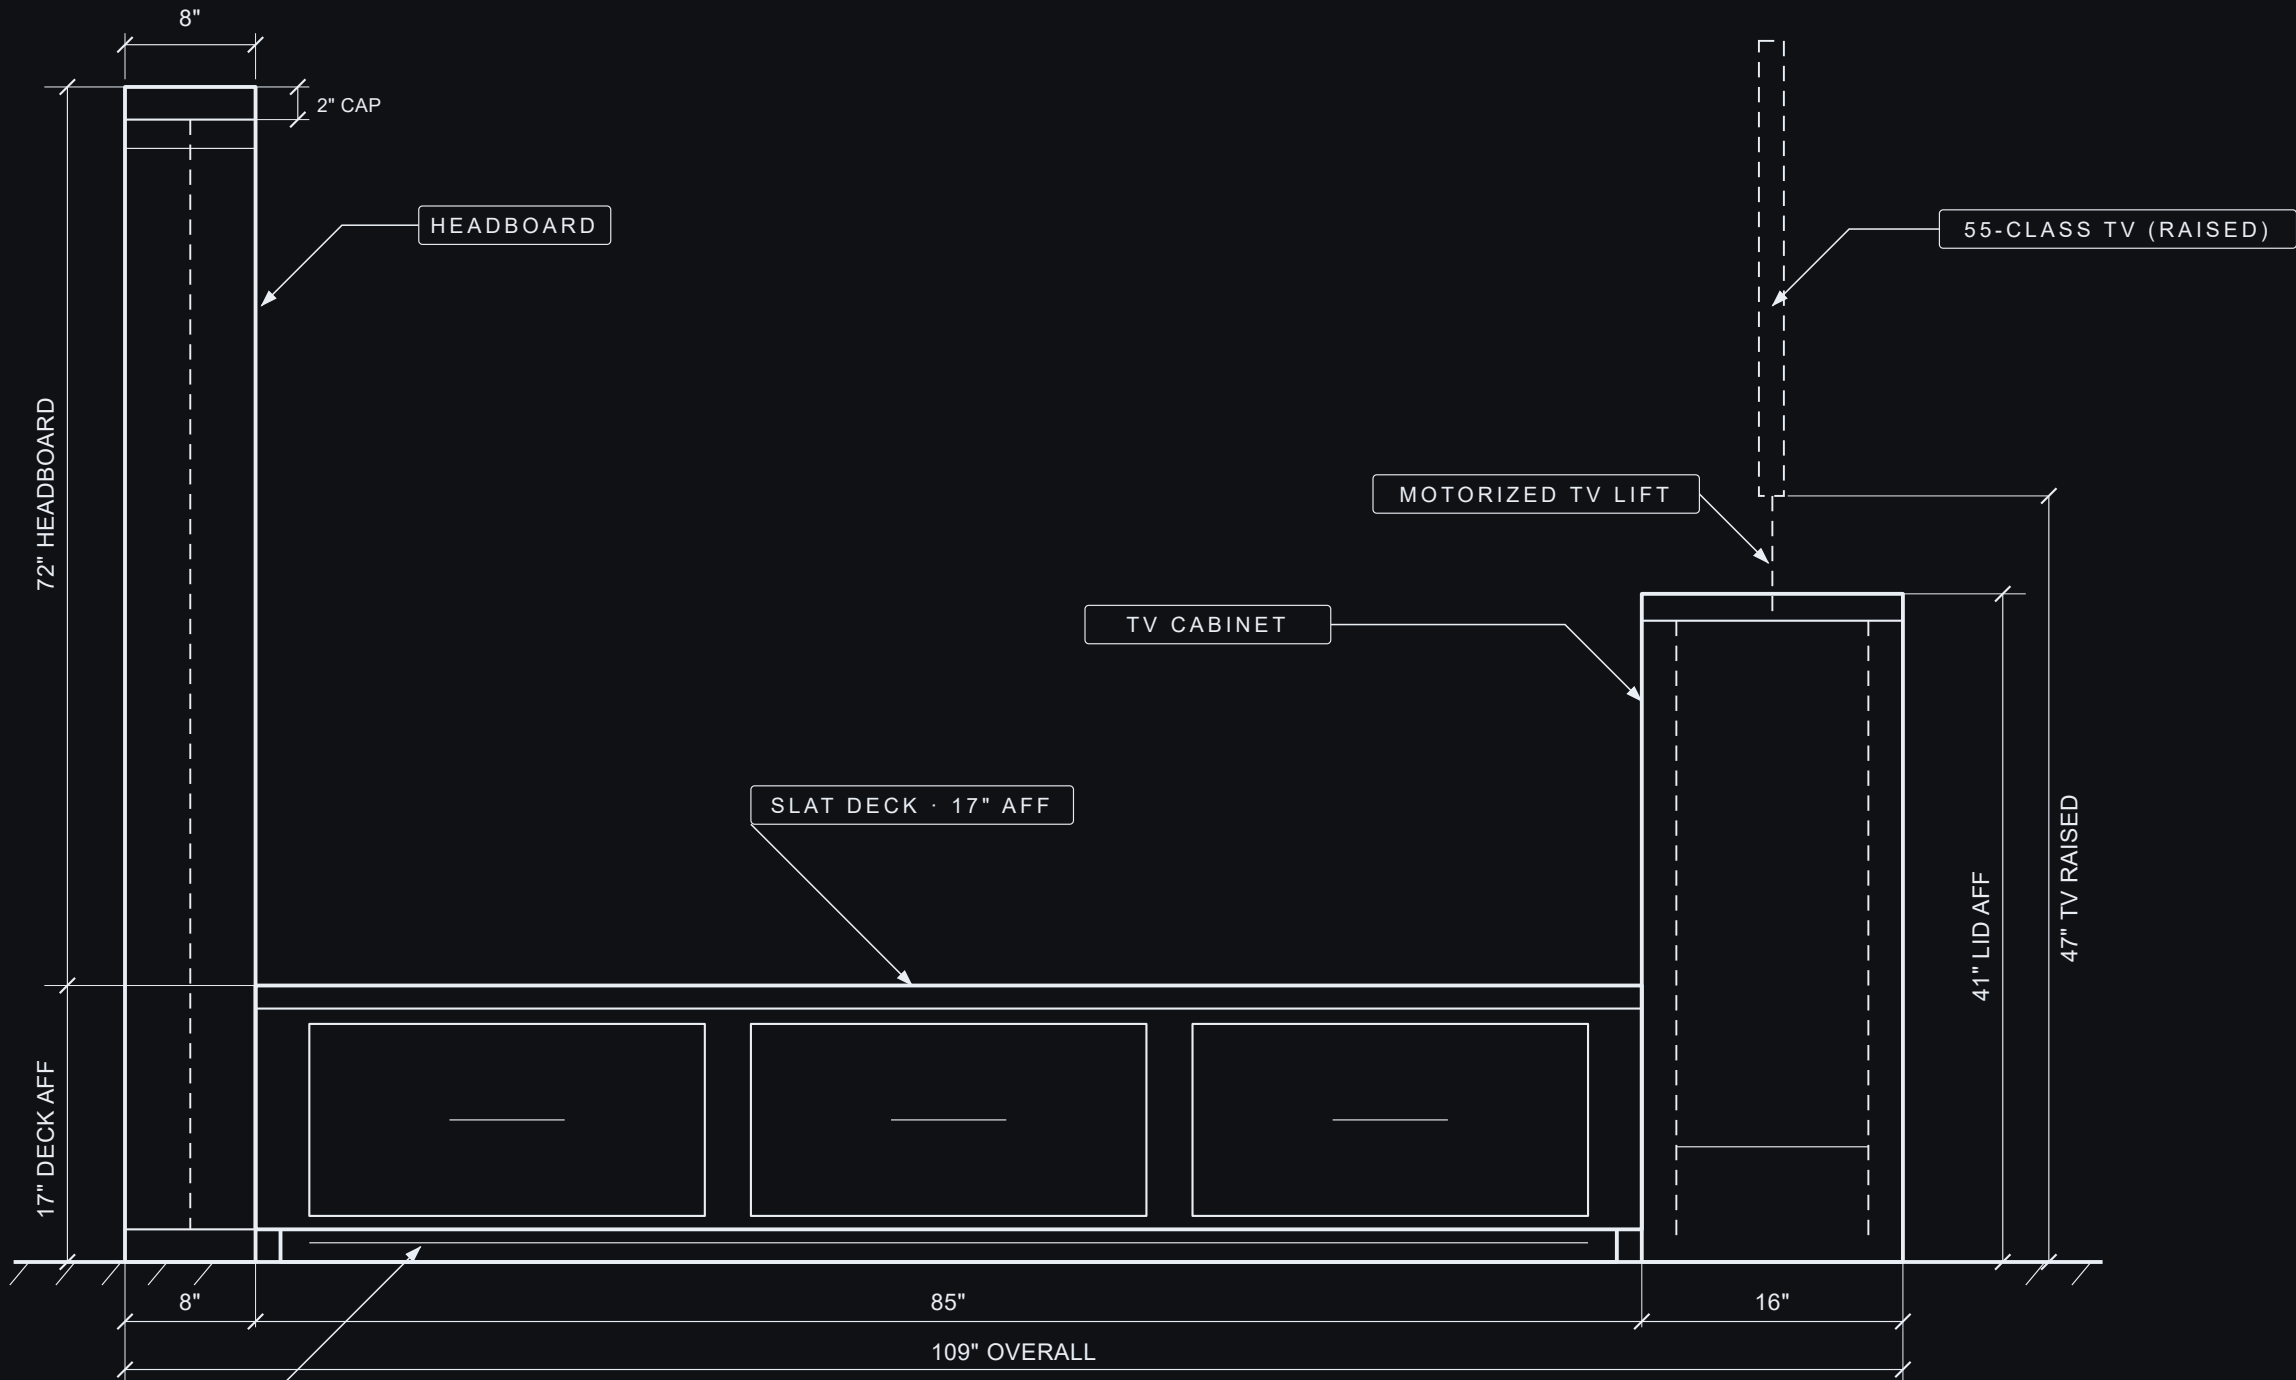

SIDE VIEW

PROJECT HEIRLOOM BED	
LAST UPDATE 2026-06-11 5:31 PM	DRAWING NO. Bed-Side_Blueprint
REV 1.14	SHEET 1 OF 1