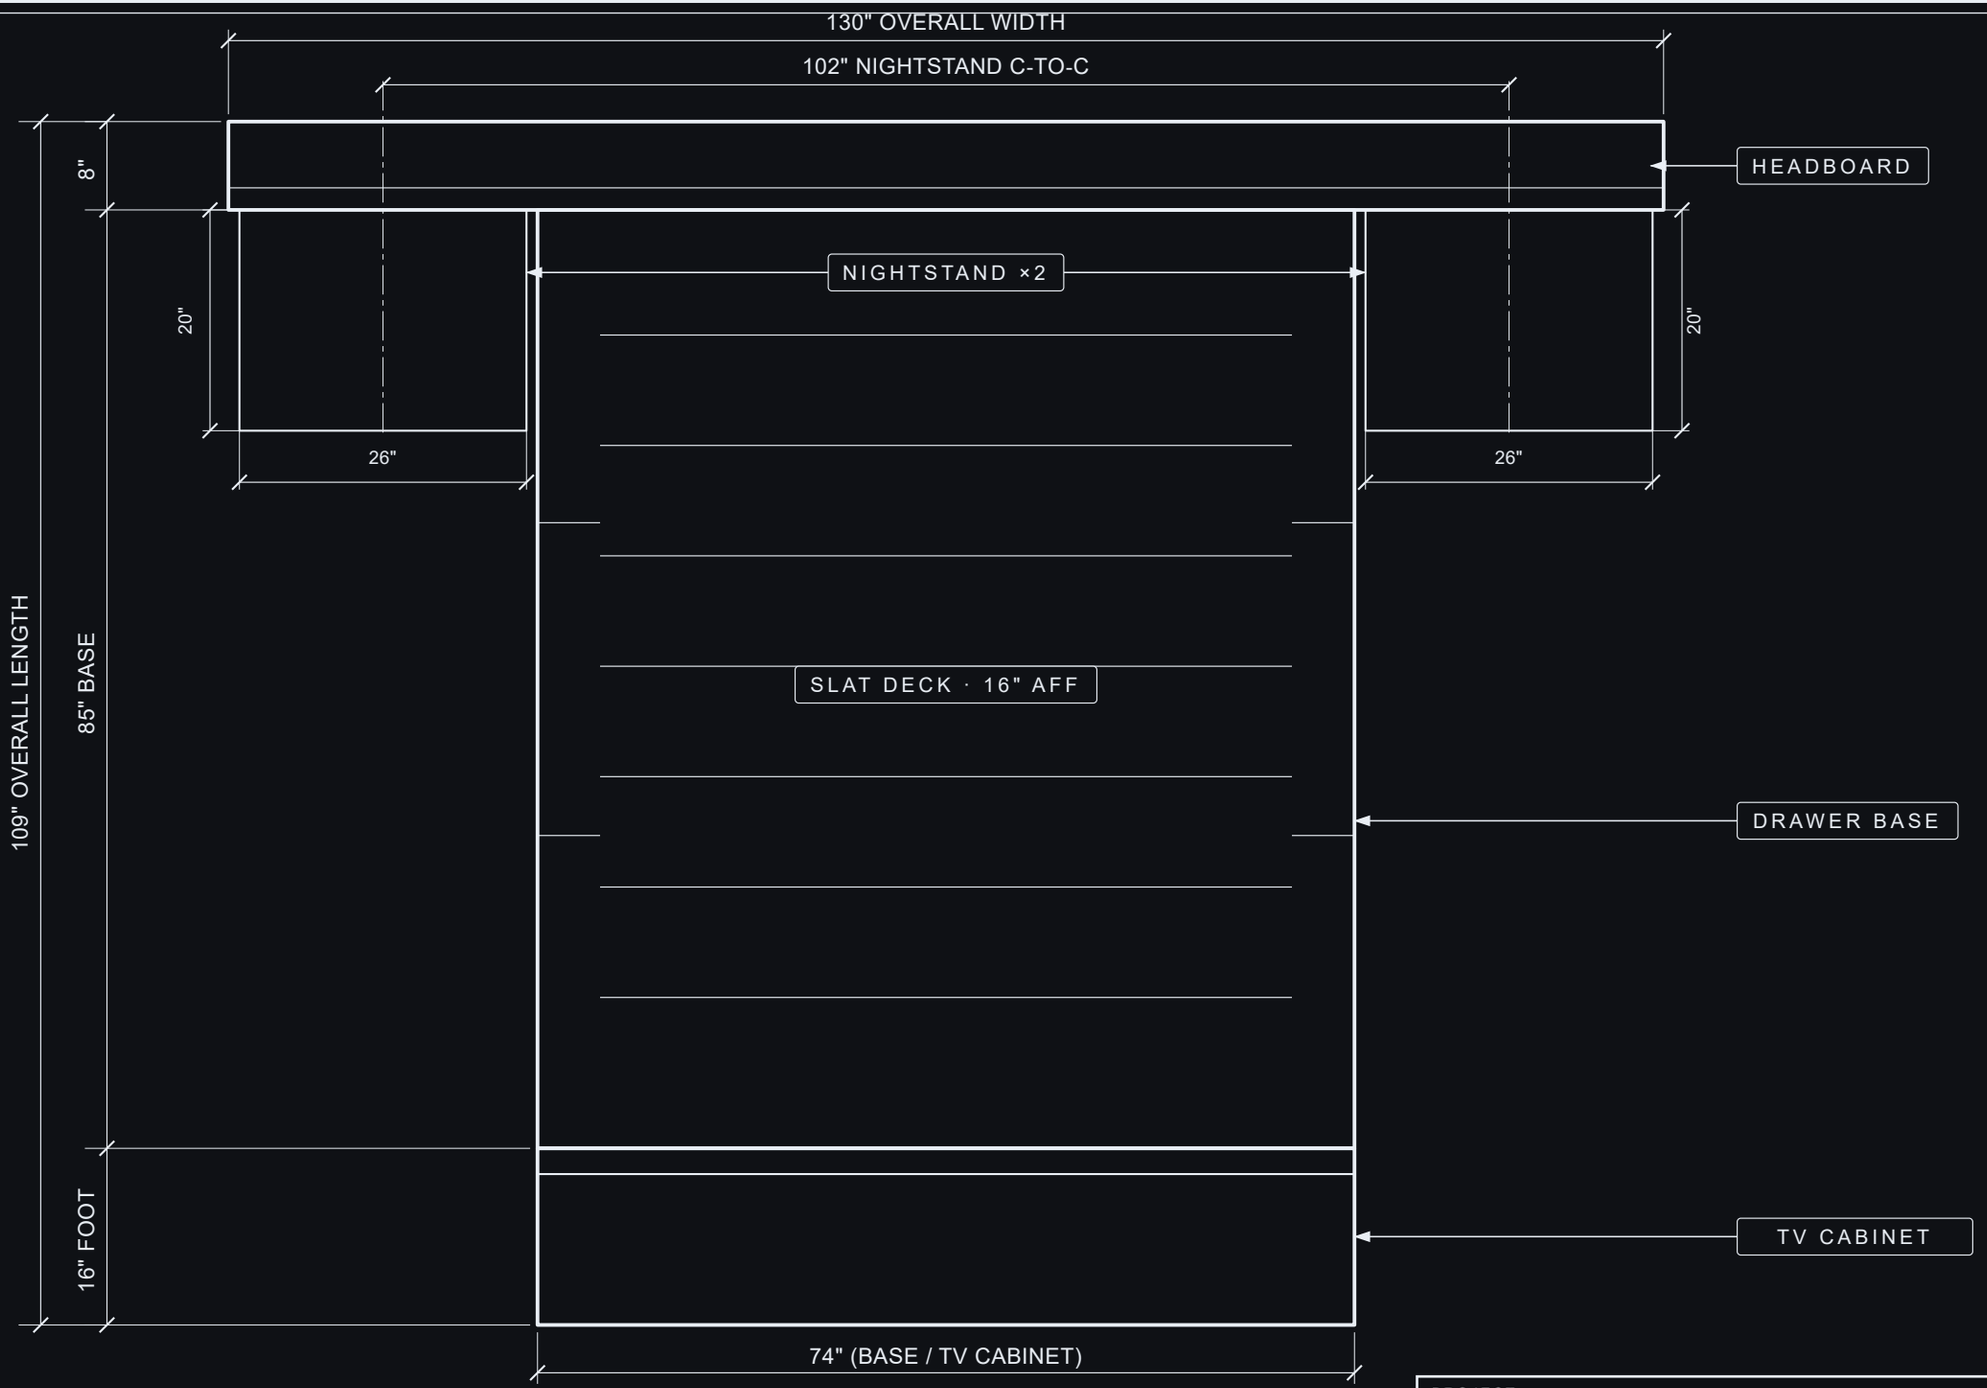


TOP VIEW

PROJECT **HEIRLOOM BED**	
LAST UPDATE **2026-06-11 6:08 PM**	DRAWING NO. **Bed-Top_Blueprint**
REV **3.1**	SHEET 1 OF 1