
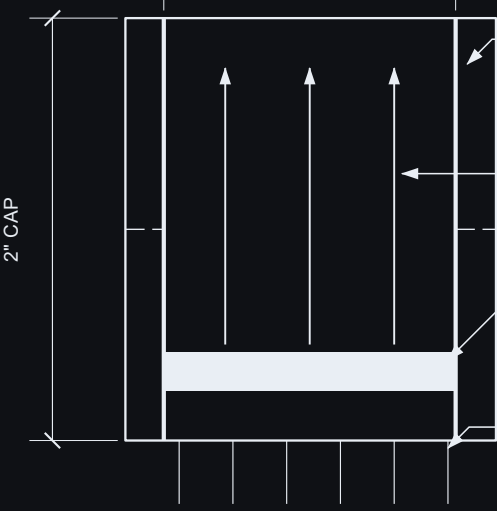


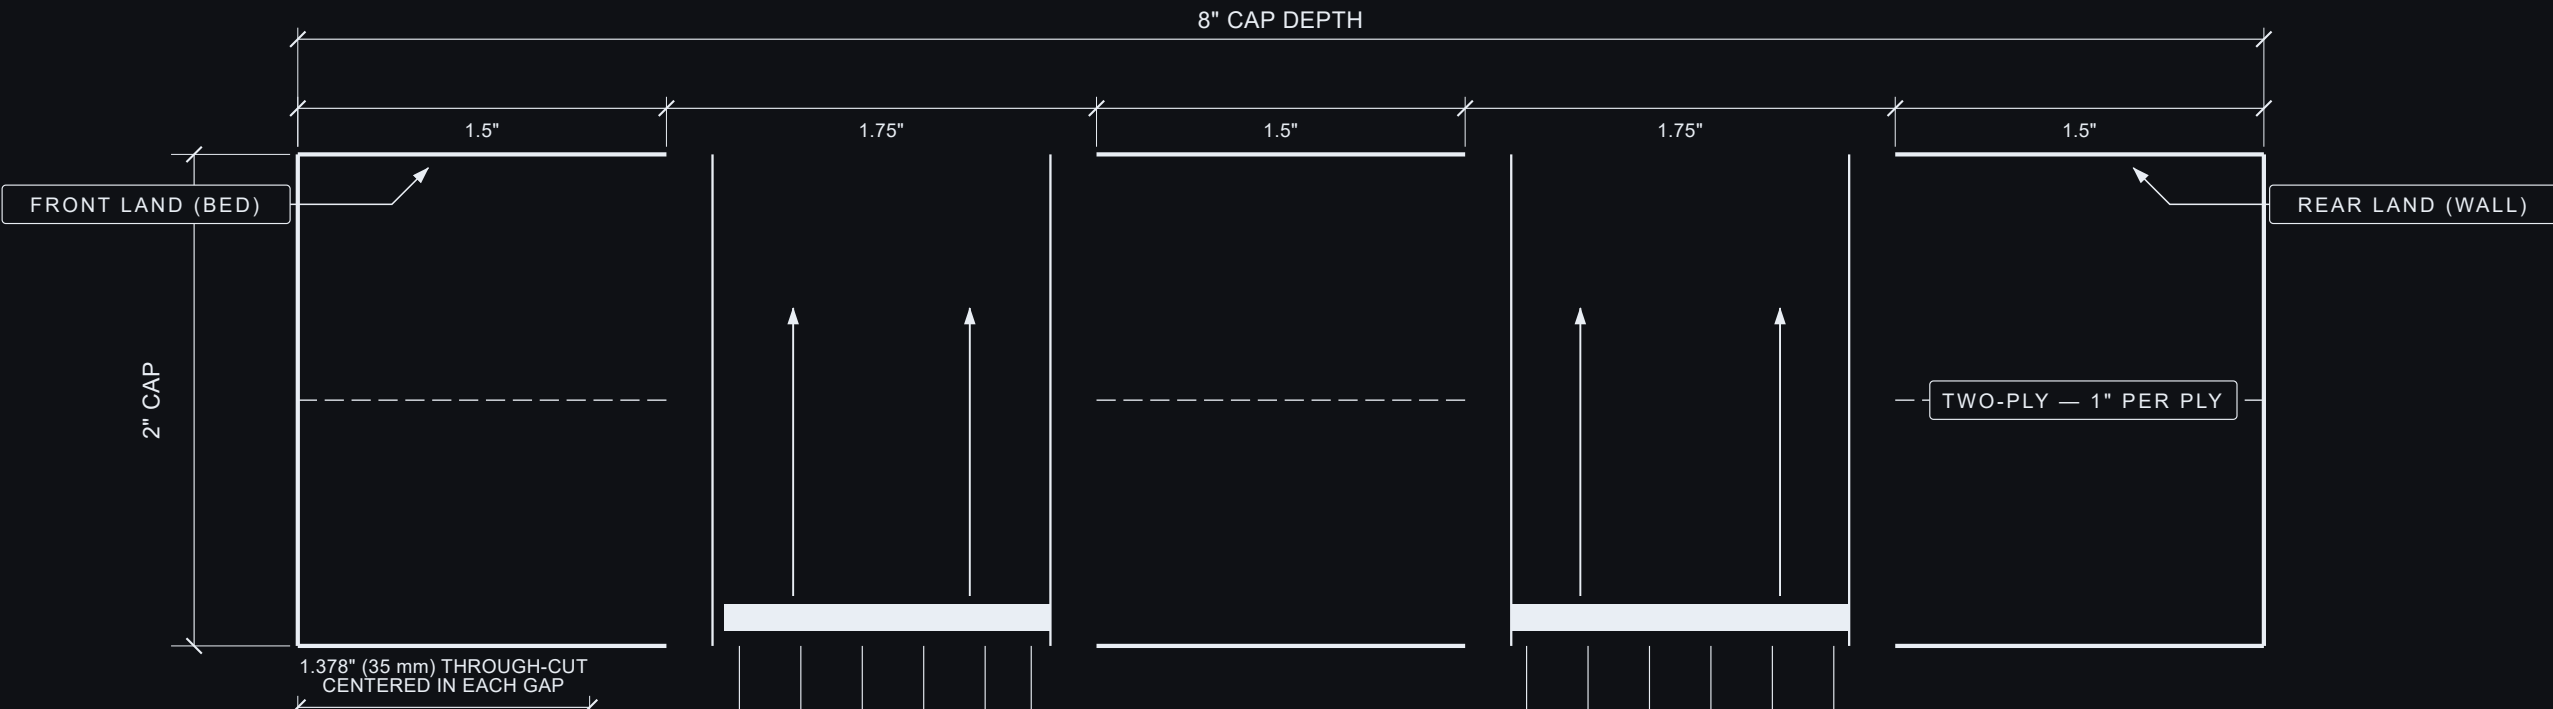

PROJECT HEIRLOOM BED	
LAST UPDATE 2026-06-11 5:31 PM	DRAWING NO. TopCap-LED_Blueprint
REV 1.11	SHEET 1 OF 1