


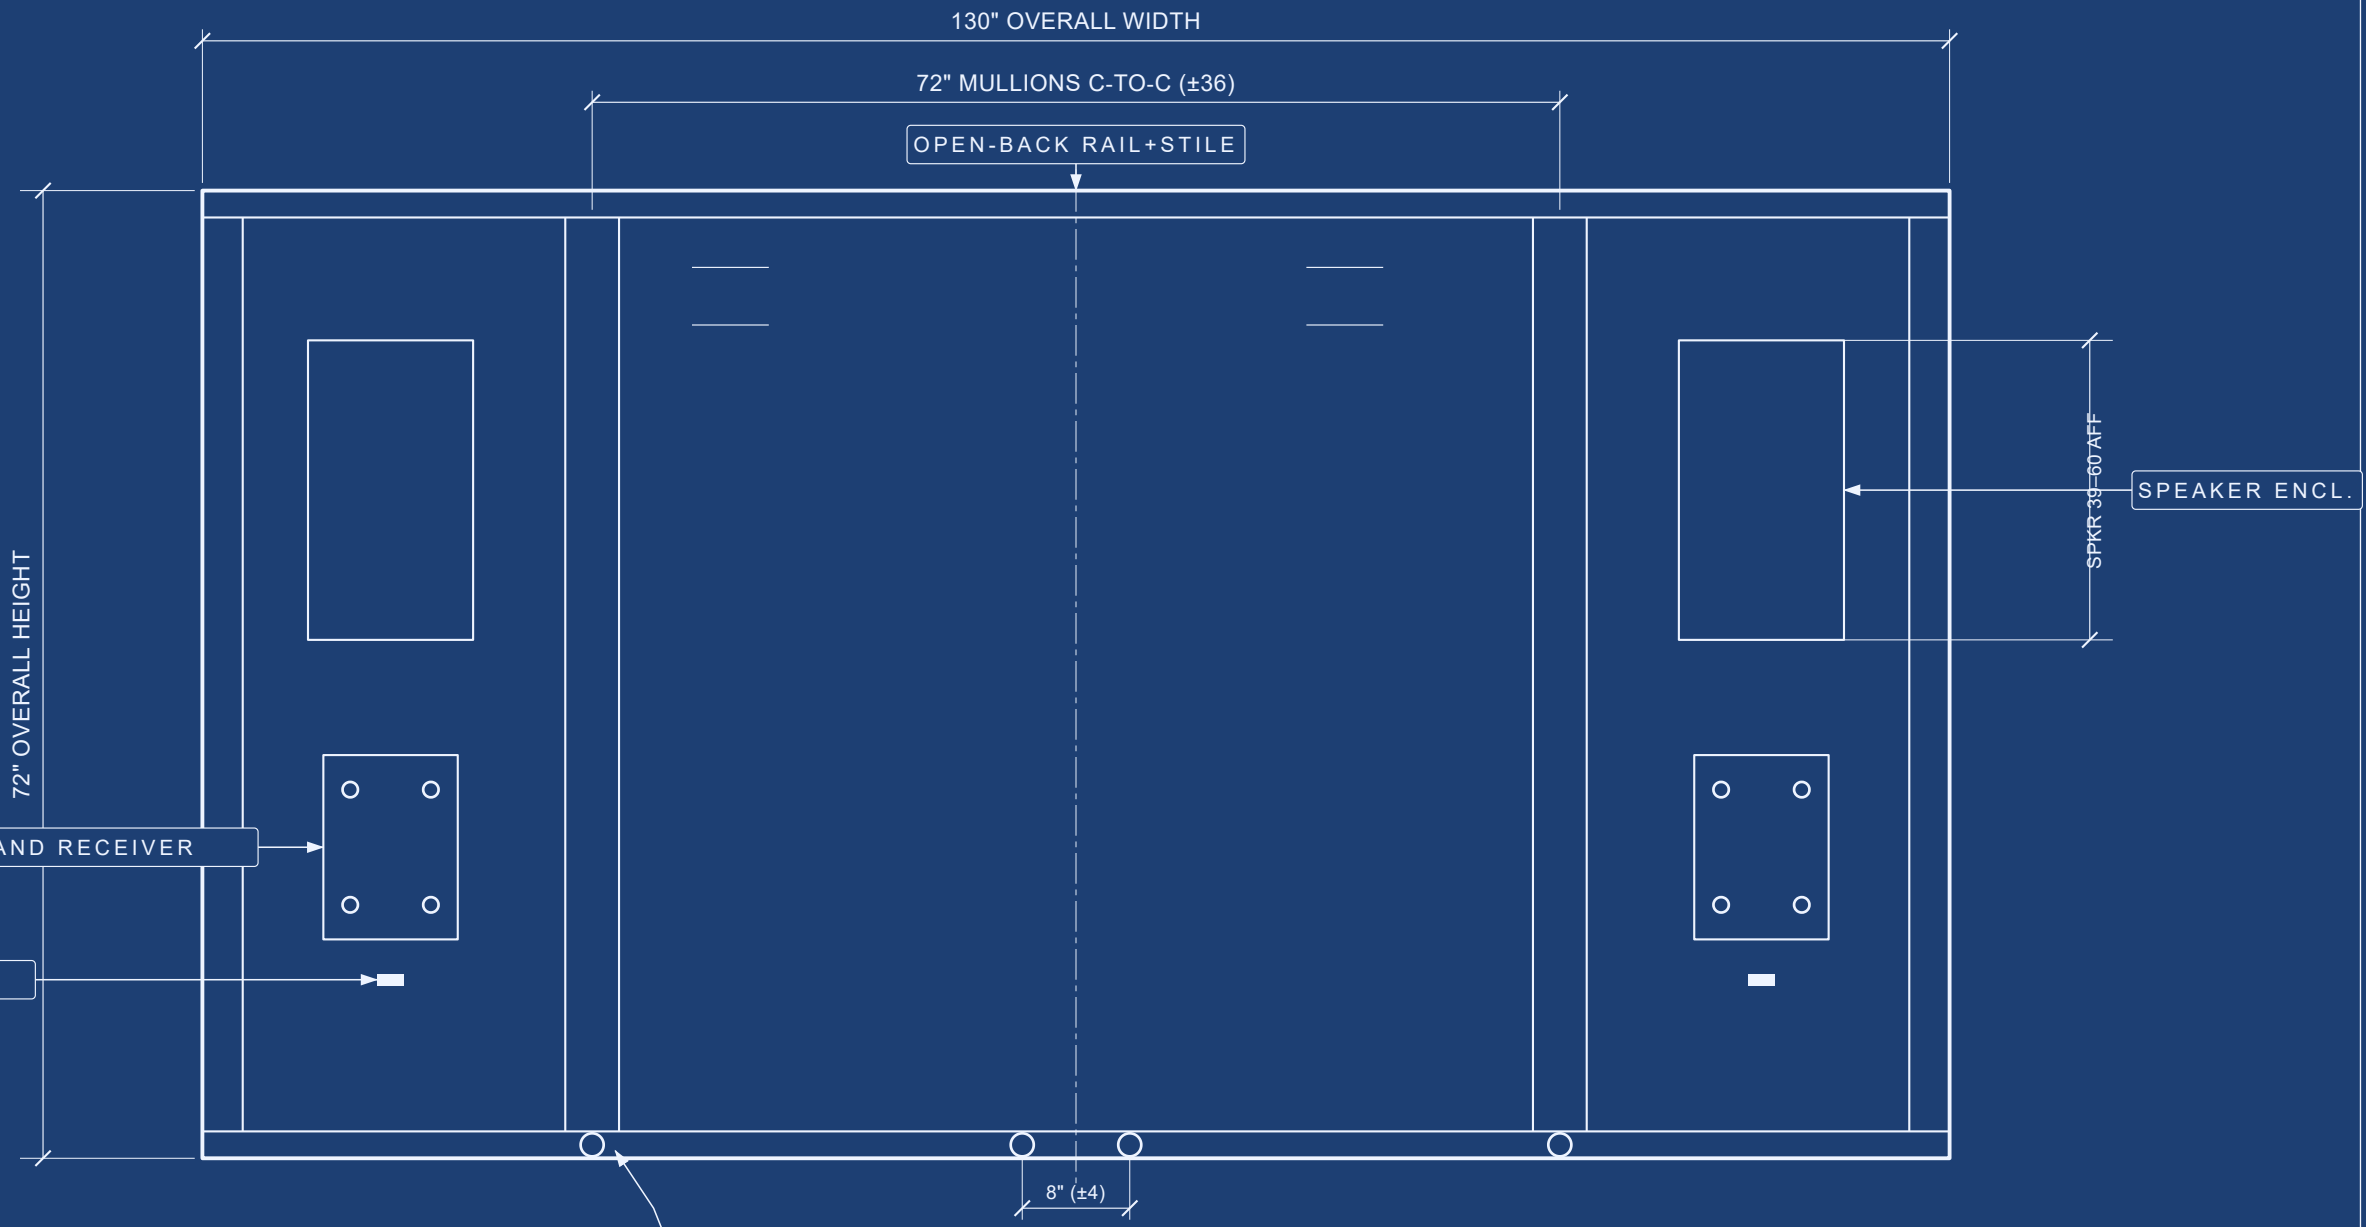

HEADBOARD — REAR ELEVATION



- GENERAL NOTES**
- 1. All dimensions in inches ("). AFF = above finished floor.
 - 2. Open-back rail-and-stile frame; mullions bolt to the base at $\pm 36 + \pm 4$ (bed bolts).
 - 3. Nightstands hang on full-depth receivers (captive-nut ports). Do not scale — figured dims govern.

PROJECT HEIRLOOM BED	
DRAWING Headboard — Rear	DRAWING NO. Headboard-Rear_Blueprint
REV 1.0	SHEET 1 OF 1