


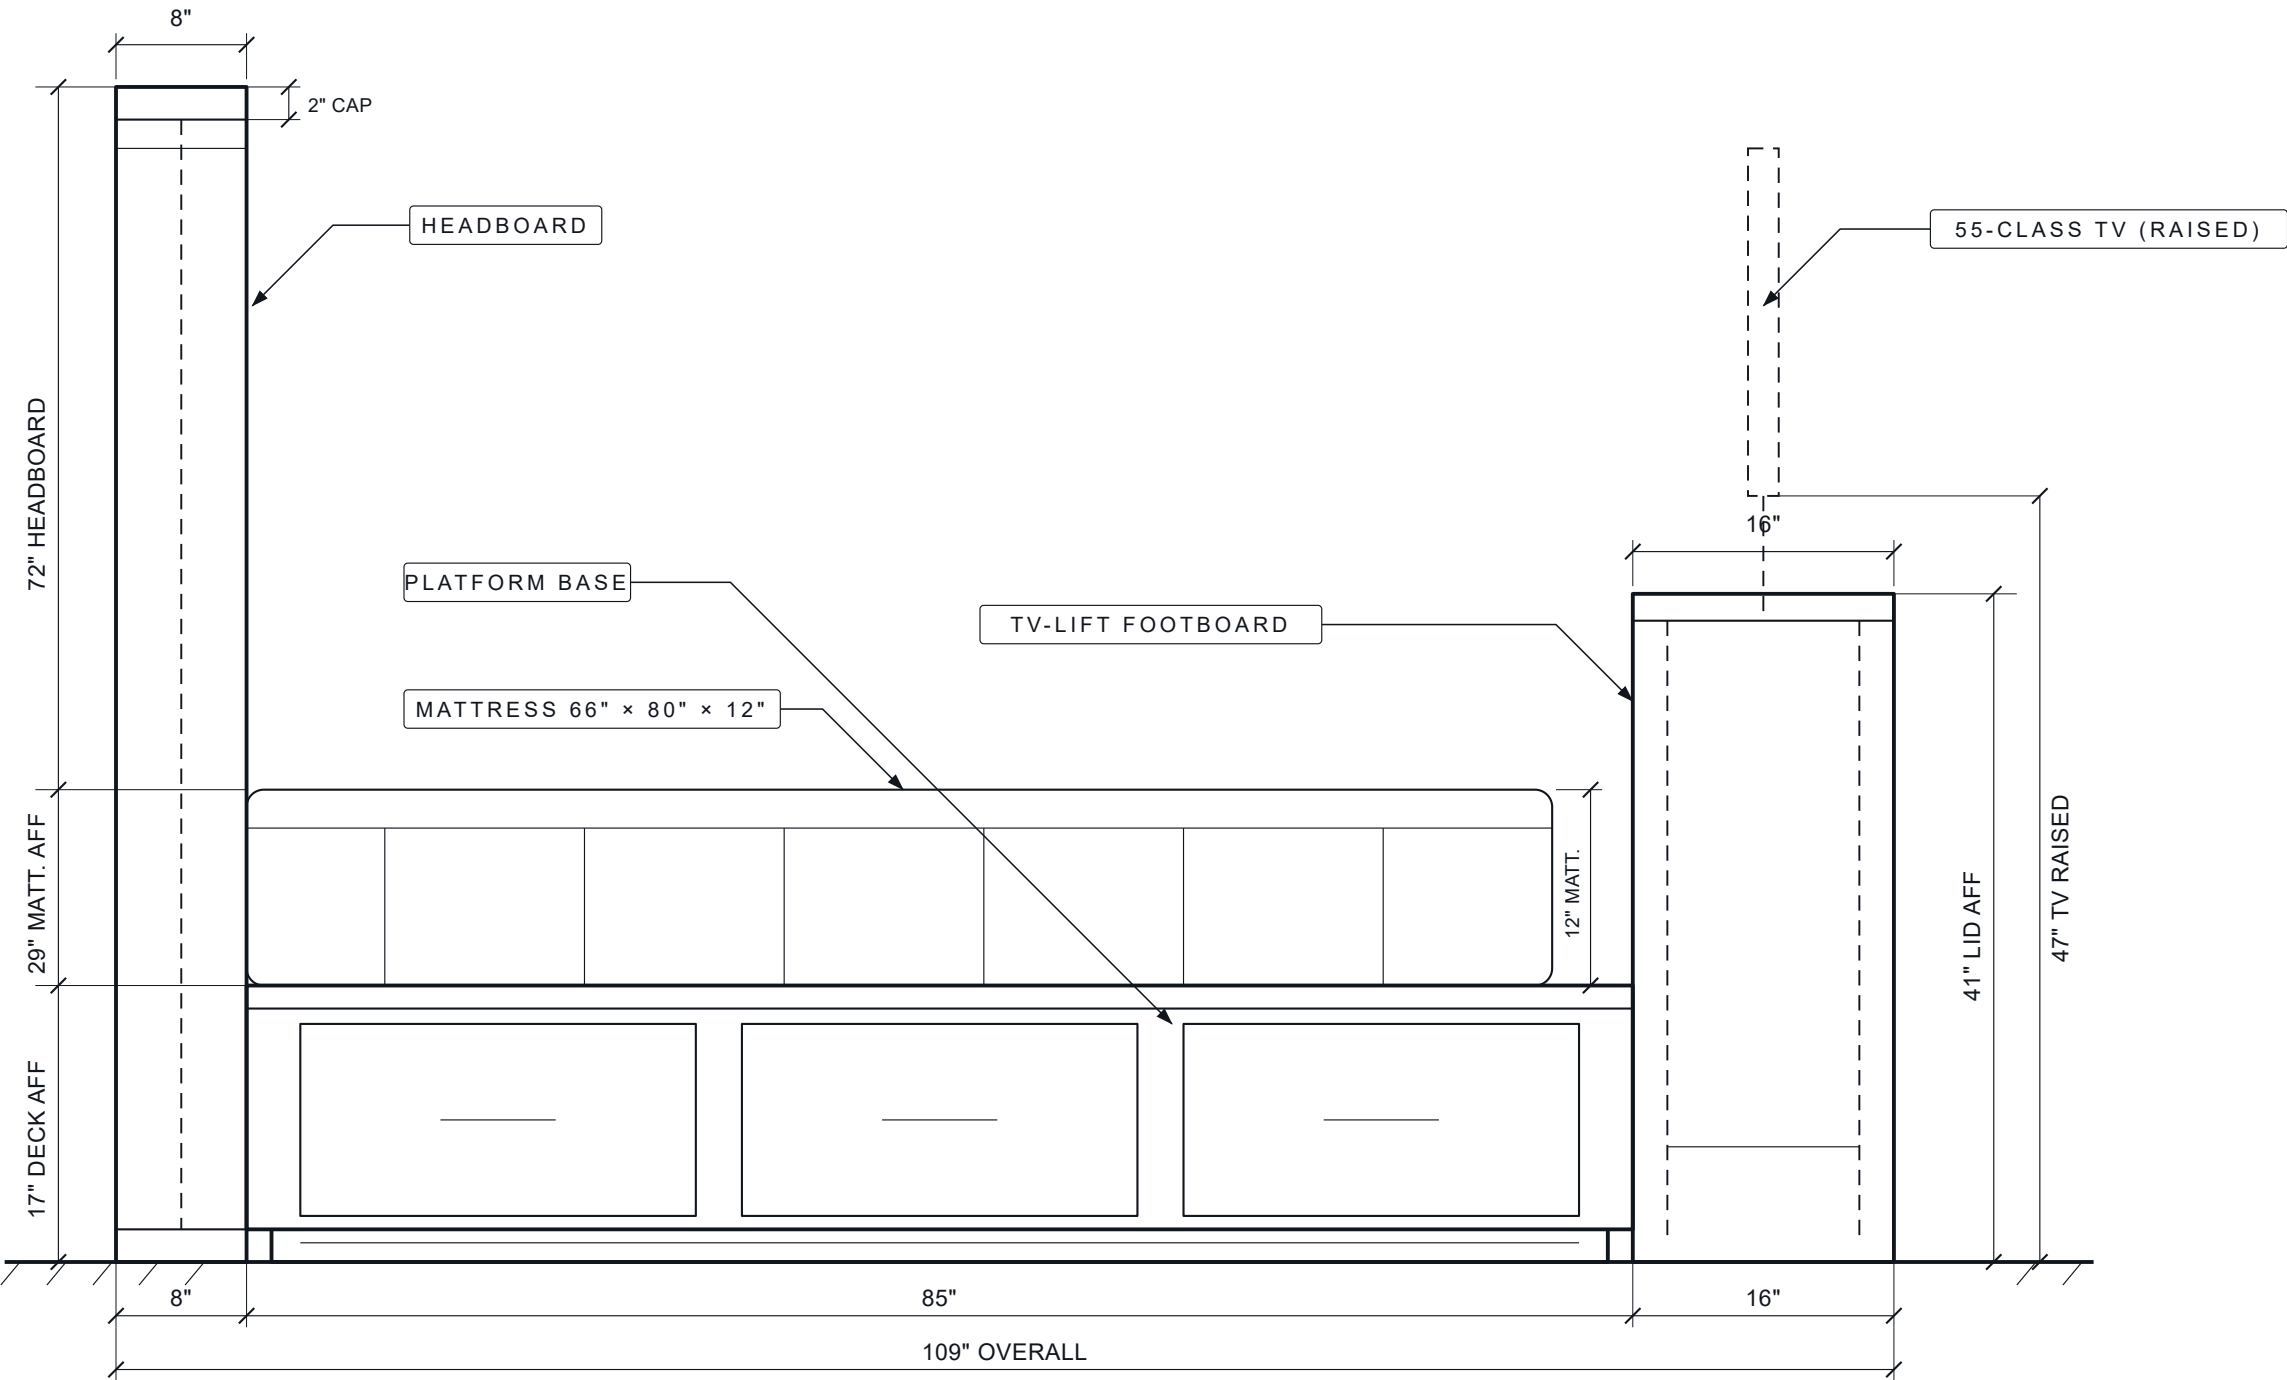

SIDE ELEVATION

- GENERAL NOTES
1. All dimensions in inches ("). AFF = above finished floor.
2. Figured dimensions govern — DO NOT scale from the print.

PROJECT HEIRLOOM BED	
DRAWING Side Elevation	DRAWING NO. Bed-Side_Blueprint
REV 1.1	SHEET 1 OF 1