


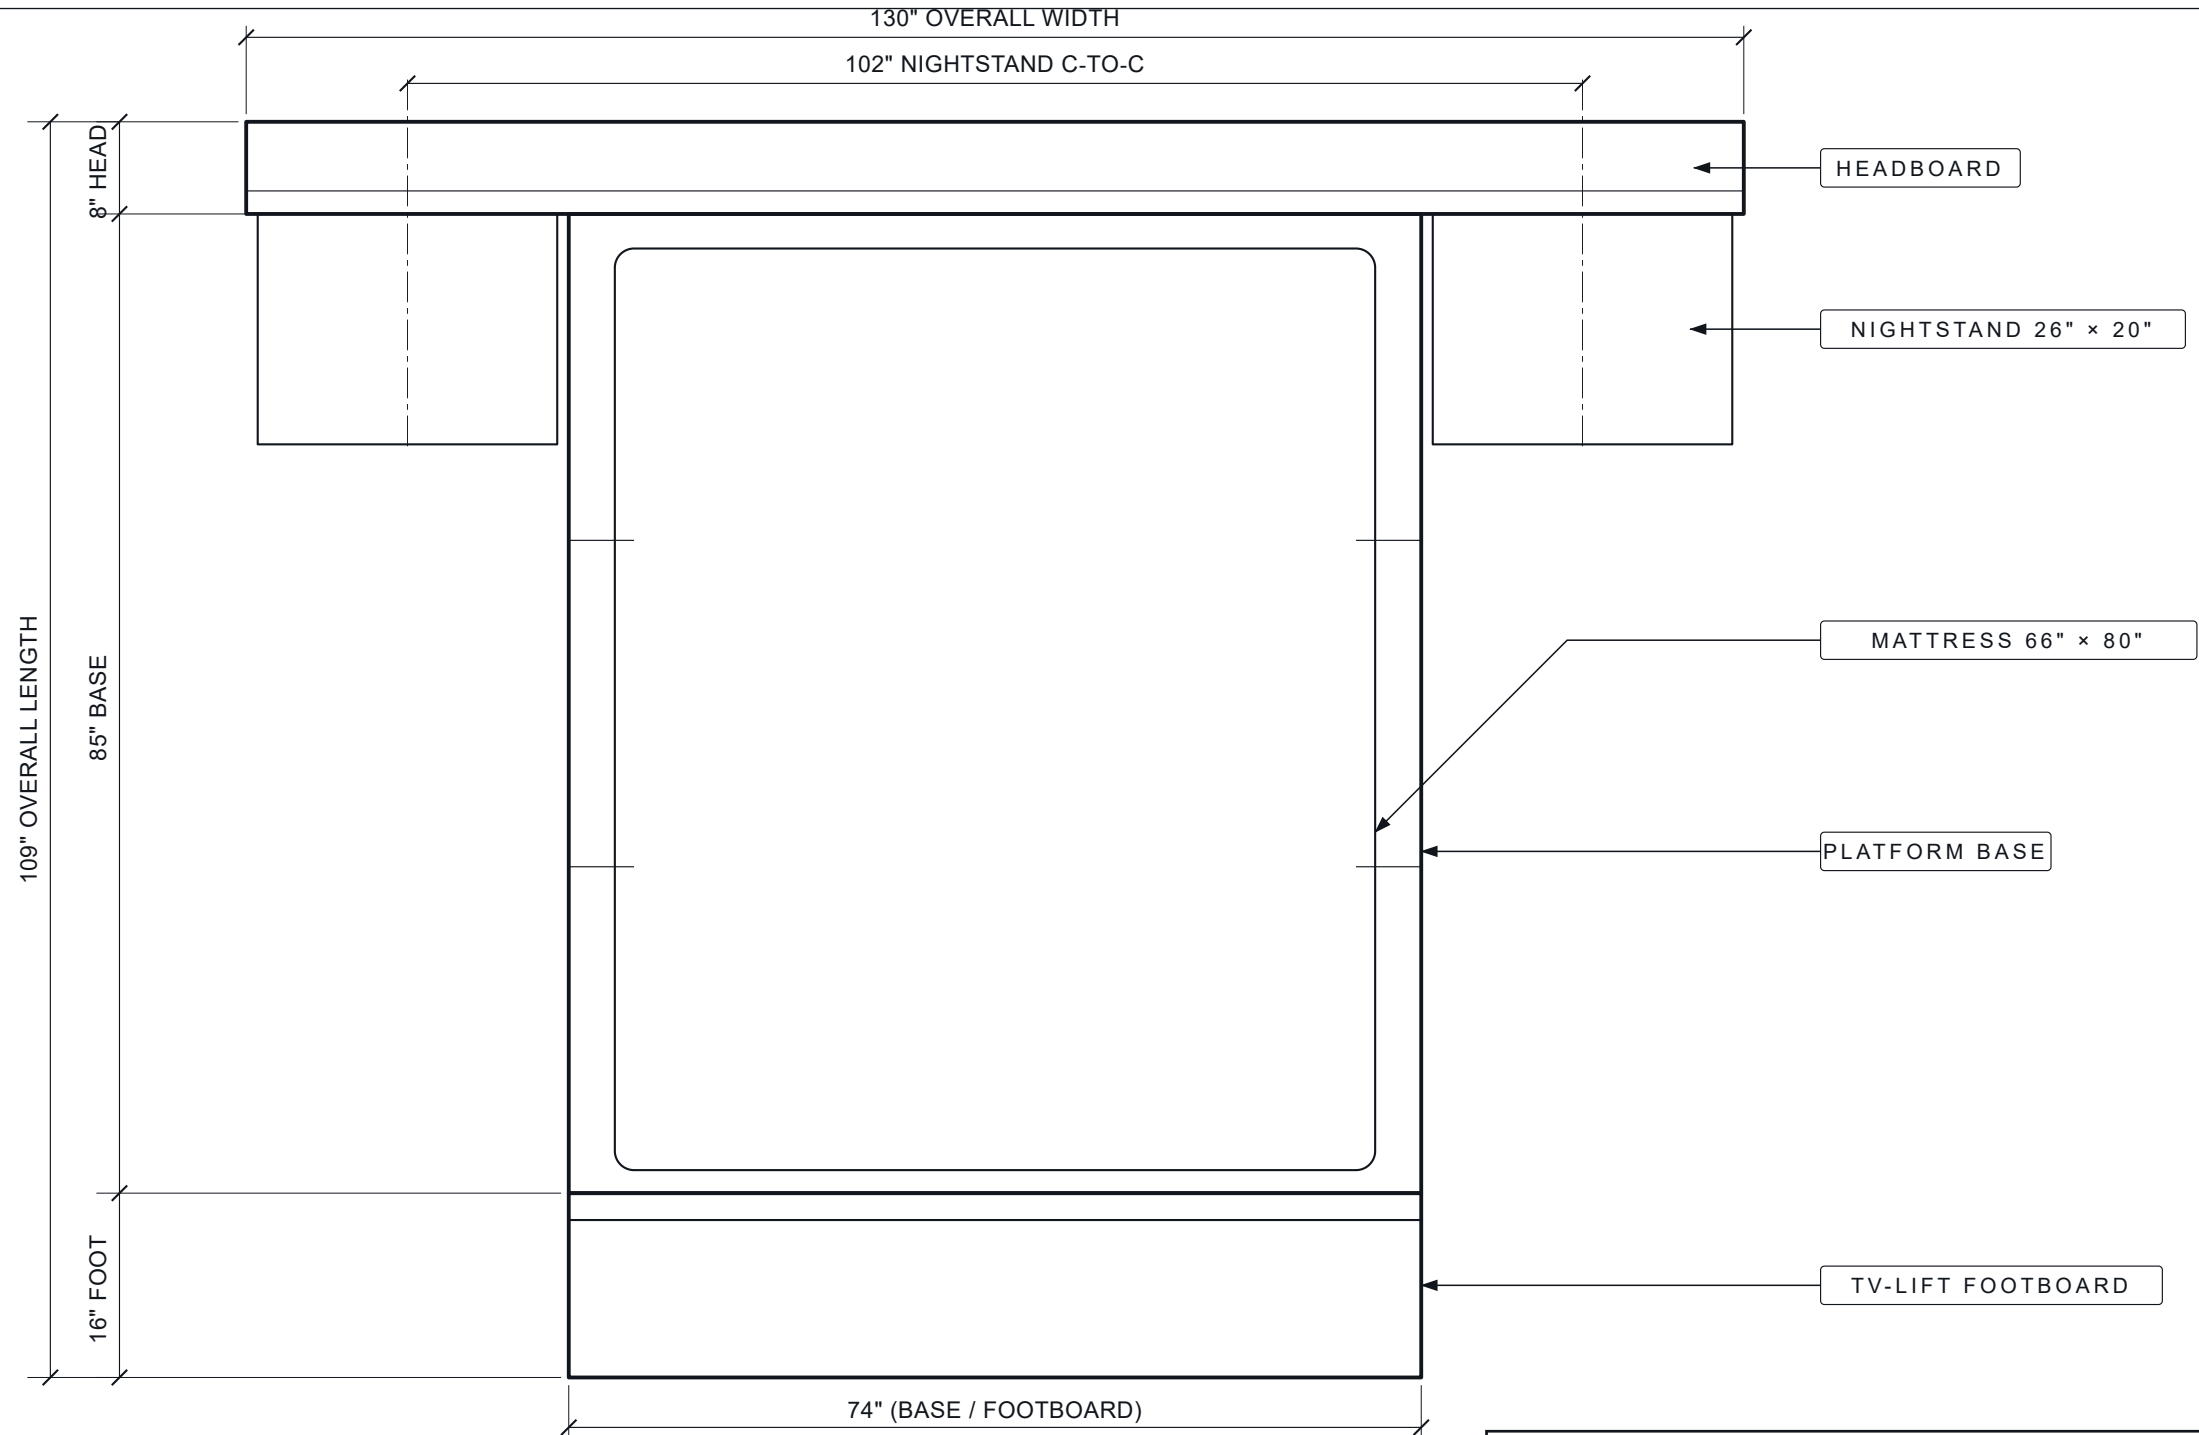

GENERAL NOTES

1. All dimensions in inches ("). Plan viewed top-down, head at top.

2. Figured dimensions govern — DO NOT scale from the print.

PLAN — TOP DOWN

PROJECT HEIRLOOM BED	
DRAWING Plan (Top-Down)	DRAWING NO. Bed-Top_Blueprint
REV 2.0	SHEET 1 OF 1