


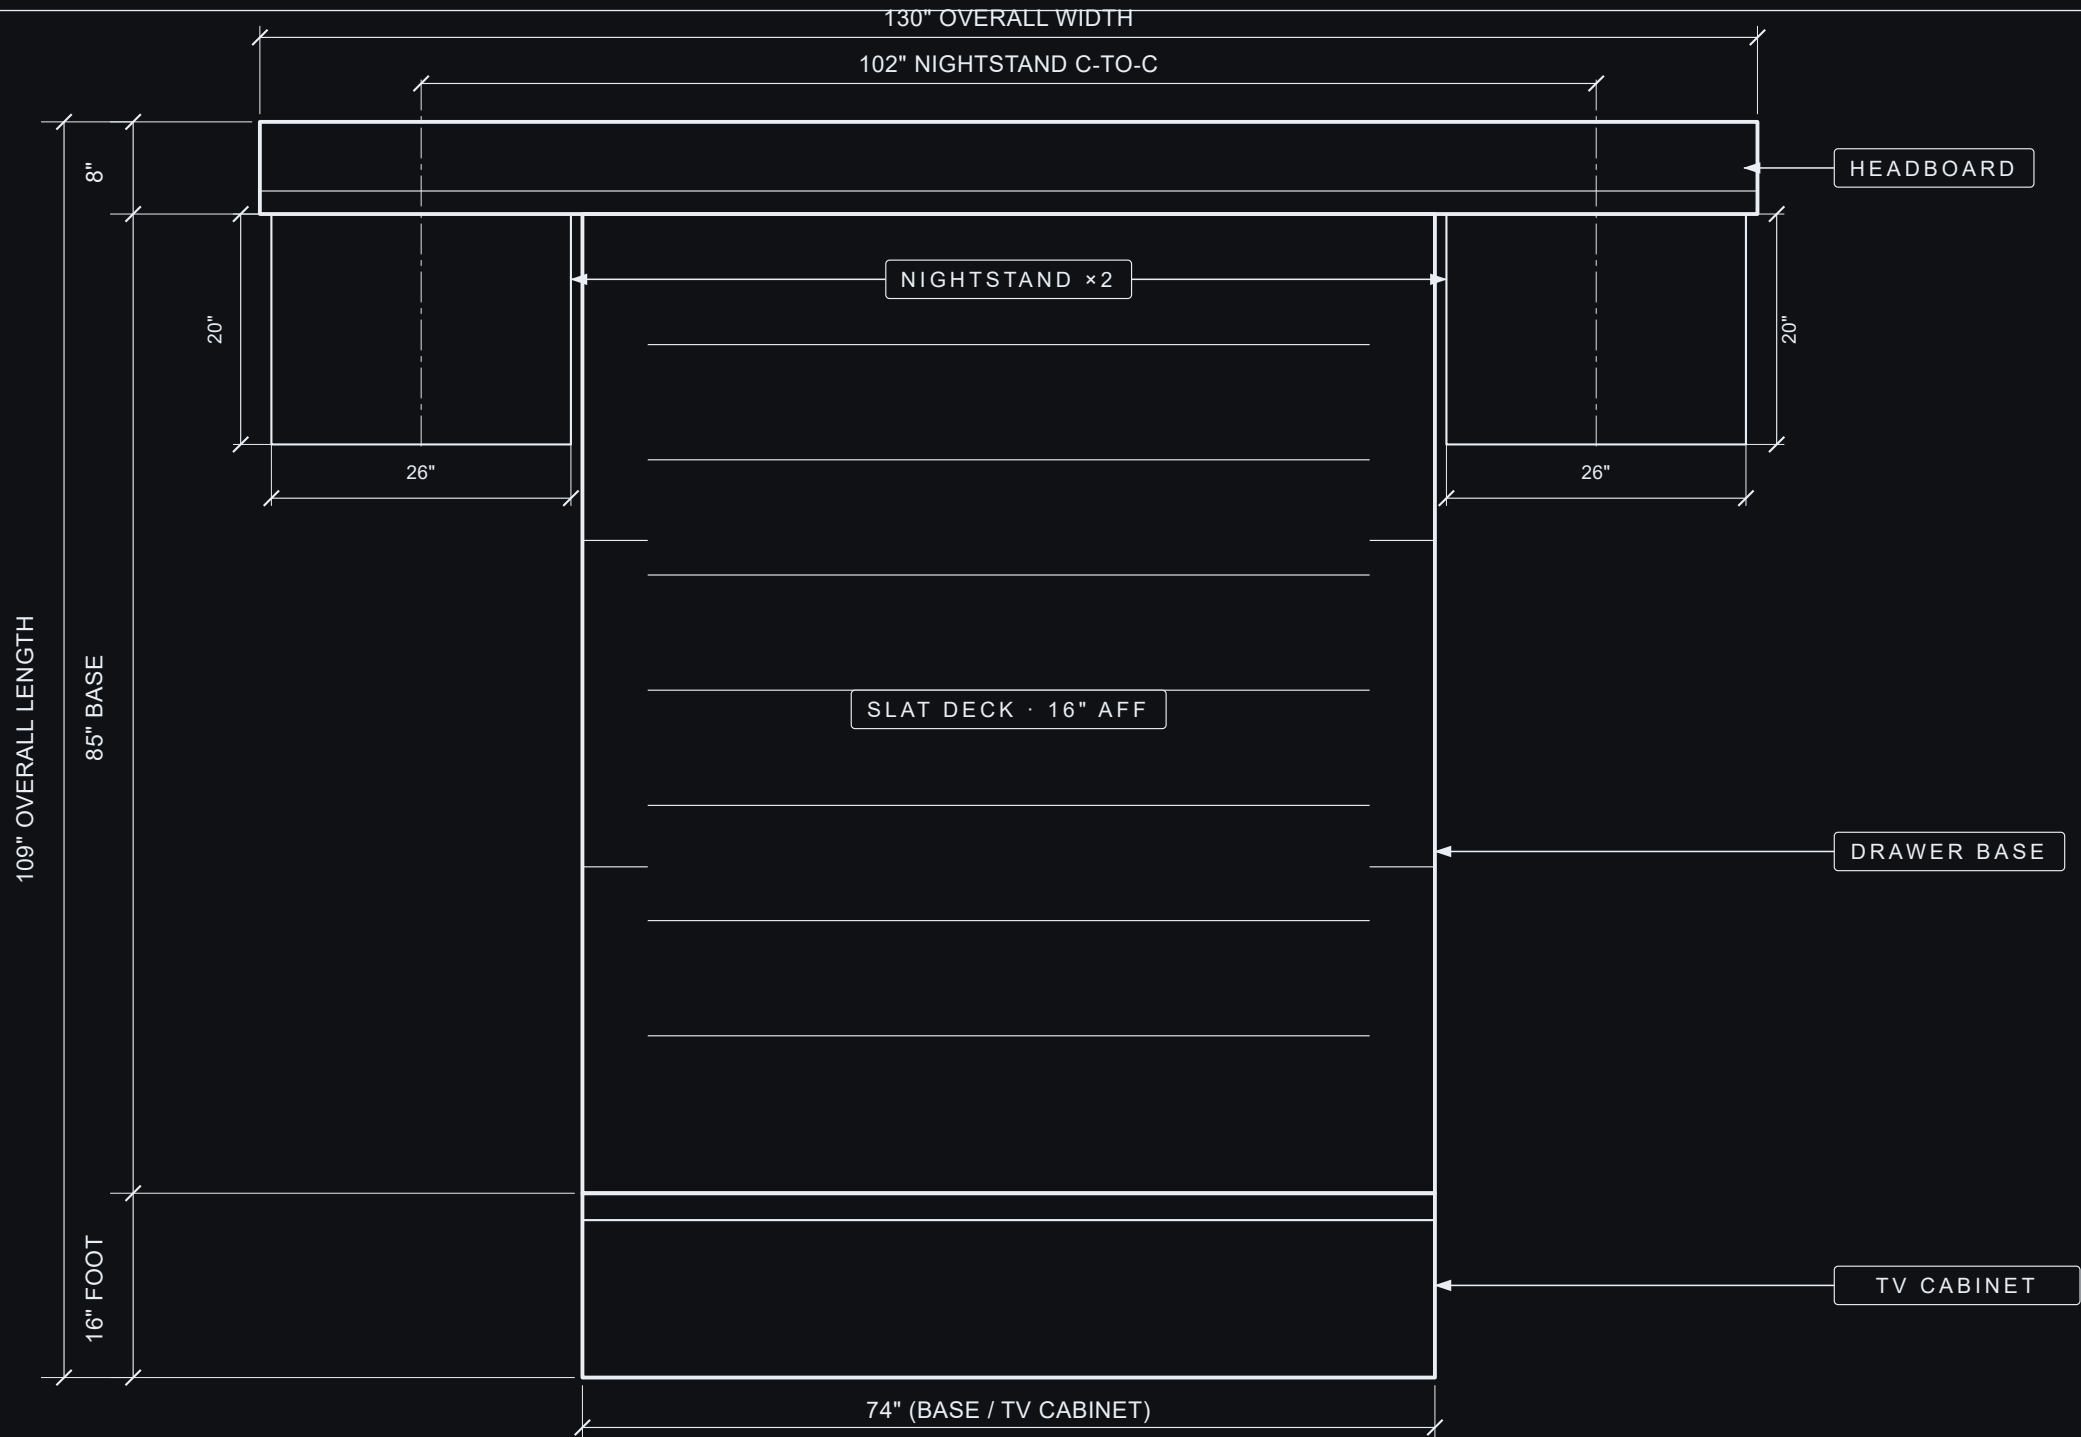

TOP VIEW

PROJECT	HEIRLOOM BED	SHEET 1 OF 1
DRAWING NO.	Bed-Top_Blueprint	
LAST UPDATE	2026-06-11 7:44 PM	REV 3.5