
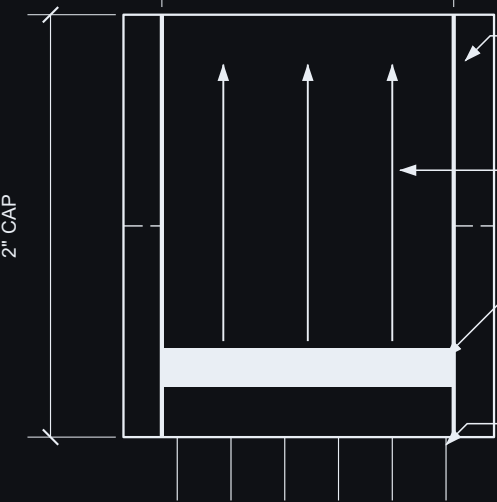


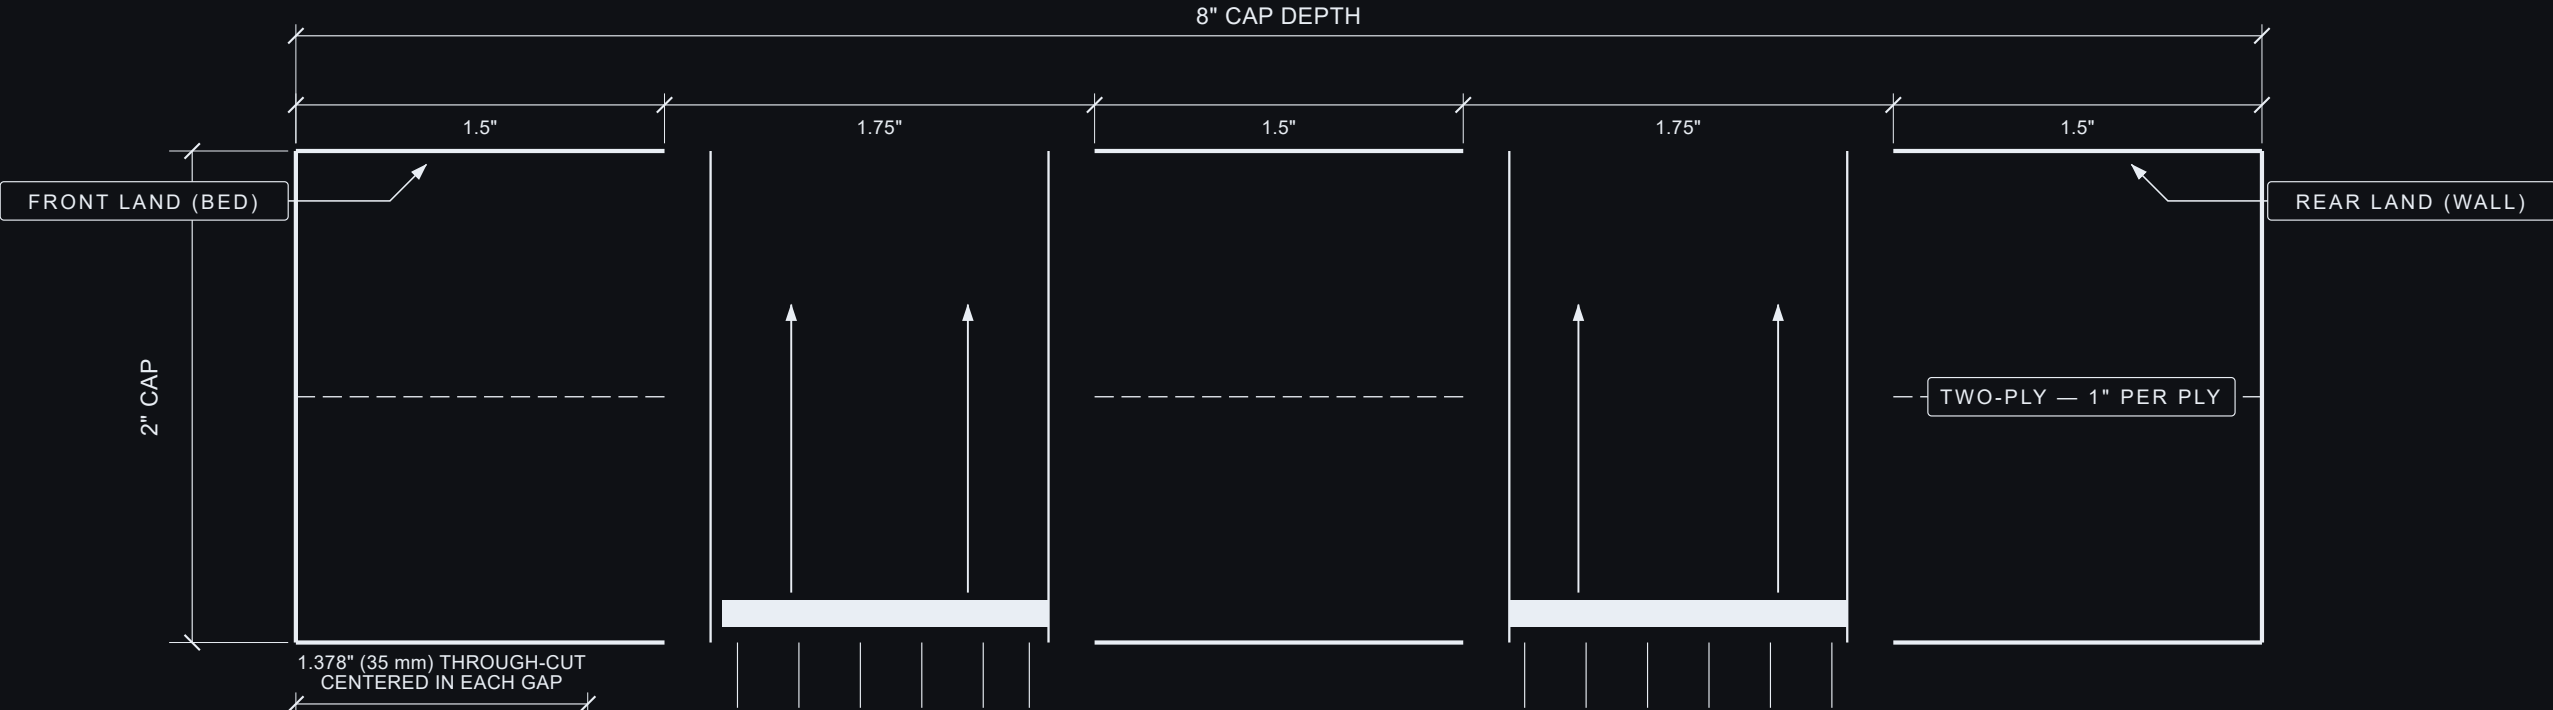

0.185" (4.7 mm) WALL EACH SIDE

LIGHT EMITS UP — UPLIGHT

LED STRIP — SEATS AT THE CHANNEL BOTTOM

FINS VENT OUT THE BOTTOM

PROJECT	HEIRLOOM BED	SHEET 1 OF 1
DRAWING NO.	TopCap-LED_Blueprint	
LAST UPDATE	2026-06-11 7:44 PM	REV 1.14