
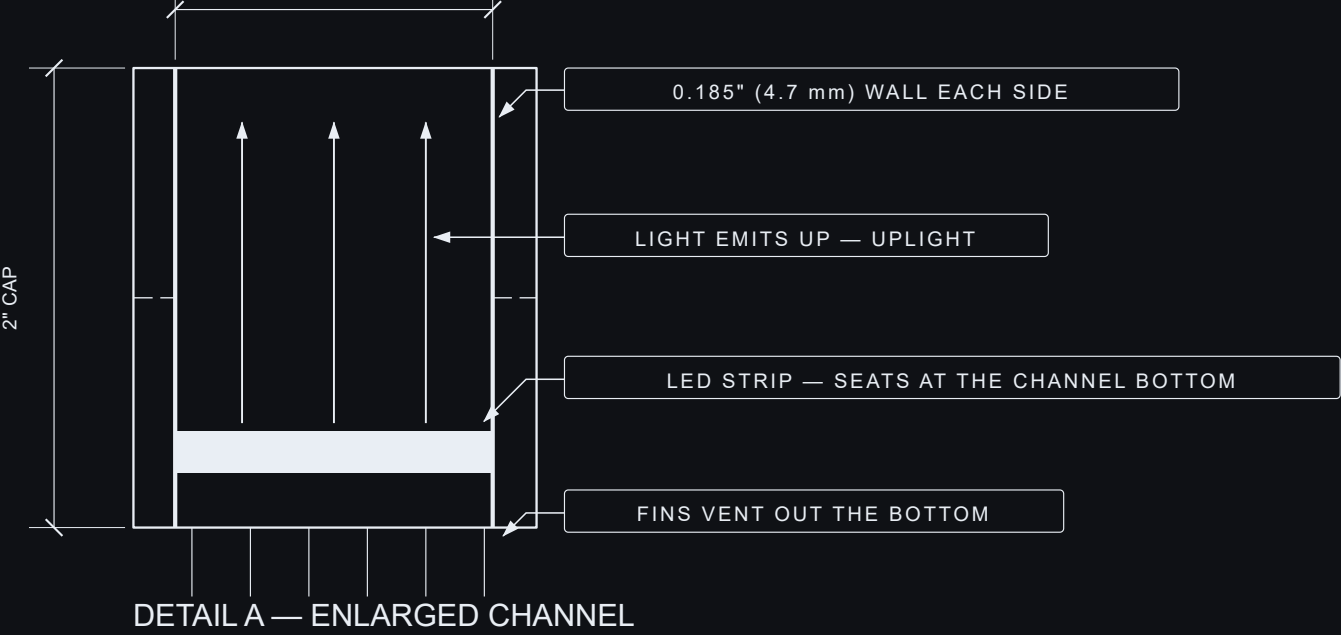


TOP-CAP LED CHANNEL — SECTION

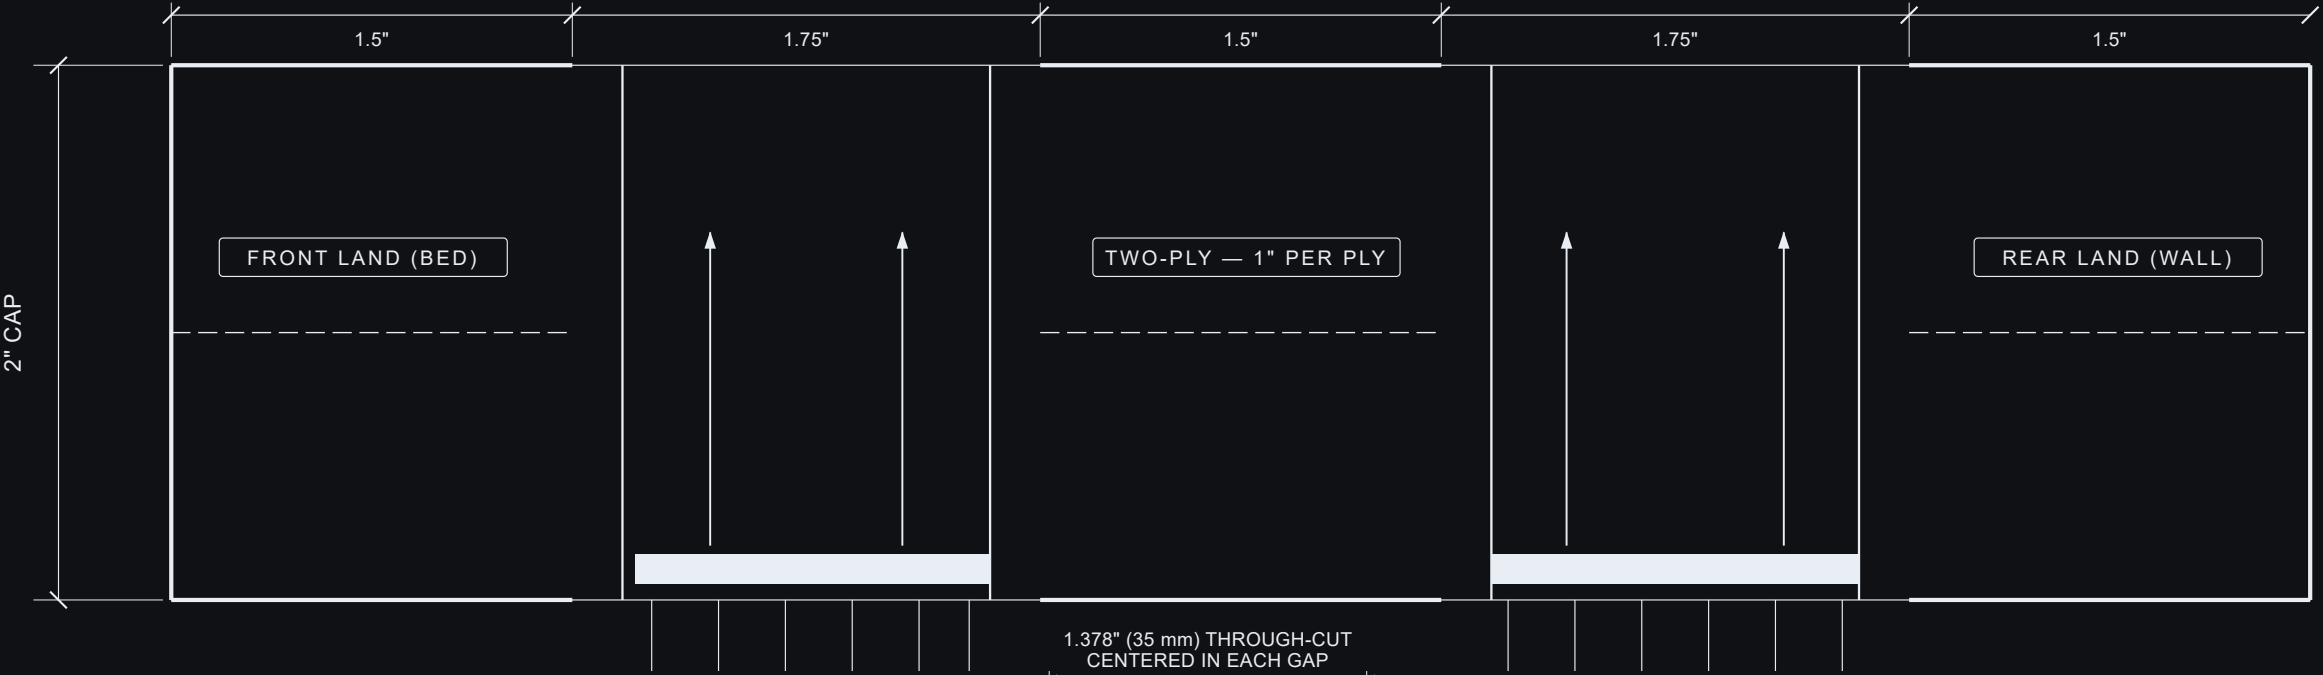

PROJECT	HEIRLOOM BED	SHEET 1 OF 1
DRAWING NO.	TopCap-LED_Blueprint	
LAST UPDATE	2026-06-12 1:00 AM	REV 1.16