


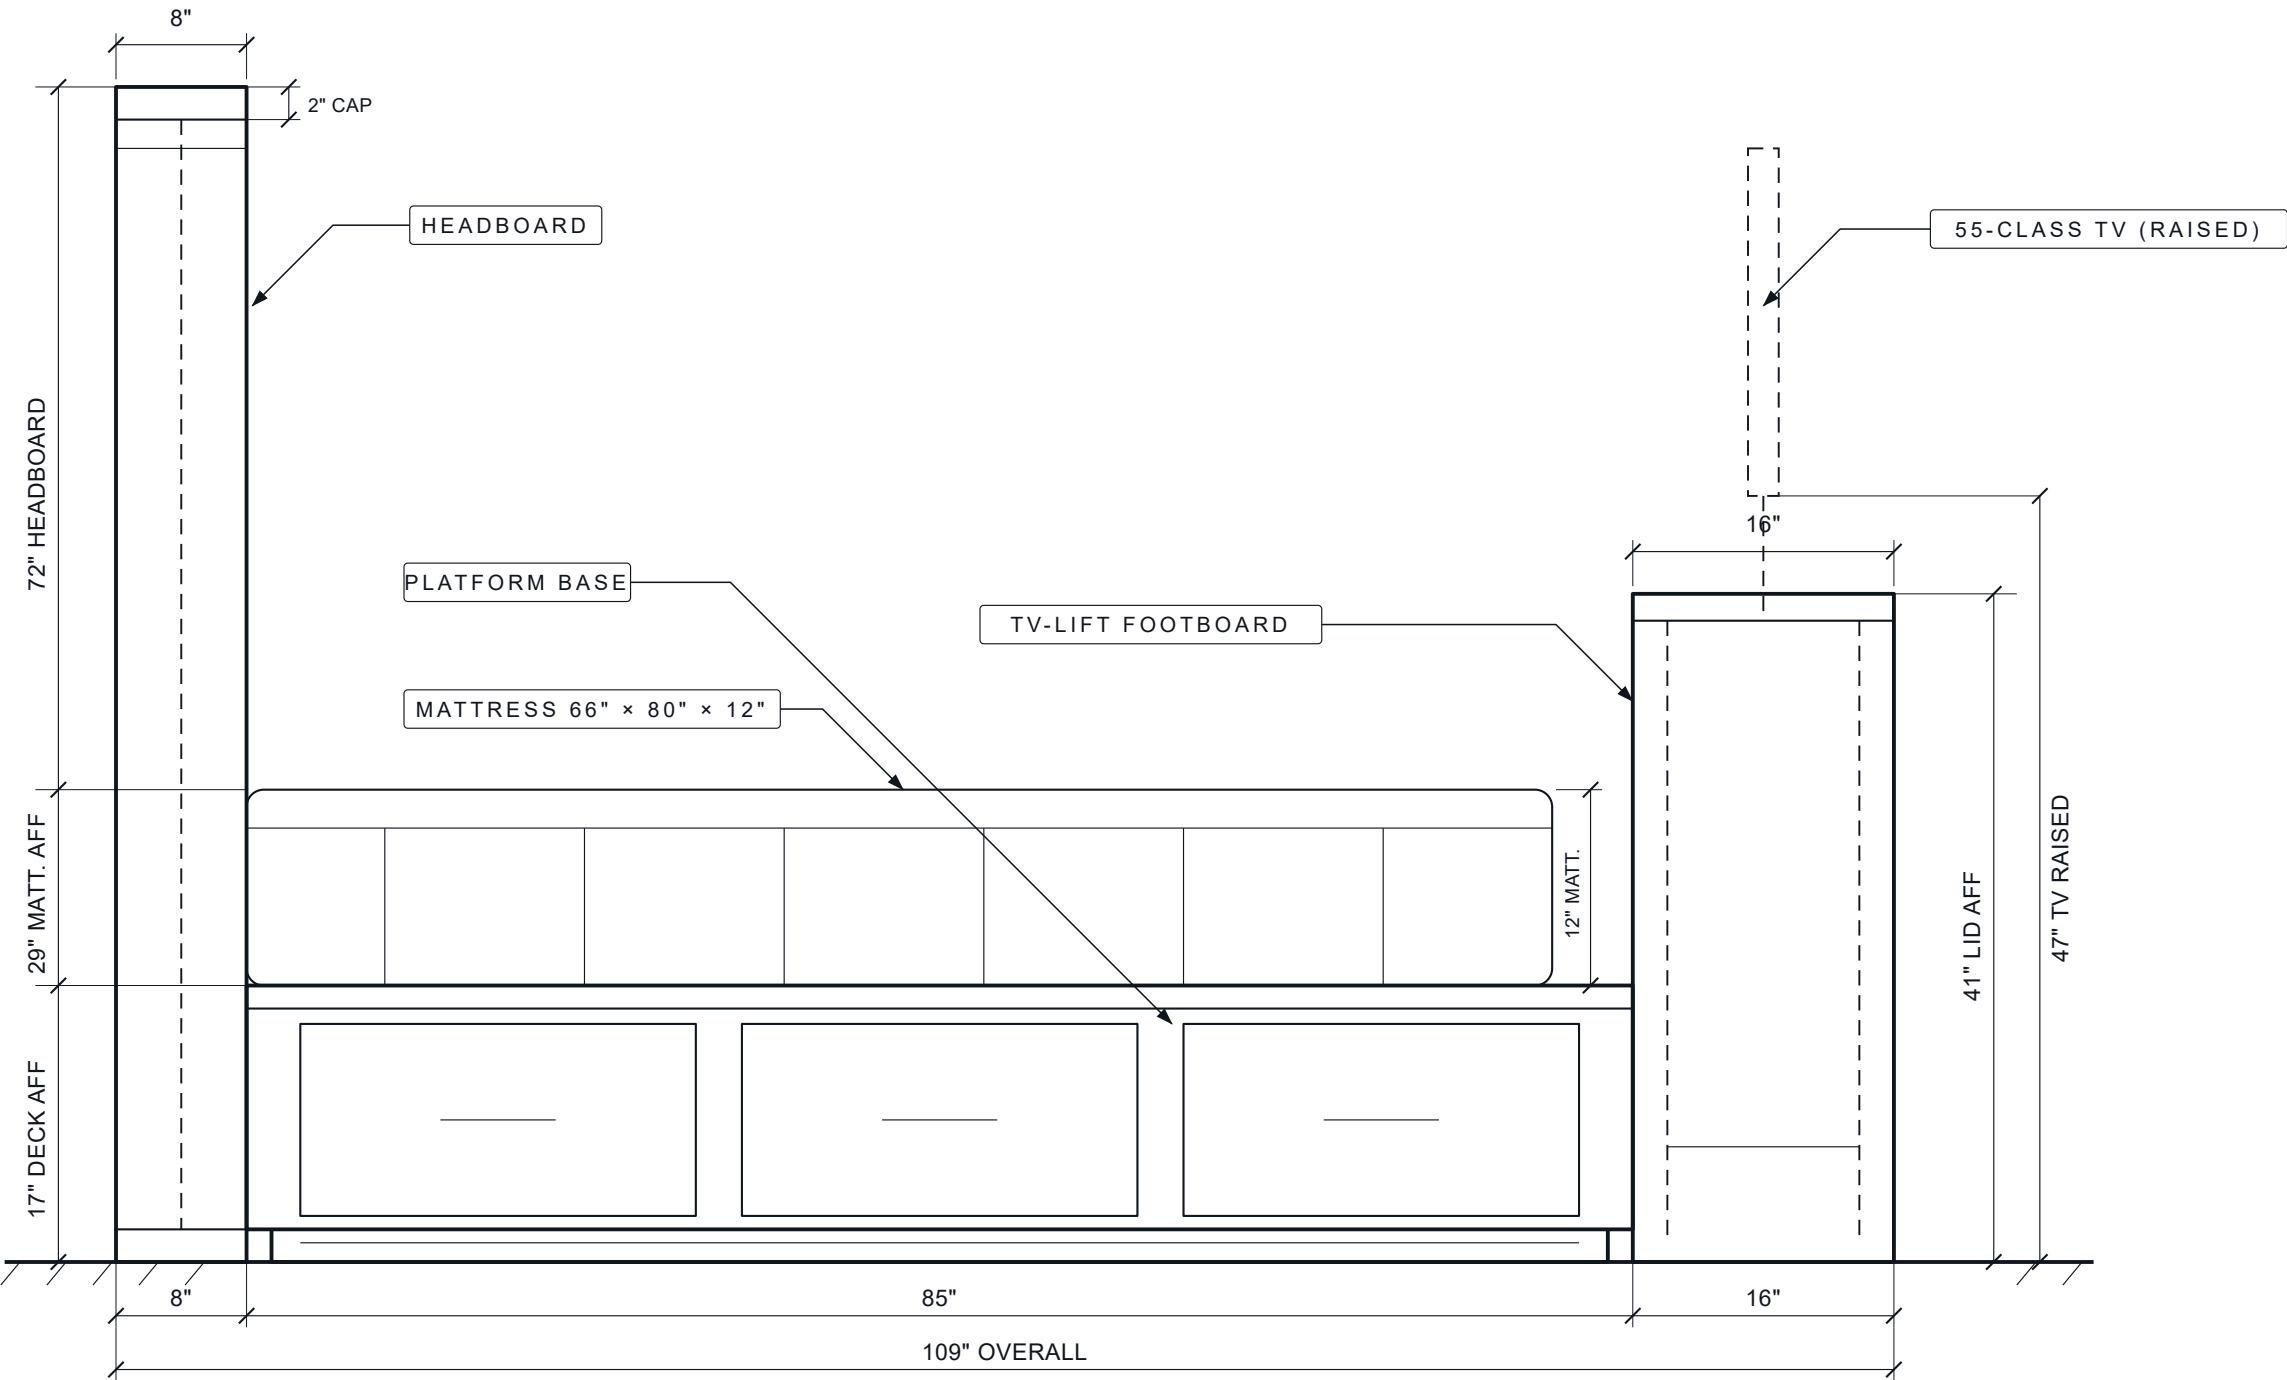

SIDE ELEVATION

- GENERAL NOTES
- 1. All dimensions in inches ("). AFF = above finished floor.
 - 2. Figured dimensions govern — DO NOT scale from the print.

PROJECT HEIRLOOM BED	
DRAWING Side Elevation	DRAWING NO. Bed-Side_Blueprint
REV 1.2	SHEET 1 OF 1