



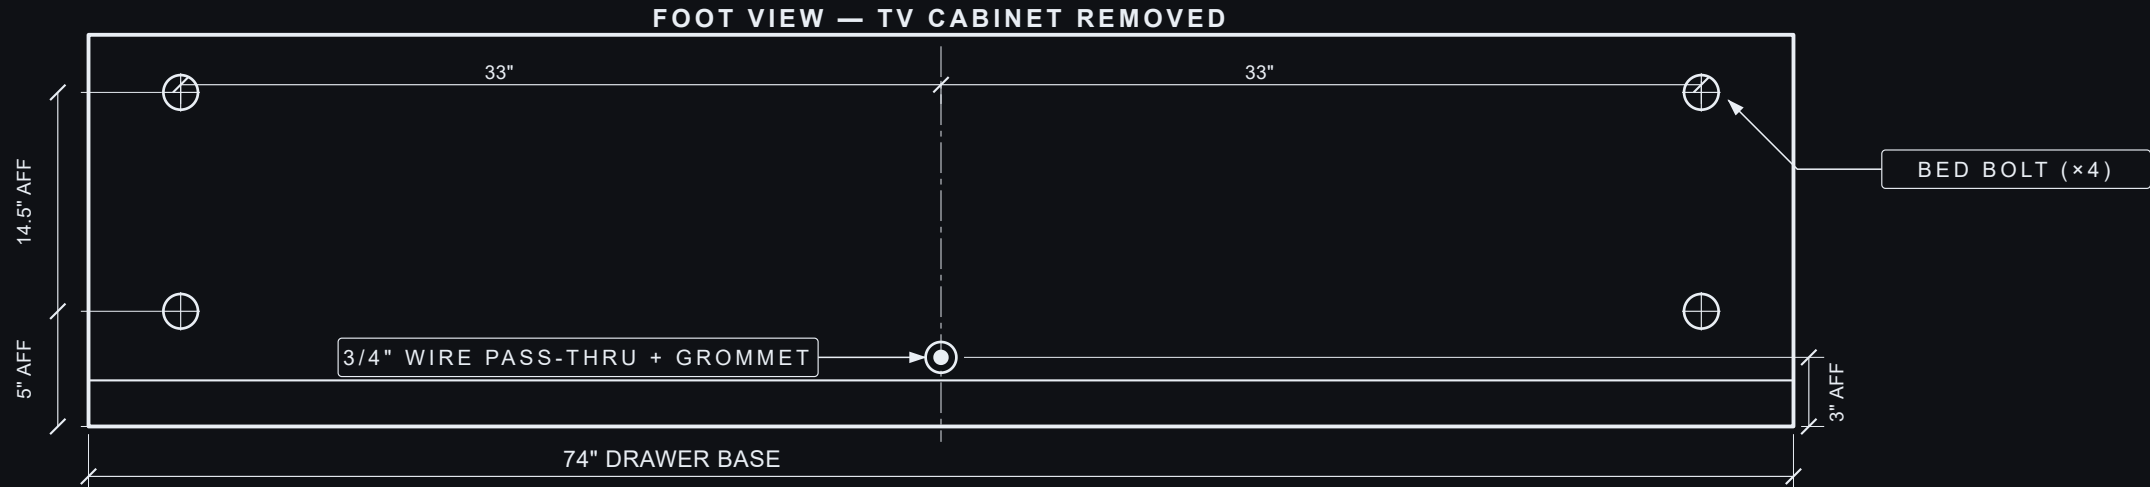

FOOT FACE — MOUNTING PATTERN

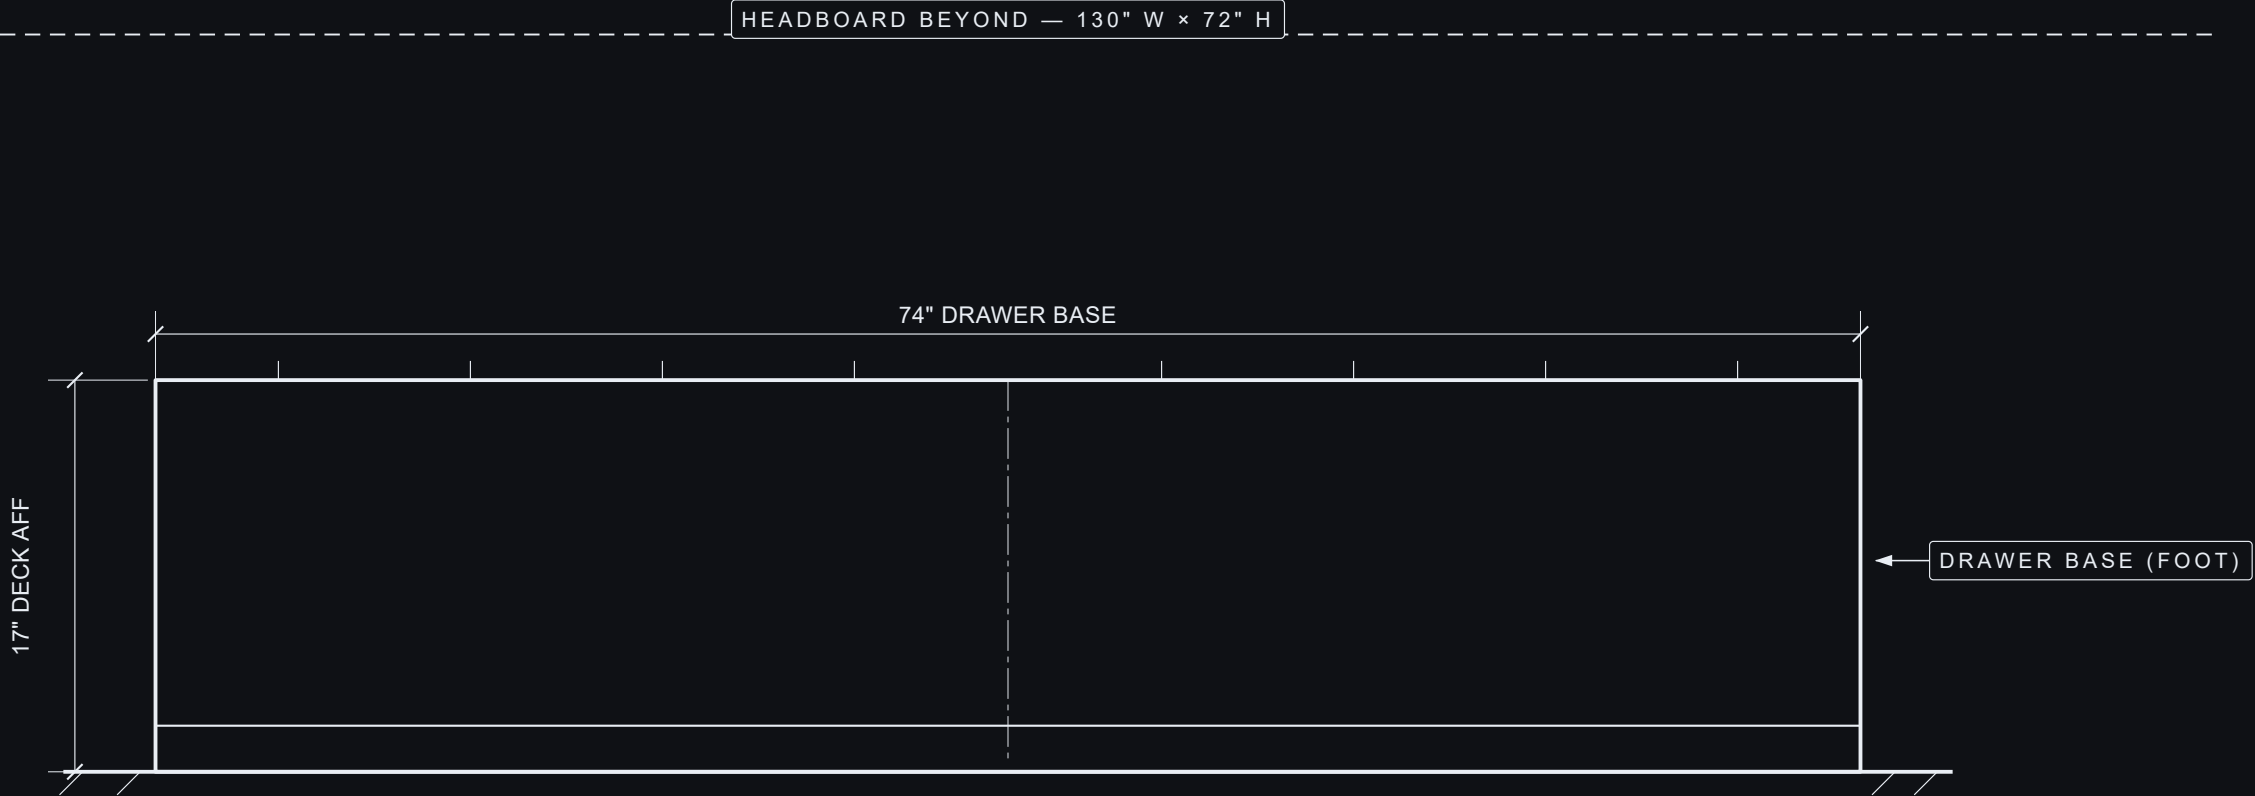

PROJECT HEIRLOOM BED	
DRAWING Front (Foot End)	DRAWING NO. Bed-Front_Blueprint
REV 3.0	SHEET 1 OF 1