


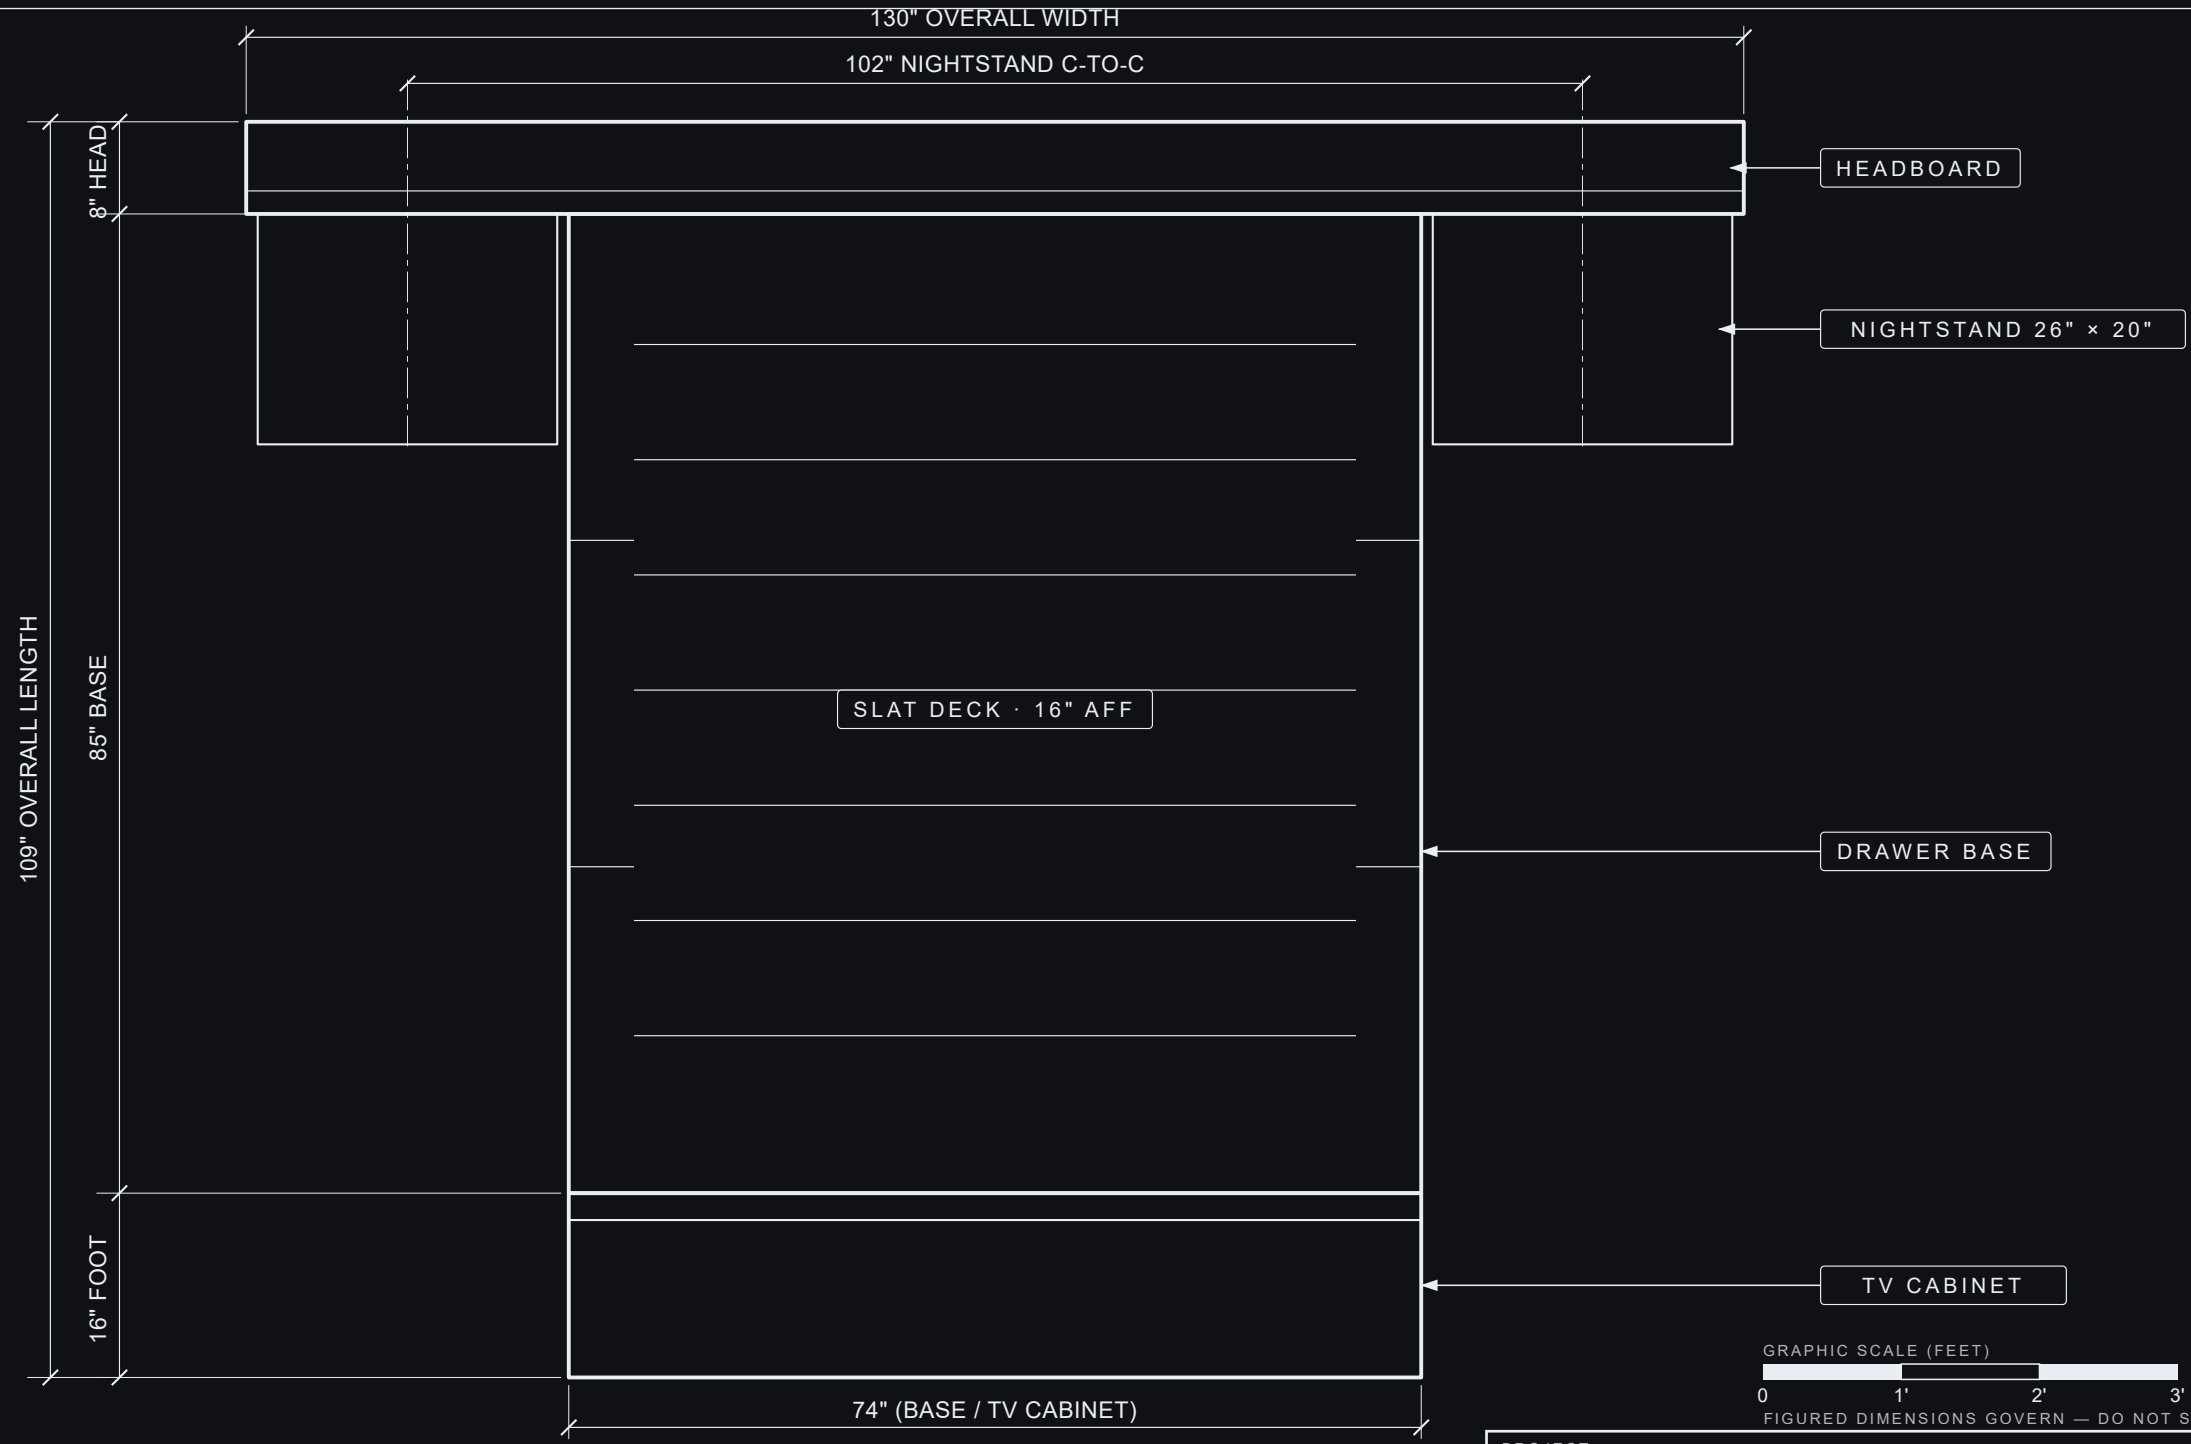

TOP VIEW



PROJECT HEIRLOOM BED	
DRAWING Top view	DRAWING NO. Bed-Top_Blueprint
REV 2.6	SHEET 1 OF 1