



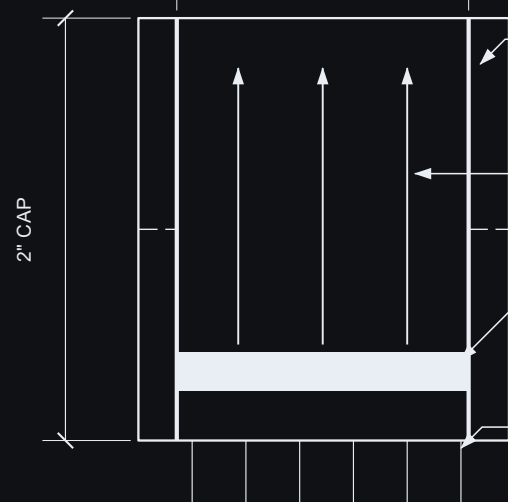

DETAIL A — ENLARGED CHANNEL

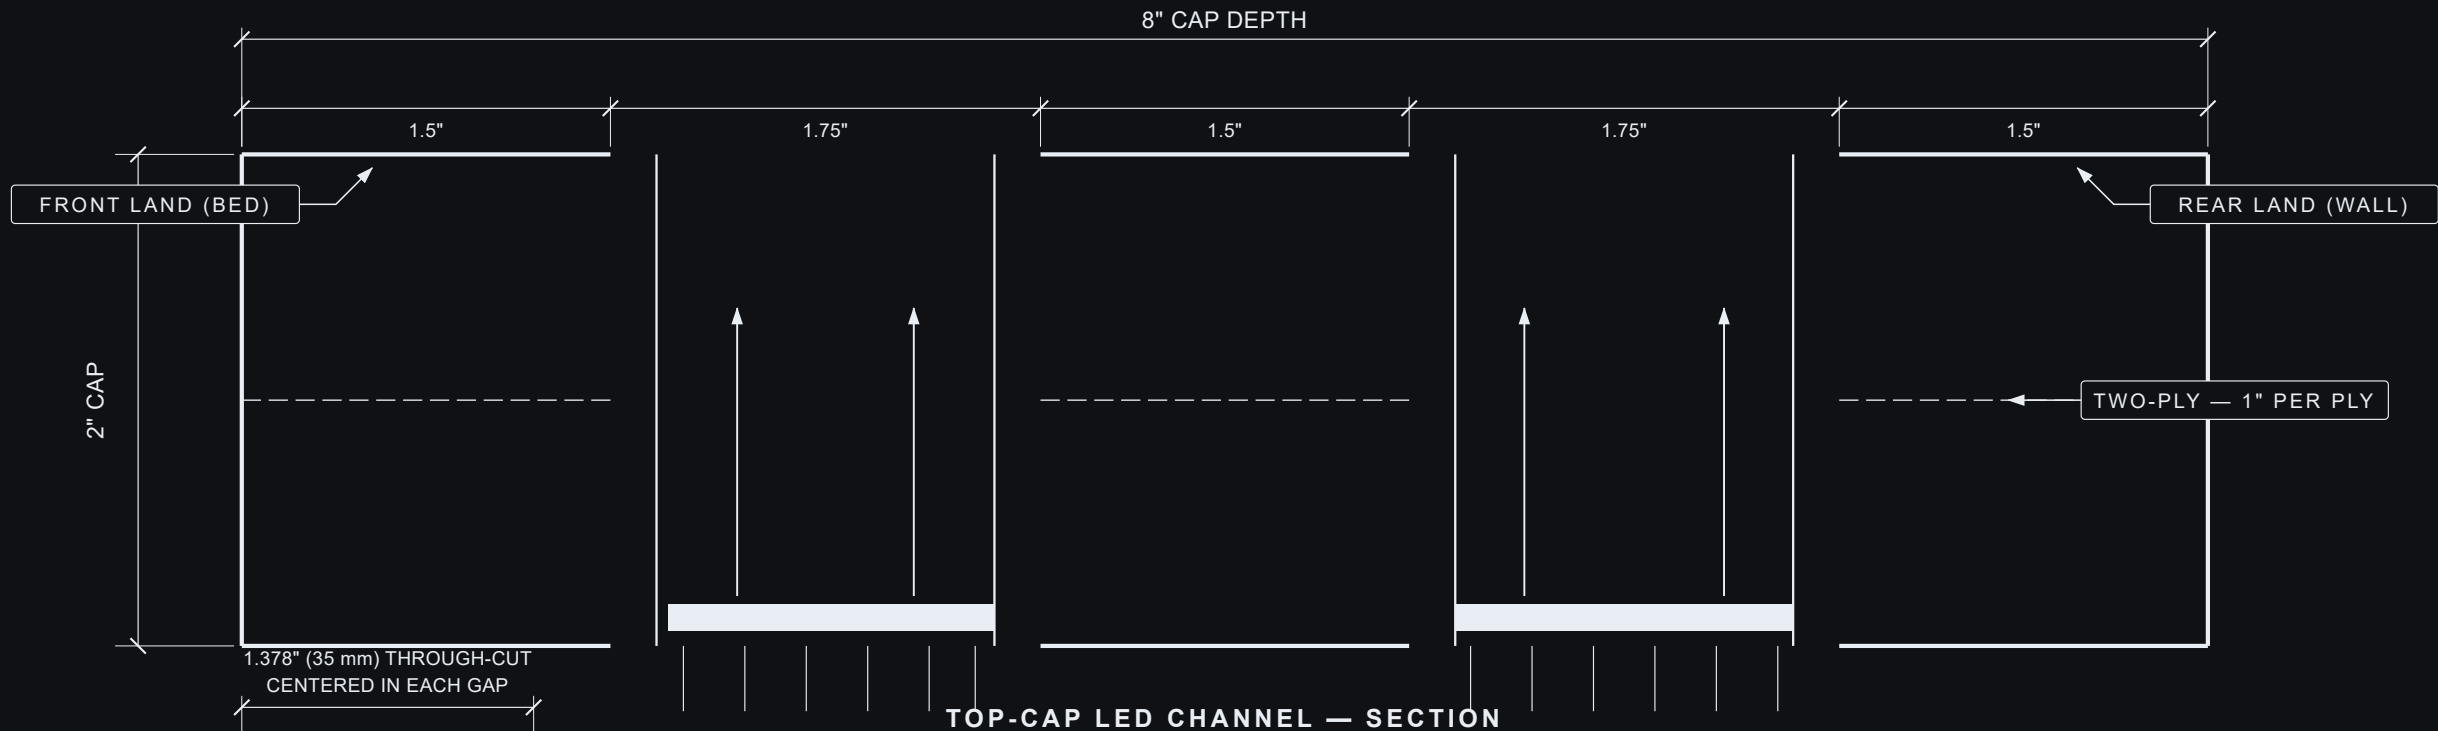

PROJECT HEIRLOOM BED	
DRAWING Top-Cap LED Channel	DRAWING NO. TopCap-LED_Blueprint
REV 1.5	SHEET 1 OF 1